CROSS MOD
CYPRESS_CC

INDEX

A0.0	COVER SHEET
A1.0	FLOOR PLAN
A1.1	LIGHTING AND FLOOR REGISTER LAYOUT
A2.0	ELEVATIONS - STANDARD
A3.0	INTERIOR DETAILS - KITCHEN
A3.1	INTERIOR DETAILS - KITCHEN
A3.2	INTERIOR DETAILS - BATHS
	SALESLIT

GENERAL NOTES

1. THIS PACKAGE IS INTENDED TO RELAY DESIGN INTENT AND IS NOT FOR CONSTRUCTION.
2. PLEASE CONTACT ANDY HUTSELL AT ANDY.HUTSELL@CLAYTONHOMES.COM WITH QUESTIONS REGARDING THESE DRAWINGS.
3. APPLIANCES, FIXTURES AND HARDWARE ARE SHOWN FOR REFERENCE - COORDINATE WITH SPECIFICATIONS.
4. ALL WINDOWS INTENDED TO BE MOUNTED AT THE SAME HEAD HEIGHT UNLESS NOTED OTHERWISE.

SYMBOLS AND ABBREVIATIONS

CLG	CEILING
DR	DOOR
EF	EXHAUST FAN
FLR	FLOOR
MNT	MOUNT
OPT	OPTIONAL
RAG	RETURN AIR GRILLE
SEP	STANDARD ELECTRIC PANEL
SGD	SLIDING GLASS DOOR

Clayton Built

MODEL NAME
CYPRESS_CC
MODEL NO.
BLN-1666-22-1
BOX SIZE
16' x 66'
MODEL SQ. FT.
990

DATE PRINTED
8/15/2025
SCALE
N.T.S.
* UNLESS OTHERWISE NOTED
PLAN NO.
BLN-1666-32-1_CYPRESS_CC
SHEET NAME
COVER SHEET
SHEET NO.
A0.0.

File Path:Z:\DesignCenter\Architecture\CrossMod\DWG Files\CHIEF CARES\1666_CYPRESS_CC\BLN-1666-32-1_CYPRESS_CC.dwg, Last Saved By:Taylorjo, Saved Date:8/15/2025 6:05 PM

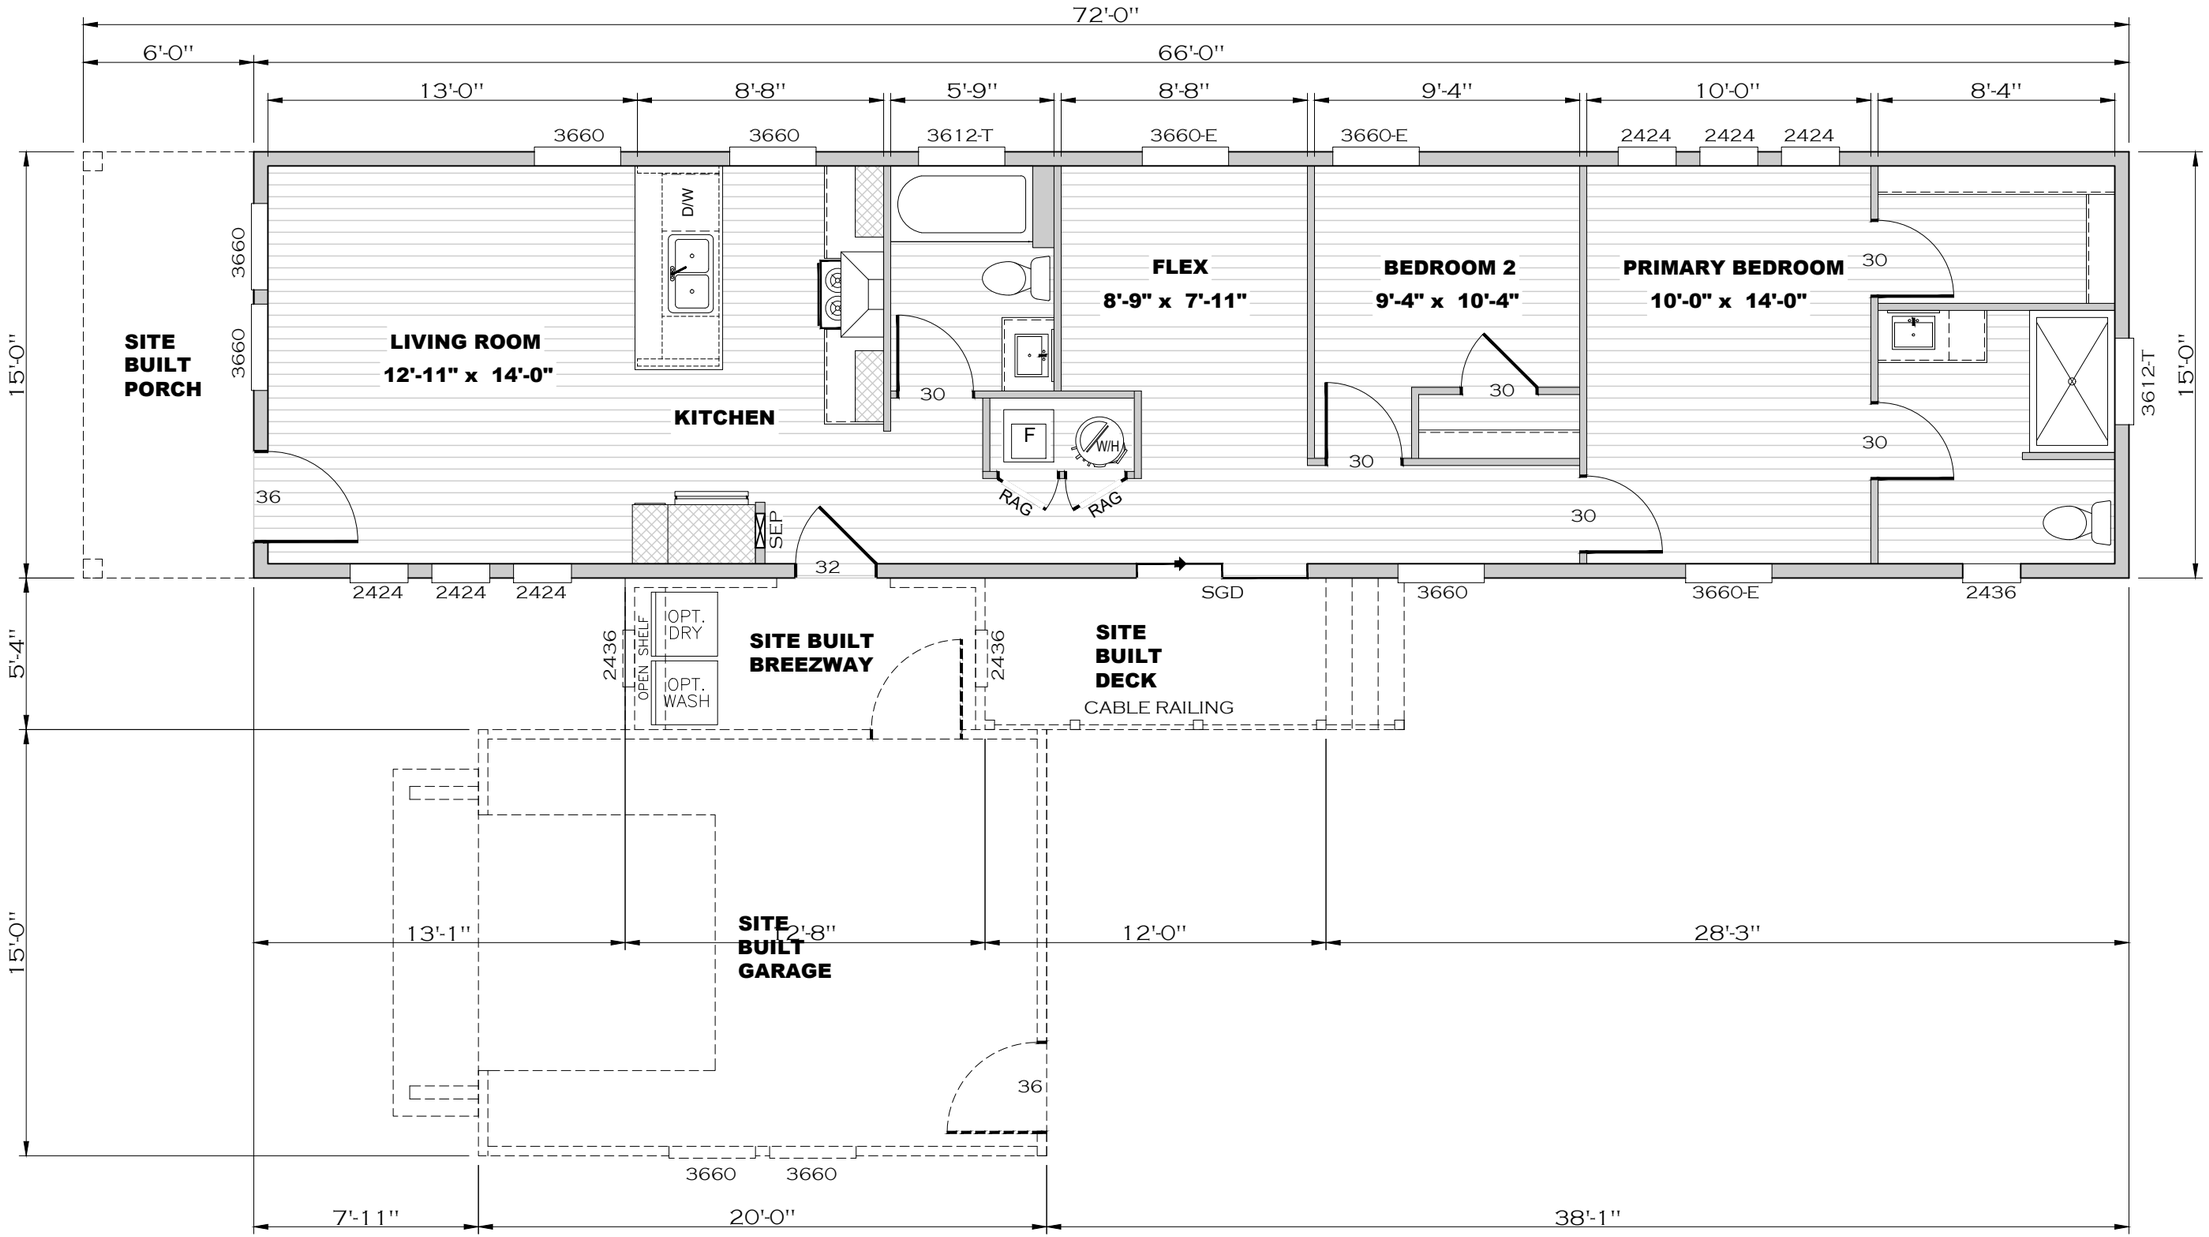

FLOOR PLAN

Clayton Built

MODEL NAME
CYPRESS_CC

MODEL NO.
BLN-1666-22-1

MODEL SQ. FT.
990

BOX SIZE
16' x 66'

DATE PRINTED
8/15/2025

SCALE
3/16"=1'
* UNLESS OTHERWISE NOTED

PLAN NO.
BLN-1666-32-1_CYPRESS_CC

SHEET NAME
FLOOR PLAN

SHEET NO.
A1.0.

File Path: Z:\DesignCenter\Architecture\CrossMod\DWG Files\CHIEF CARES\1666_CYPRESS_CC\BLN-1666-32-1_CYPRESS_CC.dwg, Last Saved By:Taylorjo, Saved Date:8/15/2025 6:05 PM

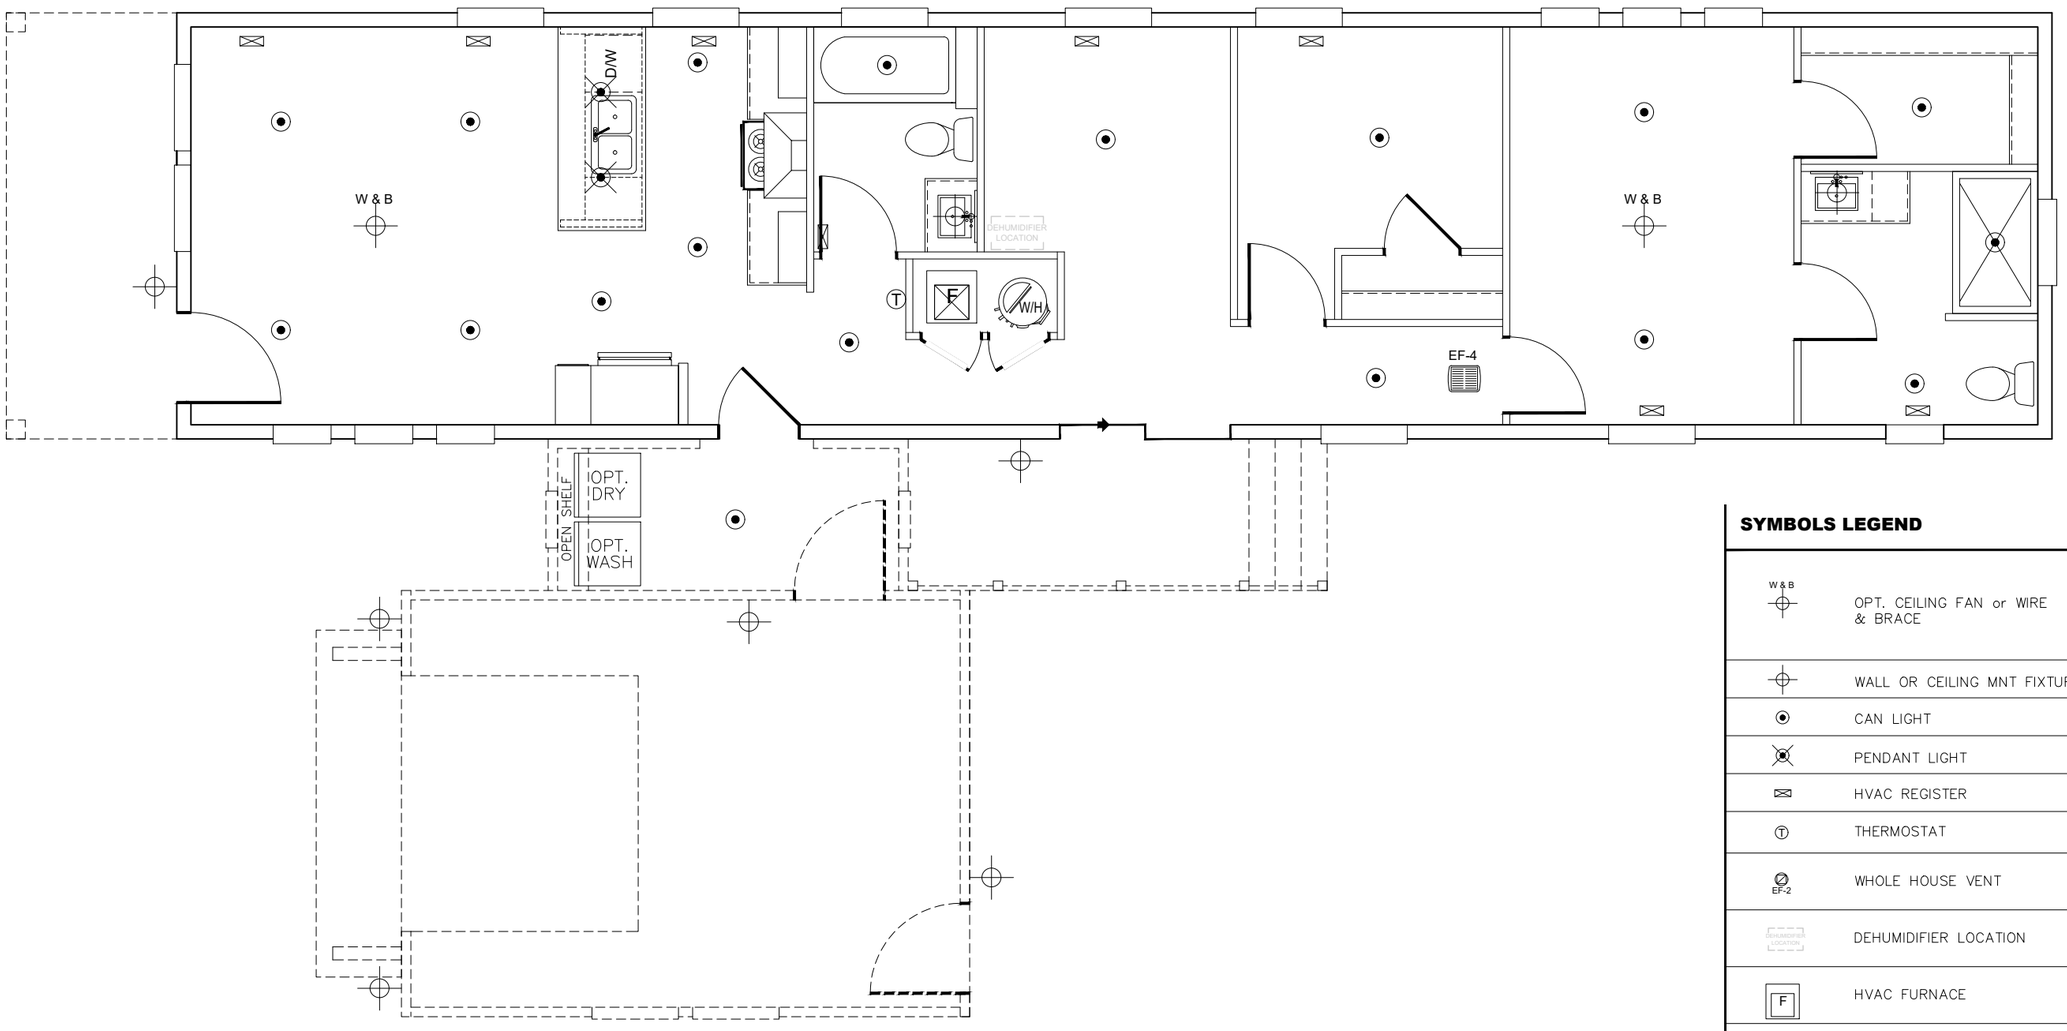

LIGHTING AND FLOOR REGISTER LAYOUT

SYMBOLS LEGEND

W & B	OPT. CEILING FAN or WIRE & BRACE
	WALL OR CEILING MNT FIXTURE
	CAN LIGHT
	PENDANT LIGHT
	HVAC REGISTER
T	THERMOSTAT
EF-2	WHOLE HOUSE VENT
DEHUMIDIFIER LOCATION	DEHUMIDIFIER LOCATION
F	HVAC FURNACE
W/H	WATER HEATER
ATTIC ACCESS	ATTIC ACCESS

NOTES:
1. ALL SYMBOLS MAY NOT BE APPLICABLE TO ALL PROJECTS.

Clayton Built

MODEL NAME
CYPRESS_CC

MODEL NO.
BLN-1666-22-1

MODEL SQ. FT.
990

BOX SIZE
16' x 66'

DATE PRINTED
8/15/2025

SCALE
3/16"=1'
* UNLESS OTHERWISE NOTED

PLAN NO.
BLN-1666-32-1_CYPRESS_CC

SHEET NAME
ELEC. PLAN

SHEET NO.
A1.1.

File Path:Z:\DesignCenter\Architecture\CrossMod\DWG Files\CHIEF CARES\1666_CYPRESS_CC\BLN-1666-32-1_CYPRESS_CC.dwg, Last Saved By:Taylorjo, Saved Date:8/15/2025 6:05 PM

FRONT ELEVATION

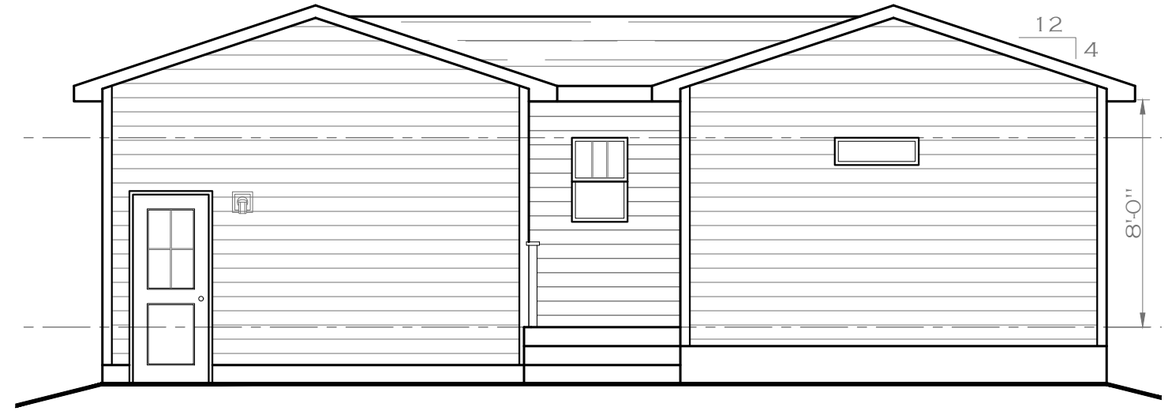

REAR ELEVATION

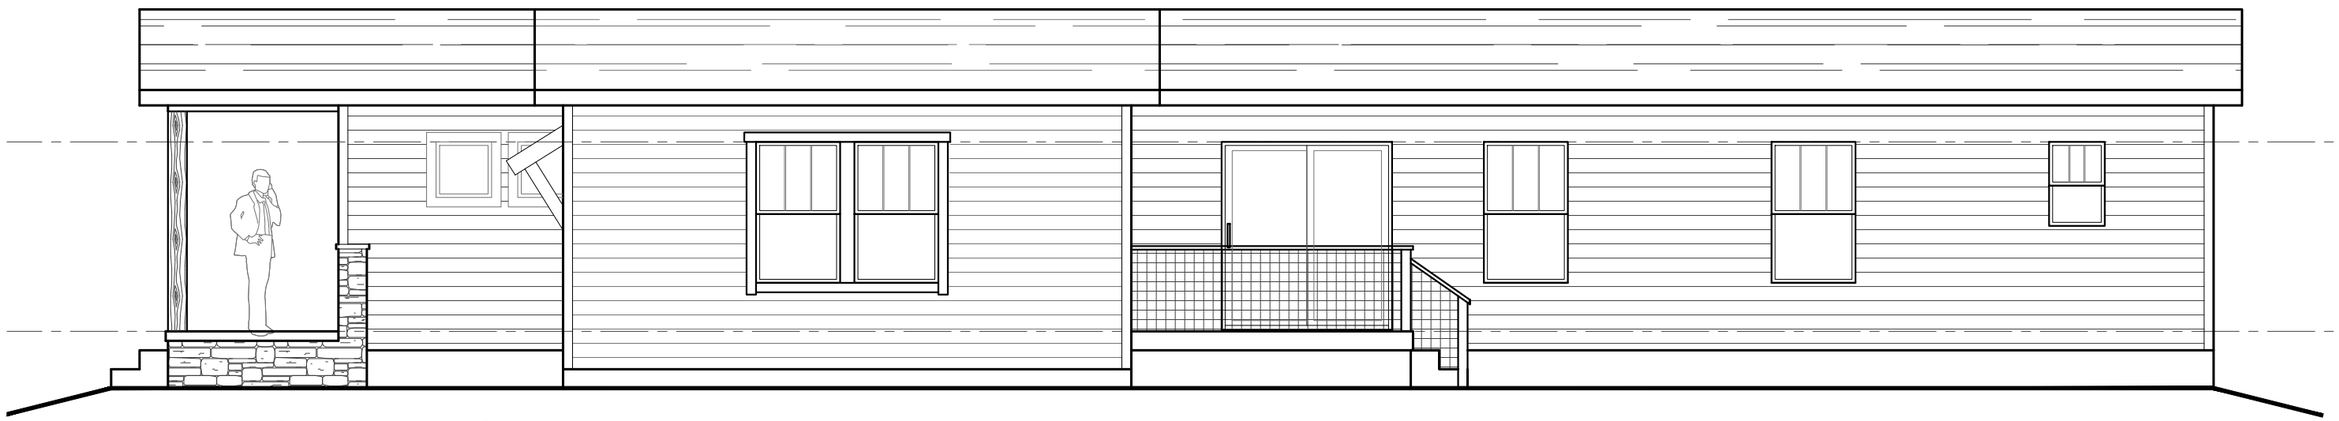

RIGHT SIDE ELEVATION

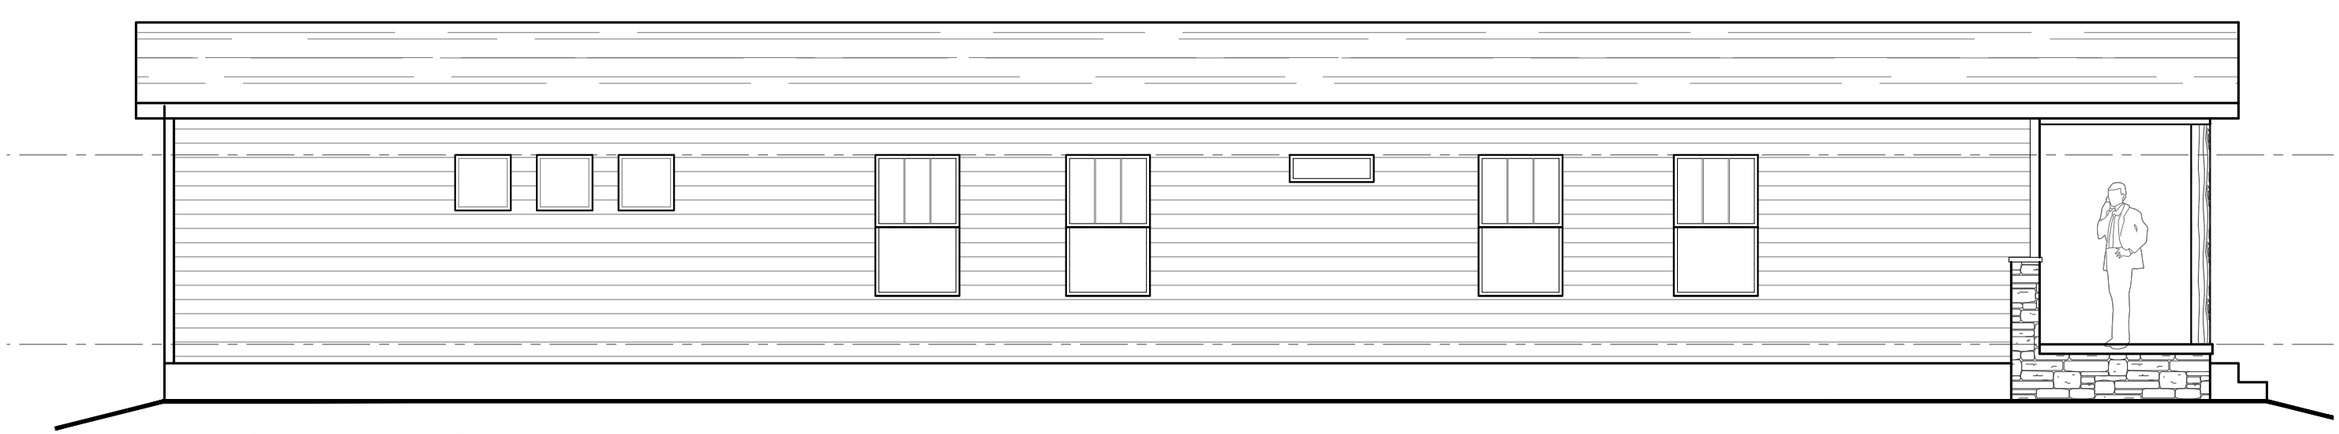

LEFT SIDE ELEVATION

Clayton Built

MODEL NAME
CYPRESS_CC

MODEL NO.
BLN-1666-22-1

MODEL SQ. FT.
990

BOX SIZE
16' x 66'

DATE PRINTED
8/15/2025

SCALE
1/8"=1'
* UNLESS OTHERWISE NOTED

PLAN NO.
BLN-1666-32-1_CYPRESS_CC

SHEET NAME
EXTERIOR ELEVATION

SHEET NO.
A2.0.

File Path:Z:\DesignCenter\Architecture\CrossMod\DWG Files\CHIEF CARES\1666_CYPRESS_CC\BLN-1666-32-1_CYPRESS_CC.dwg, Last Saved By:Taylorjo, Saved Date:8/15/2025 6:05 PM

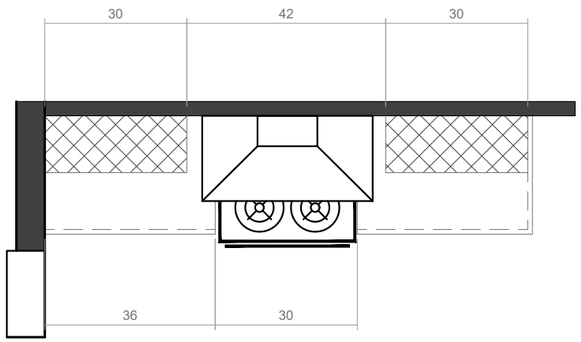

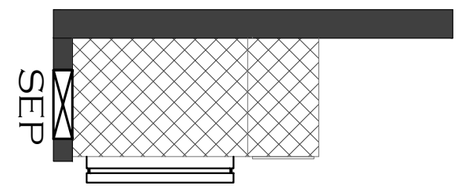

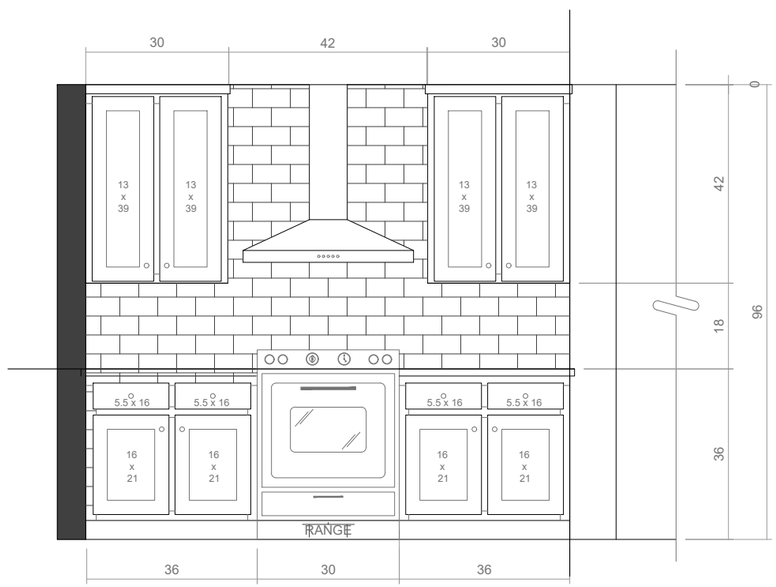

KITCHEN ELEVATION @ OVEN WALL

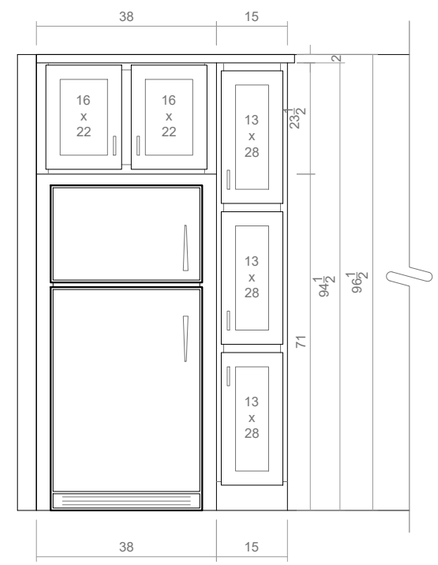

KITCHEN ELEVATION @ REFRIGERATOR

Clayton Built

MODEL NAME
CYPRESS_CC

MODEL NO.
BLN-1666-22-1

BOX SIZE
16' x 66'

MODEL SQ. FT.
990

DATE PRINTED
8/15/2025

SCALE
3/8"=1'
* UNLESS OTHERWISE NOTED

PLAN NO.
BLN-1666-32-1_CYPRESS_CC

SHEET NAME
CABINETS KITCHEN

SHEET NO.
A3.0.

File Path:Z:\DesignCenter\Architecture\CrossMod\DWG Files\CHIEF CARES\1666_CYPRESS_CC\BLN-1666-32-1_CYPRESS_CC.dwg, Last Saved By:Taylorjo, Saved Date:8/15/2025 6:05 PM

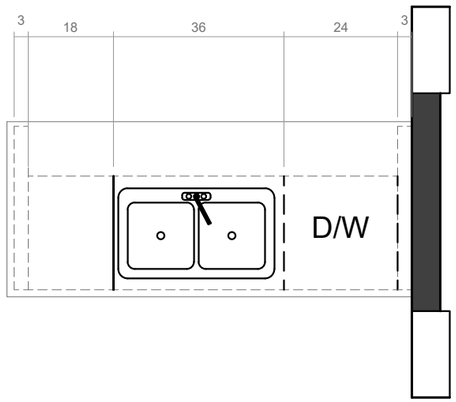

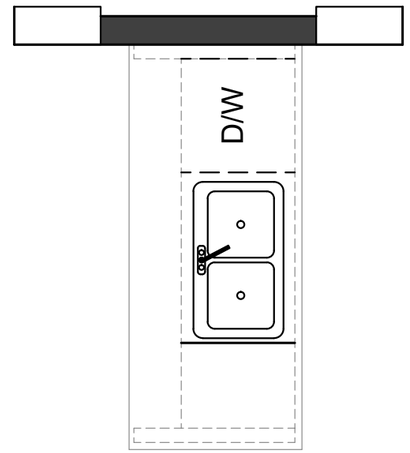

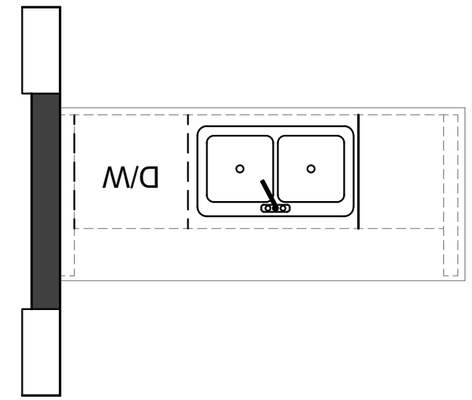

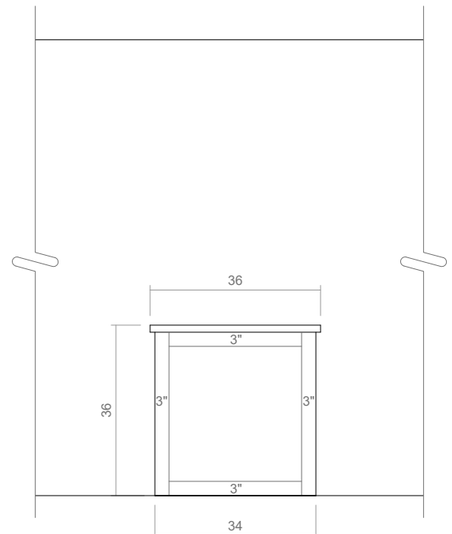

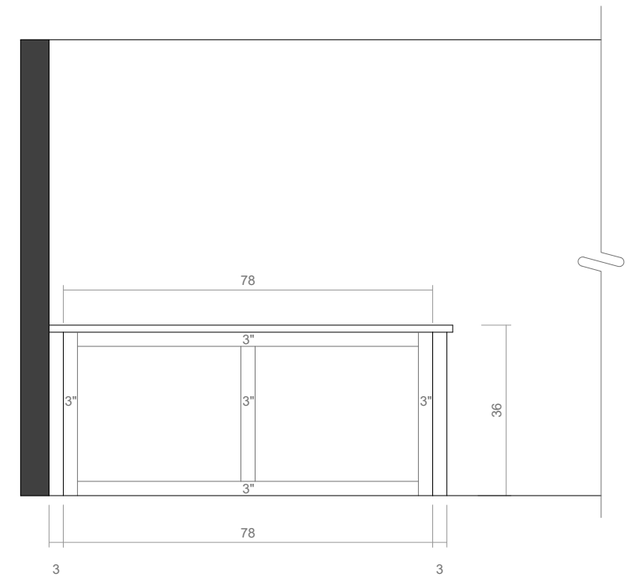

ISLAND ELEVATIONS

$\frac{3}{8}$" = 1'-0"

Clayton Built

MODEL NAME
CYPRESS_CC

MODEL NO.
BLN-1666-22-1

MODEL SQ. FT.
990

BOX SIZE
16' x 66'

DATE PRINTED
8/15/2025

SCALE
VARIES
* UNLESS OTHERWISE NOTED

PLAN NO.
BLN-1666-32-1_CYPRESS_CC

SHEET NAME
CABINETS KITCHEN

SHEET NO.
A3.1.

File Path:Z:\DesignCenter\Architecture\CrossMod\DWG Files\CHIEF CARES\1666_CYPRESS_CC\BLN-1666-32-1_CYPRESS_CC.dwg, Last Saved By:Taylorjo, Saved Date:8/15/2025 6:05 PM

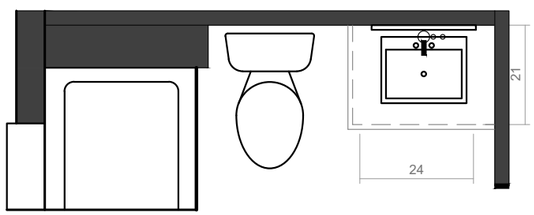

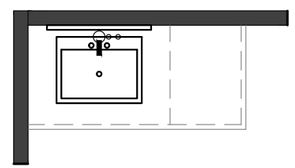

HALL BATH ELEVATION

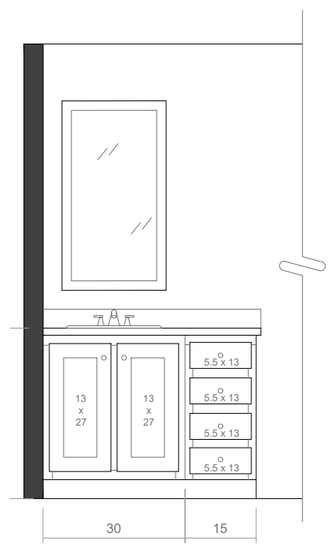

PRIMARY BATH VANITY ELEVATION

Clayton Built

MODEL NAME
CYPRESS_CC

MODEL NO.
BLN-1666-22-1

BOX SIZE
16' x 66'

MODEL SQ. FT.
990

DATE PRINTED
8/15/2025

SCALE
3/8"=1'
* UNLESS OTHERWISE NOTED

PLAN NO.
BLN-1666-32-1_CYPRESS_CC

SHEET NAME
CABINETS BATH

SHEET NO.
A3.2

File Path:Z:\DesignCenter\Architecture\CrossMod\DWG Files\CHIEF CARES\1666_CYPRESS_CC\BLN-1666-32-1_CYPRESS_CC.dwg, Last Saved By:Taylorjo, Saved Date:8/15/2025 6:05 PM

"CYPRESS_CC"

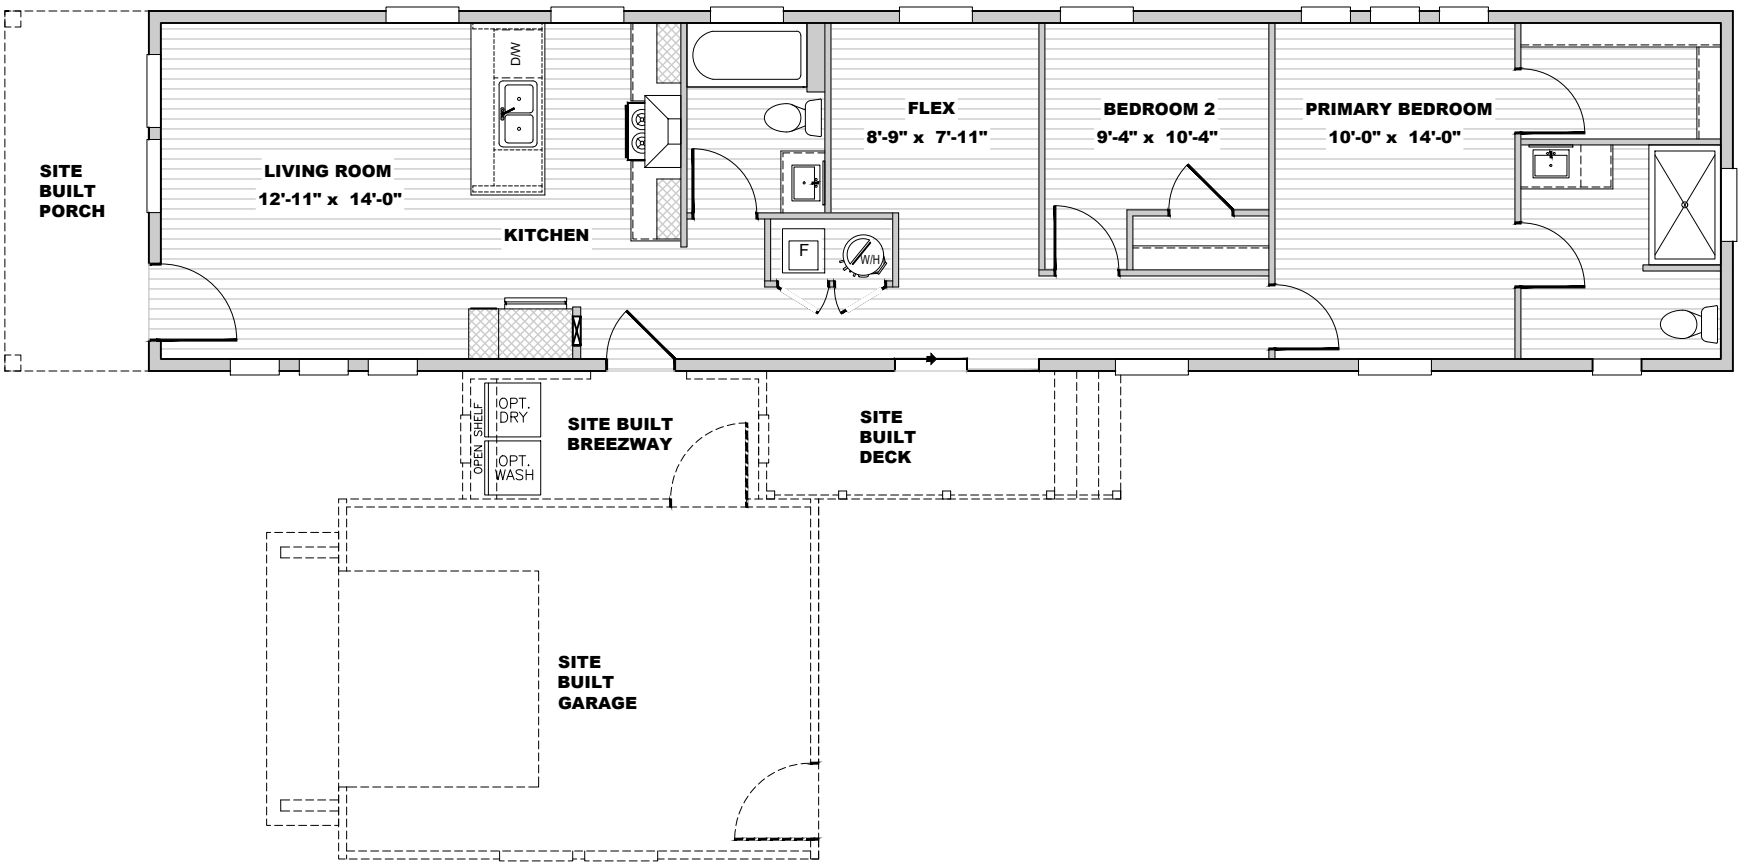

MODEL #BLN-1666-22-1 SQ.FT. 990 DRAWING # BLN-1666-32-1_CYPRESS_CC

File Path:Z:\DesignCenter\Architecture\CrossMod\DWG Files\CHIEF CARES\1666_CYPRESS_CC\BLN-1666-32-1_CYPRESS_CC.dwg, Last Saved By:Taylorjo, Saved Date:8/15/2025 6:05 PM, Date Printed:8/15/25 6:06 PM

NO BREEZWAY
CYPRESS_CC

INDEX

A0.1	COVER SHEET
A4.0	FLOOR PLAN
A4.1	LIGHTING AND FLOOR REGISTER LAYOUT
A4.2	ELEVATIONS SALESLIT (2)

GENERAL NOTES

1. THIS PACKAGE IS INTENDED TO RELAY DESIGN INTENT AND IS NOT FOR CONSTRUCTION.
2. PLEASE CONTACT ANDY HUTSELL AT ANDY.HUTSELL@CLAYTONHOMES.COM WITH QUESTIONS REGARDING THESE DRAWINGS.
3. APPLIANCES, FIXTURES AND HARDWARE ARE SHOWN FOR REFERENCE - COORDINATE WITH SPECIFICATIONS.
4. ALL WINDOWS INTENDED TO BE MOUNTED AT THE SAME HEAD HEIGHT UNLESS NOTED OTHERWISE.

SYMBOLS AND ABBREVIATIONS

CLG	CEILING
DR	DOOR
EF	EXHAUST FAN
FLR	FLOOR
MNT	MOUNT
OPT	OPTIONAL
RAG	RETURN AIR GRILLE
SEP	STANDARD ELECTRIC PANEL
SGD	SLIDING GLASS DOOR

Clayton Built

MODEL NAME
CYPRESS_CC
MODEL NO.
BLN-1666-22-1
BOX SIZE
16' x 66'
MODEL SQ. FT.
990

DATE PRINTED
8/15/2025
SCALE
N.T.S.
* UNLESS OTHERWISE NOTED
PLAN NO.
BLN-1666-32-1_CYPRESS_CC
SHEET NAME
COVER SHEET
SHEET NO.
A0.1.

File Path:Z:\DesignCenter\Architecture\CrossMod\DWG Files\CHIEF CARES\1666_CYPRESS_CC\BLN-1666-32-1_CYPRESS_CC.dwg, Last Saved By:Taylorjo, Saved Date:8/15/2025 6:05 PM

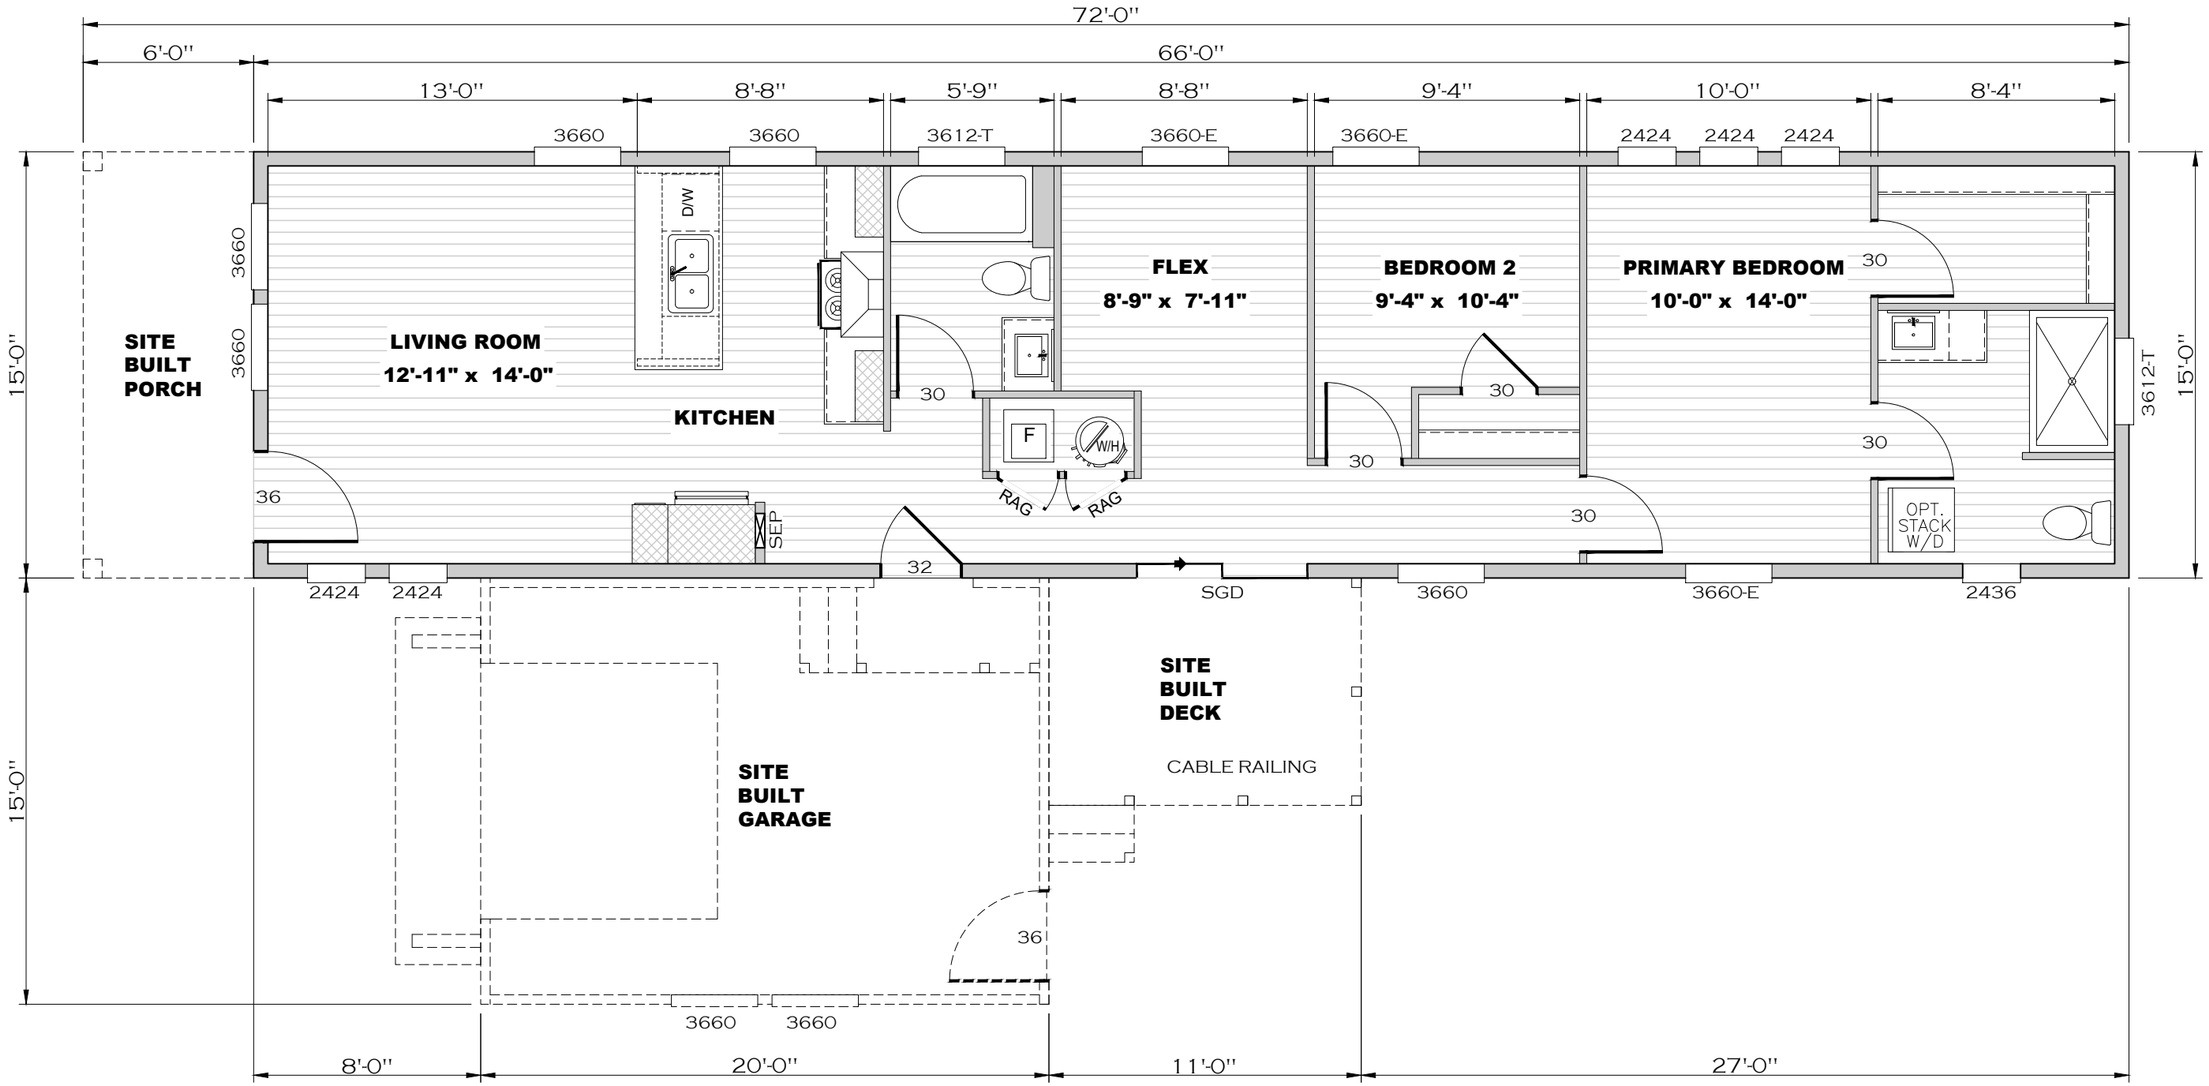

FLOOR PLAN

Clayton Built

MODEL NAME
CYPRESS_CC

MODEL NO.
BLN-1666-22-1

MODEL SQ. FT.
990

BOX SIZE
16' x 66'

DATE PRINTED
8/15/2025

SCALE
3/16"=1'
* UNLESS OTHERWISE NOTED

PLAN NO.
BLN-1666-32-1_CYPRESS_CC

SHEET NAME
FLOOR PLAN

SHEET NO.
A4.0

File Path: Z:\DesignCenter\Architecture\CrossMod\DWG Files\CHIEF CARES\1666_CYPRESS_CC\BLN-1666-32-1_CYPRESS_CC.dwg, Last Saved By:Taylorjo, Saved Date:8/15/2025 6:05 PM

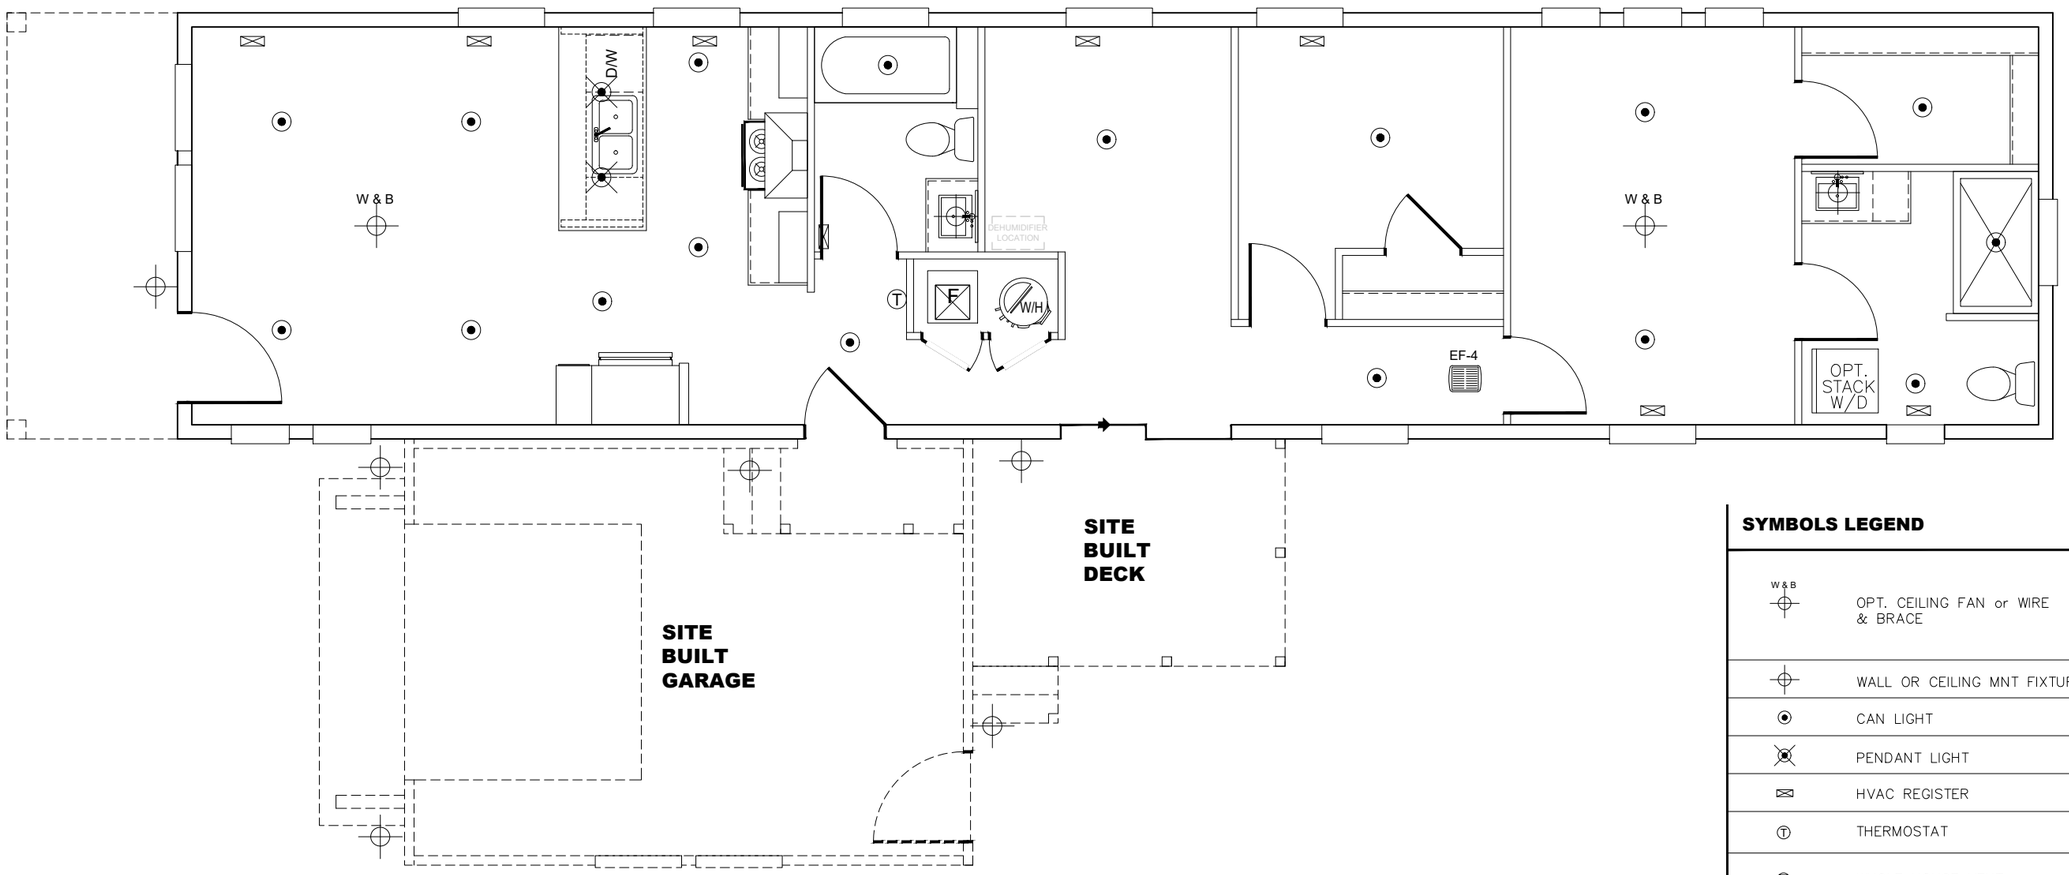

LIGHTING AND FLOOR REGISTER LAYOUT

SYMBOLS LEGEND

W & B	OPT. CEILING FAN or WIRE & BRACE
	WALL OR CEILING MNT FIXTURE
	CAN LIGHT
	PENDANT LIGHT
	HVAC REGISTER
T	THERMOSTAT
EF-2	WHOLE HOUSE VENT
DEHUMIDIFIER LOCATION	DEHUMIDIFIER LOCATION
F	HVAC FURNACE
W/H	WATER HEATER
ATTIC ACCESS	ATTIC ACCESS

NOTES:
1. ALL SYMBOLS MAY NOT BE APPLICABLE TO ALL PROJECTS.

Clayton Built

MODEL NAME
CYPRESS_CC
MODEL NO.
BLN-1666-22-1
MODEL SQ. FT.
990
BOX SIZE
16' x 66'

DATE PRINTED
8/15/2025

SCALE
3/16"=1'
* UNLESS OTHERWISE NOTED

PLAN NO.
BLN-1666-32-1_CYPRESS_CC

SHEET NAME
ELEC. PLAN

SHEET NO.
A4.1.

File Path:Z:\DesignCenter\Architecture\CrossMod\DWG Files\CHIEF CARES\1666_CYPRESS_CC\BLN-1666-32-1_CYPRESS_CC.dwg, Last Saved By:Taylorjo, Saved Date:8/15/2025 6:05 PM

FRONT ELEVATION (NO BREEZWAY VERSION)

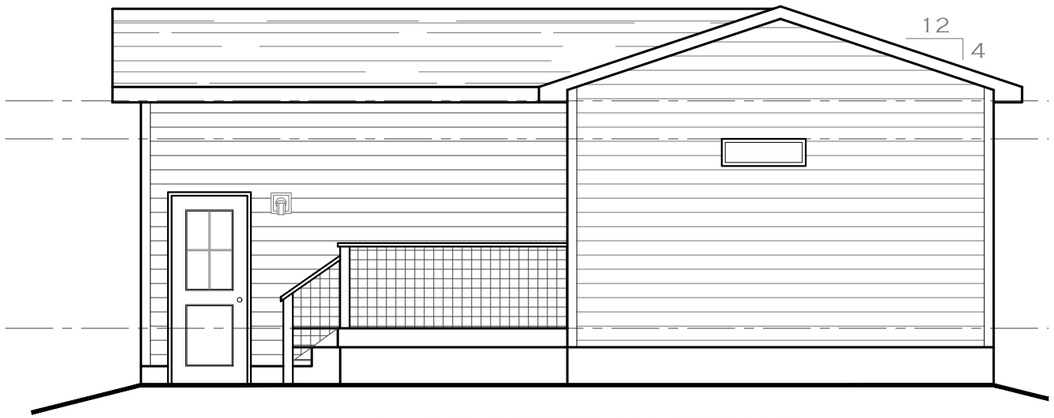

REAR ELEVATION (NO BREEZWAY VERSION)

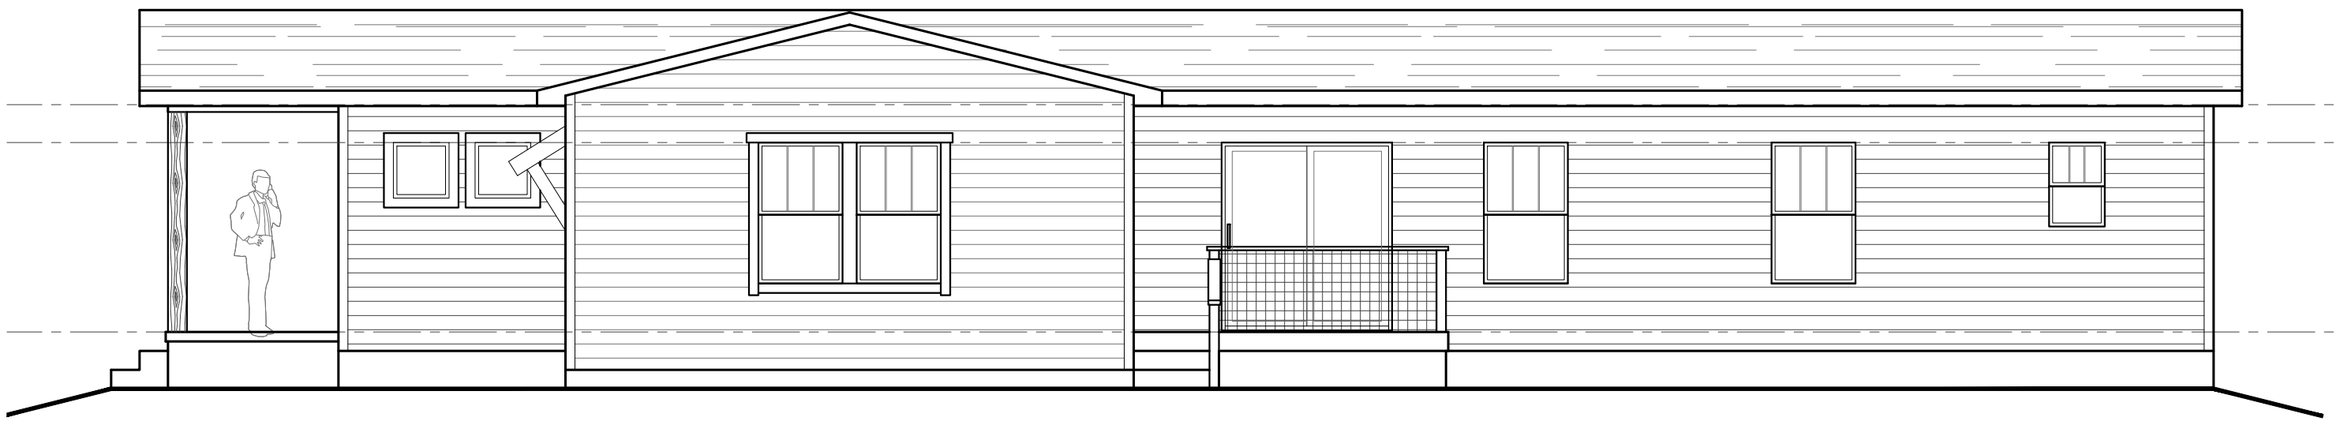

RIGHT SIDE ELEVATION (NO BREEZWAY VERSION)

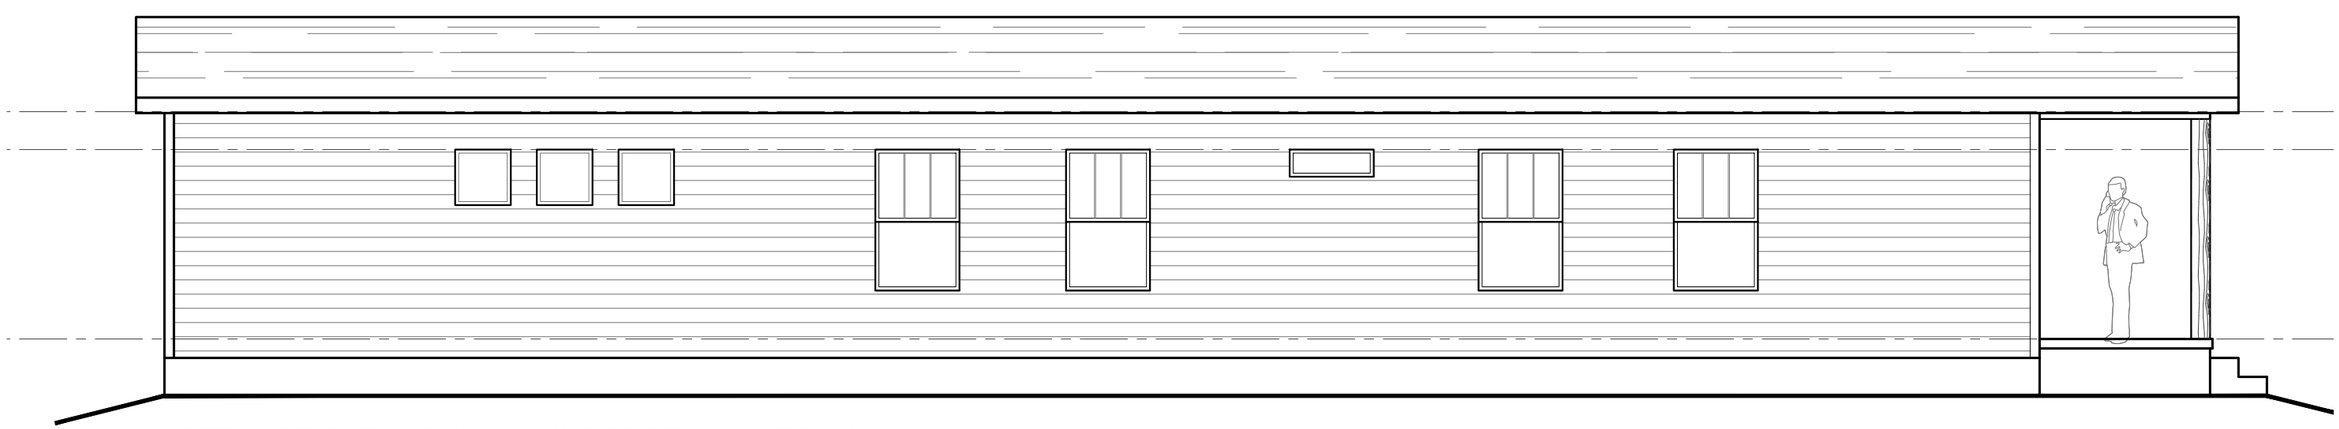

LEFT SIDE ELEVATION (NO BREEZWAY VERSION)

Clayton Built

MODEL NAME
CYPRESS_CC

MODEL NO.
BLN-1666-22-1

MODEL SQ. FT.
990

BOX SIZE
16' x 66'

DATE PRINTED
8/15/2025

SCALE
1/8"=1'
* UNLESS OTHERWISE NOTED

PLAN NO.
BLN-1666-32-1_CYPRESS_CC

SHEET NAME
EXTERIOR ELEVATION

SHEET NO.
A4.2

File Path:Z:\DesignCenter\Architecture\CrossMod\DWG Files\CHIEF CARES\1666_CYPRESS_CC\BLN-1666-32-1_CYPRESS_CC.dwg, Last Saved By:Taylorjo, Saved Date:8/15/2025 6:05 PM

"CYPRESS_CC"

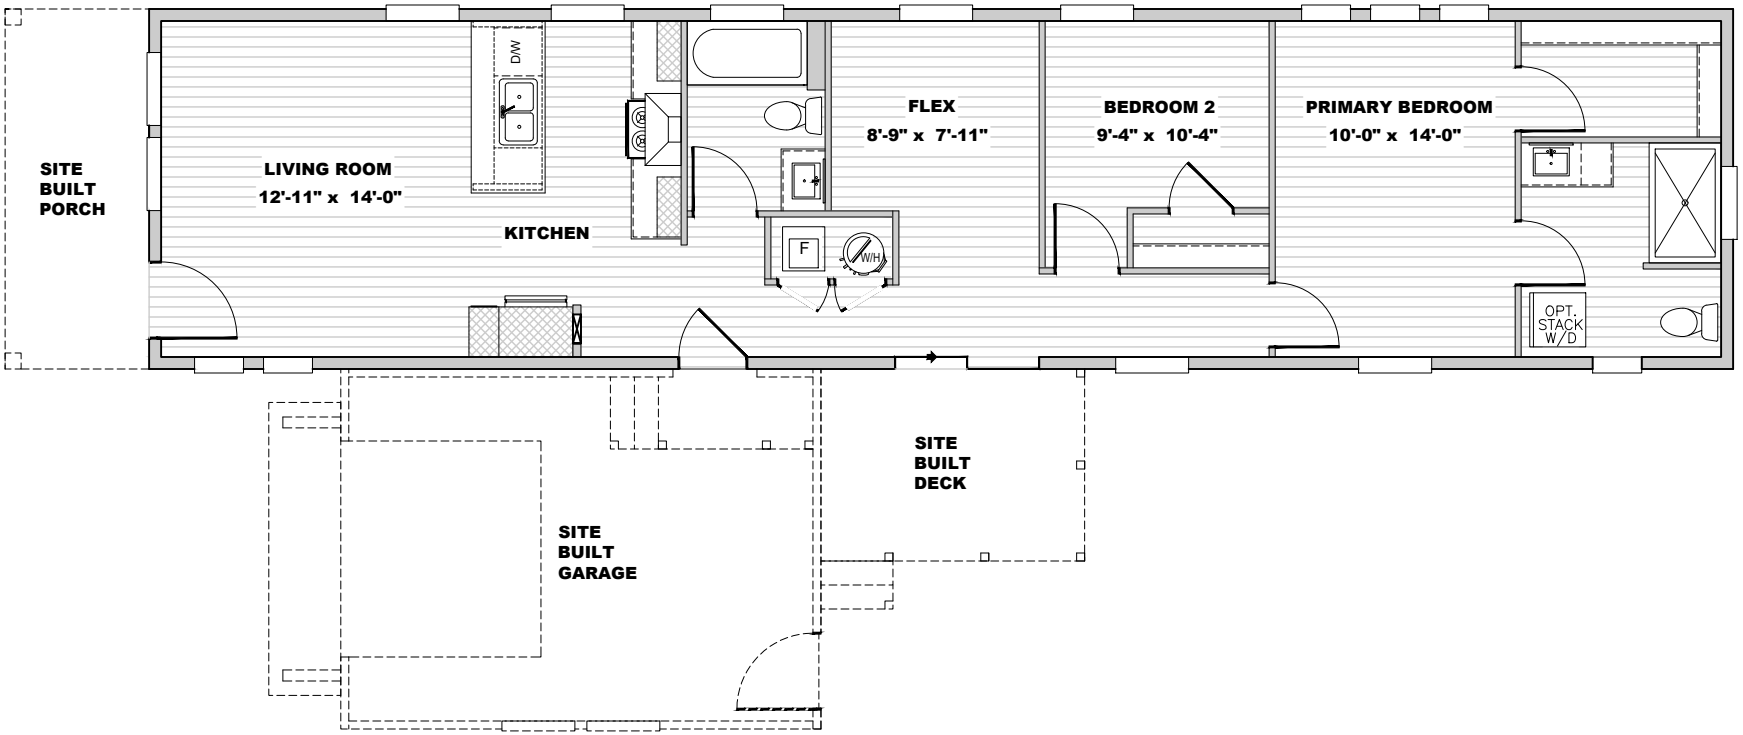

MODEL #BLN-1666-22-1 SQ.FT. 990 DRAWING # BLN-1666-32-1_CYPRESS_CC

File Path:Z:\DesignCenter\Architecture\CrossMod\DWG Files\CHIEF CARES\1666_CYPRESS_CC\BLN-1666-32-1_CYPRESS_CC.dwg, Last Saved By:Taylorjo, Saved Date:8/15/2025 6:05 PM, Date Printed:8/15/25 6:06 PM