INDEX

A0.0	COVER SHEET
A1.0	FLOOR PLAN
A1.1	LIGHTING AND FLOOR REGISTER LAYOUT
A2.0	ELEVATIONS - STANDARD
A2.1	ELEVATIONS - OPTION
A3.0	INTERIOR DETAILS - KITCHEN
A3.1	INTERIOR DETAILS - KITCHEN
A3.2	INTERIOR DETAILS - KITCHEN
A3.3	INTERIOR DETAILS - BATHS
A3.4	INTERIOR DETAILS - MISC
A3.5	INTERIOR DETAILS - MISC
A4.0	SALESLIT PRINT
	SALESLIT
	SALESLIT 2
	SALESLIT 3
	SALESLIT 4

GENERAL NOTES

1. THIS PACKAGE IS INTENDED TO RELAY DESIGN INTENT AND IS NOT FOR CONSTRUCTION.
2. PLEASE CONTACT ANDY HUTSELL AT ANDY.HUTSELL@CLAYTONHOMES.COM WITH QUESTIONS REGARDING THESE DRAWINGS.

SYMBOLS AND ABBREVIATIONS

CLG	CEILING
DR	DOOR
EF	EXHAUST FAN
FLR	FLOOR
MNT	MOUNT
OPT	OPTIONAL
RAG	RETURN AIR GRILLE
SEP	STANDARD ELECTRIC PANEL
SGD	SLIDING GLASS DOOR

Clayton Built

MODEL NAME
CrossMod_Aspen-3260_R

MODEL NO.
CrossMod-3260-32-2_Aspen_R

BOX SIZE
32' x 60'

MODEL SQ. FT.
1,620

DATE PRINTED
9/27/2023

SCALE
N.T.S.
* UNLESS OTHERWISE NOTED

PLAN NO.
CrossMod-3260-32-2_Aspen_R

SHEET NAME
COVER SHEET

SHEET NO.
A0.0.

File Path:B:\Architecture\CrossMod\DWG Files\3260_ASPEN\CrossMod-3260-32-2_Aspen_R.dwg, Last Saved By:Hutsella, Saved Date:9/27/2023 1:03 PM

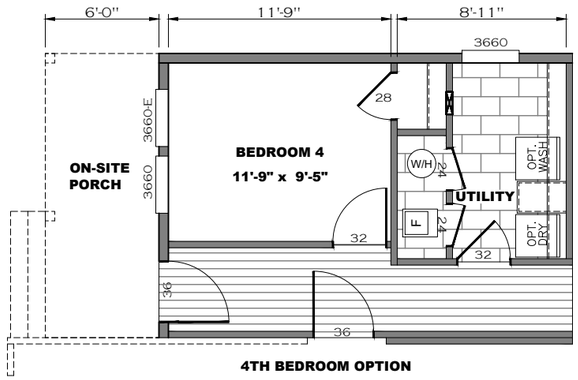

4TH BEDROOM OPTION

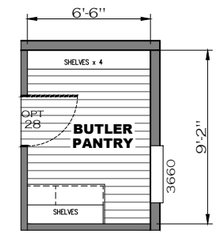

BUTLER PANTRY OPTION

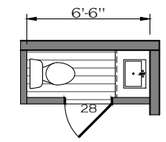

HALF BATH OPTION

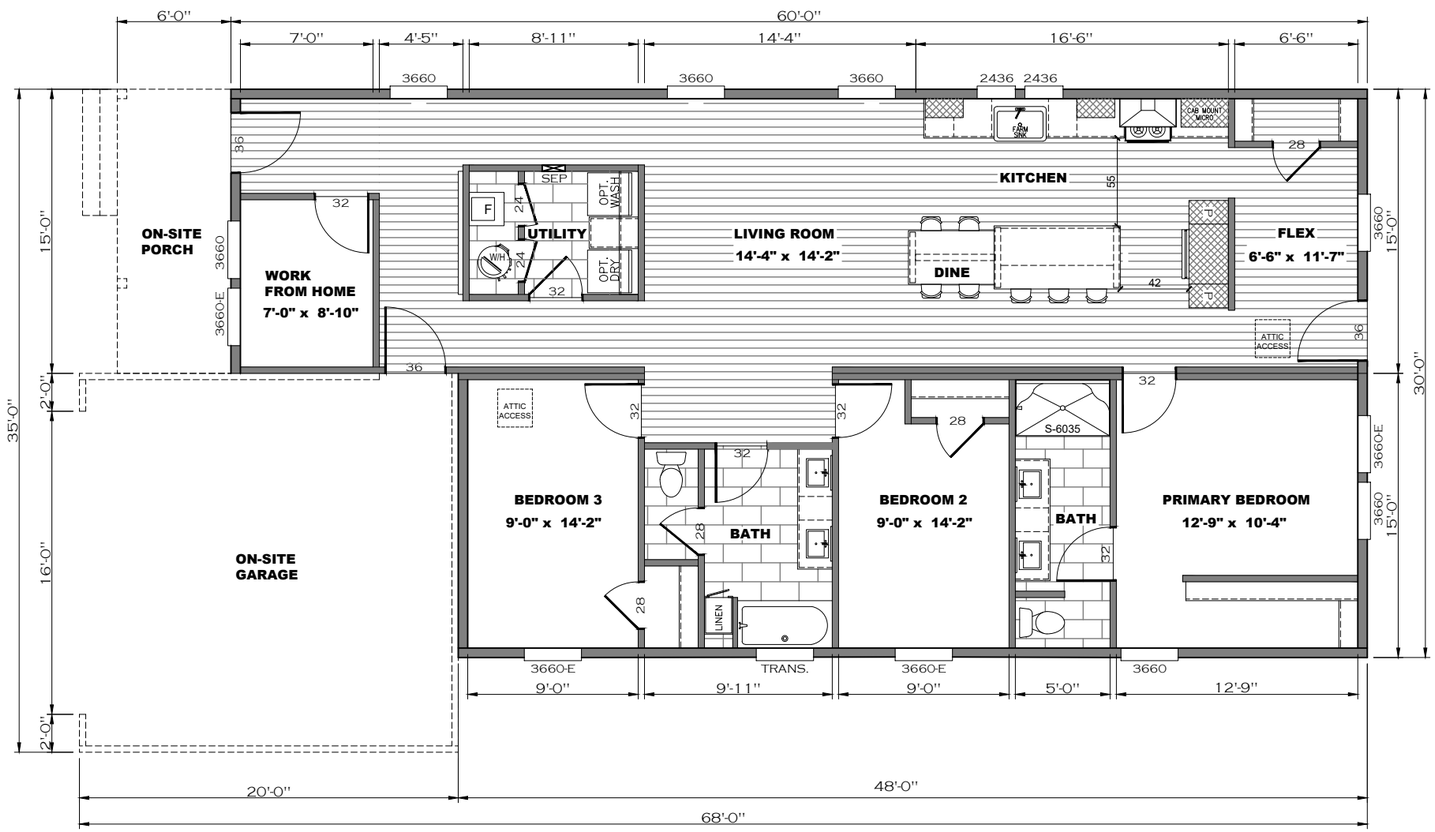

FLOOR PLAN

Clayton Built

MODEL NAME
CrossMod_Aspen-3260_R

MODEL NO.
CrossMod-3260-32-2_Aspen_R

BOX SIZE
32' x 60'

MODEL SQ. FT.
1,620

DATE PRINTED
9/27/2023

SCALE
1/8"=1'
* UNLESS OTHERWISE NOTED

PLAN NO.
CrossMod–3260-32-2_Aspen_R

SHEET NAME
FLOOR PLAN

SHEET NO.
A1.0.

File Path:B:\Architecture\CrossMod\DWG Files\3260_ASPEN\CrossMod–3260-32-2_Aspen_R.dwg, Last Saved By:Hutsella, Saved Date:9/27/2023 1:03 PM

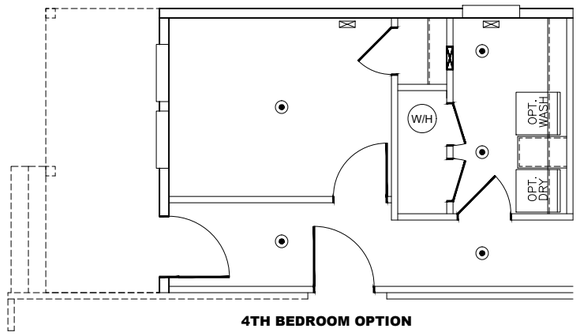

4TH BEDROOM OPTION

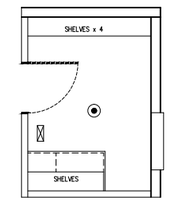

BUTLER PANTRY OPTION

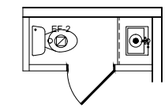

POWDER ROOM OPTION

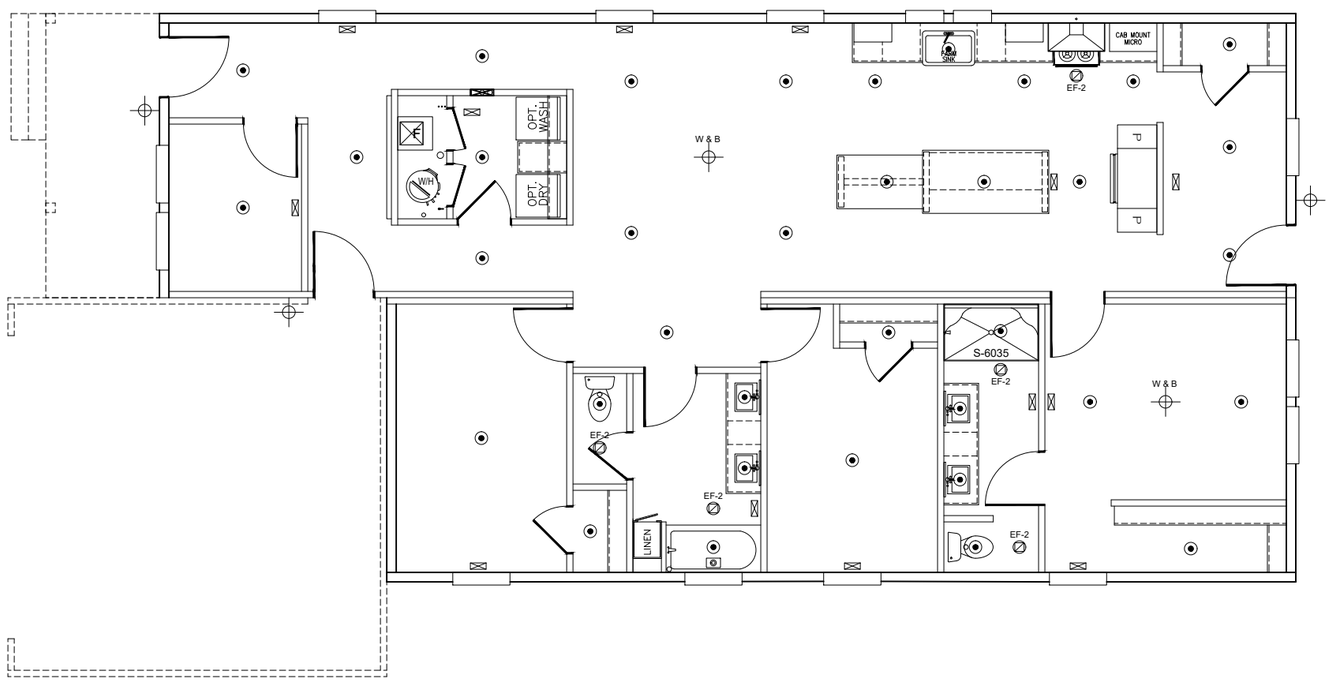

LIGHTING AND FLOOR REGISTER LAYOUT

SYMBOLS LEGEND

W & B	OPT. CEILING FAN or WIRE & BRACE
	WALL OR CEILING MNT FIXTURE
	CAN LIGHT
EF-2	BATH FAN
	HVAC REGISTER
F	HVAC FURNACE
W/H	WATER HEATER

NOTES:

1. ALL SYMBOLS MAY NOT BE APPLICABLE TO ALL PROJECTS.

Clayton Built

MODEL NAME
CrossMod_Aspen-3260_R

MODEL NO.
CrossMod-3260-32-2_Aspen_R

BOX SIZE
32' x 60'

MODEL SQ. FT.
1,620

DATE PRINTED
9/27/2023

SCALE
1/8"=1'
* UNLESS OTHERWISE NOTED

PLAN NO.
CrossMod-3260-32-2_Aspen_R

SHEET NAME
ELEC. PLAN

SHEET NO.
A1.1.

File Path:B:\Architecture\CrossMod\DWG Files\3260_ASPEN\CrossMod-3260-32-2_Aspen_R.dwg, Last Saved By:Hutsella, Saved Date:9/27/2023 1:03 PM

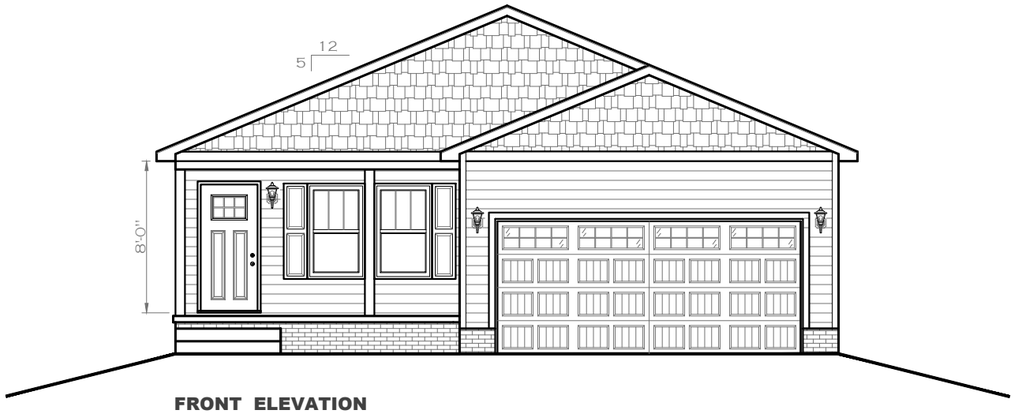

FRONT ELEVATION

REAR ELEVATION

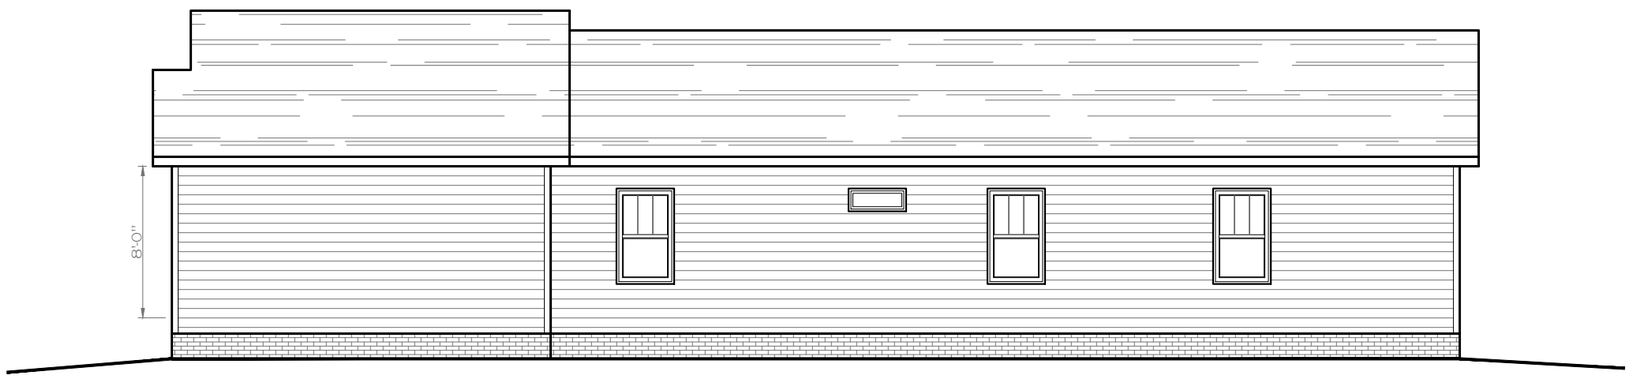

RIGHT SIDE ELEVATION

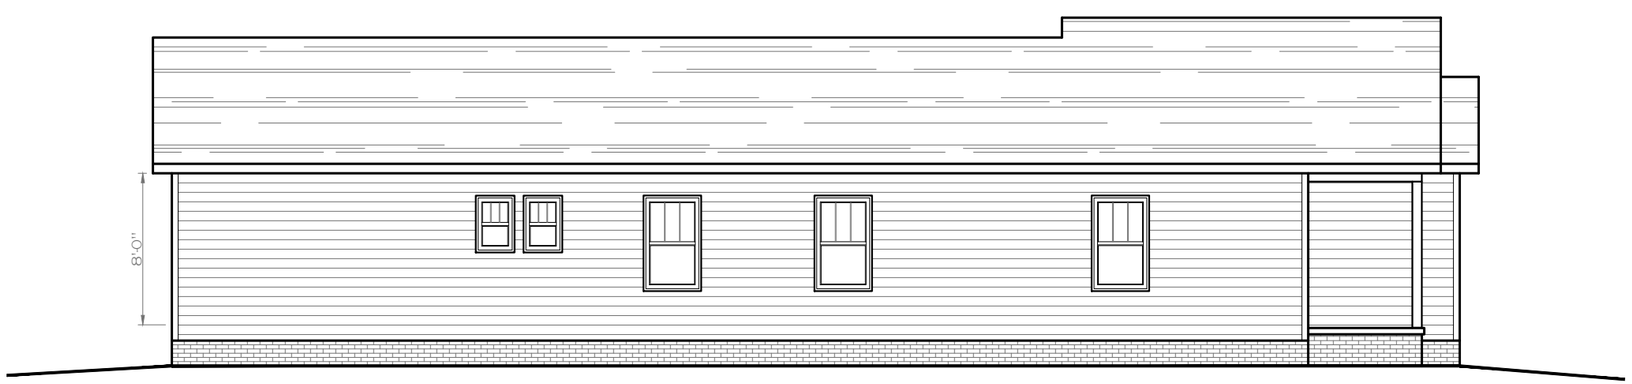

LEFT SIDE ELEVATION

Clayton Built

MODEL NAME
CrossMod_Aspen-3260_R

MODEL NO.
CrossMod-3260-32-2_Aspen_R

BOX SIZE
32' x 60'

MODEL SQ. FT.
1,620

DATE PRINTED
9/27/2023

SCALE
1/8"=1'
* UNLESS OTHERWISE NOTED

PLAN NO.
CrossMod-3260-32-2_Aspen_R

SHEET NAME
EXTERIOR ELEVATION

SHEET NO.
A2.0.

File Path:B:\Architecture\CrossMod\DWG Files\3260_ASPEN\CrossMod-3260-32-2_Aspen_R.dwg, Last Saved By:Hutsella, Saved Date:9/27/2023 1:03 PM

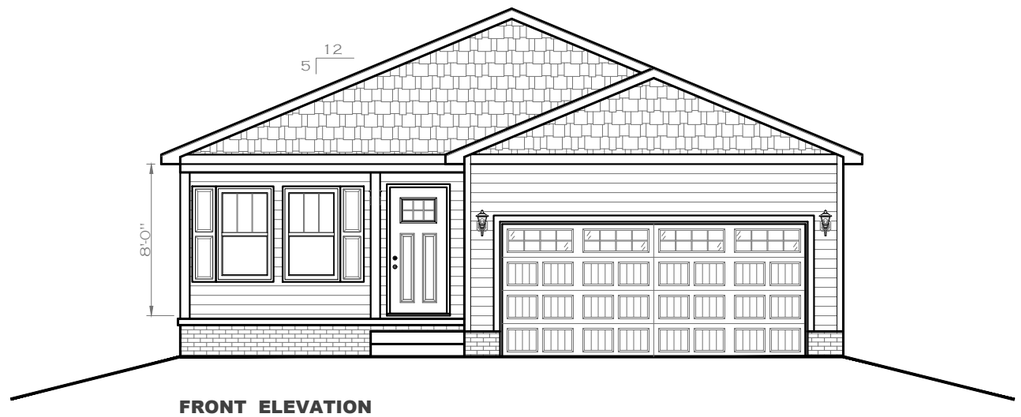

FRONT ELEVATION
(4 BEDROOM OPTION ONLY)

LEFT SIDE ELEVATION
(4 BEDROOM OPTION ONLY)

Clayton Built

MODEL NAME
CrossMod_Aspen-3260_R

MODEL NO.
CrossMod-3260-32-2_Aspen_R

BOX SIZE
32' x 60'

MODEL SQ. FT.
1,620

DATE PRINTED
9/27/2023

SCALE
1/8"=1'
* UNLESS OTHERWISE NOTED

PLAN NO.
CrossMod-3260-32-2_Aspen_R

SHEET NAME
EXTERIOR ELEVATION

SHEET NO.
A2.1.

File Path:B:\Architecture\CrossMod\DWG Files\3260_ASPEN\CrossMod-3260-32-2_Aspen_R.dwg, Last Saved By:Hutsella, Saved Date:9/27/2023 1:03 PM

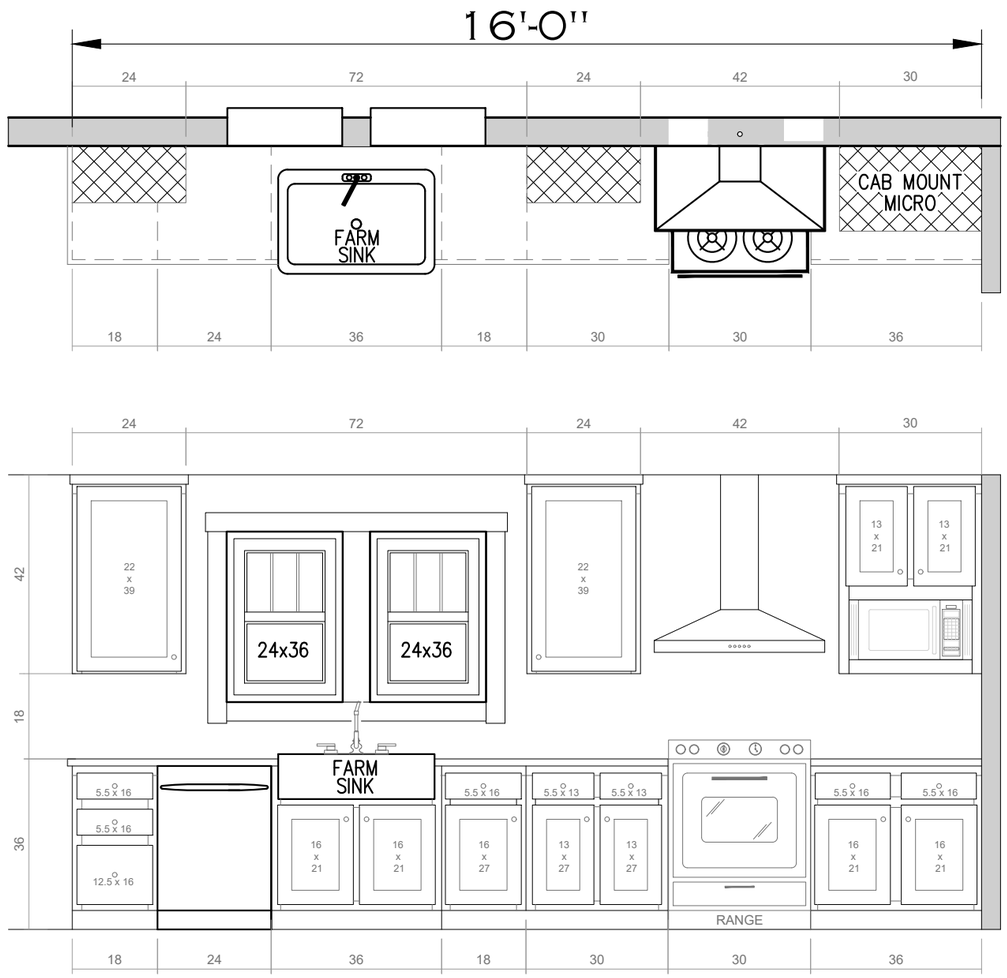

KITCHEN ELEVATION

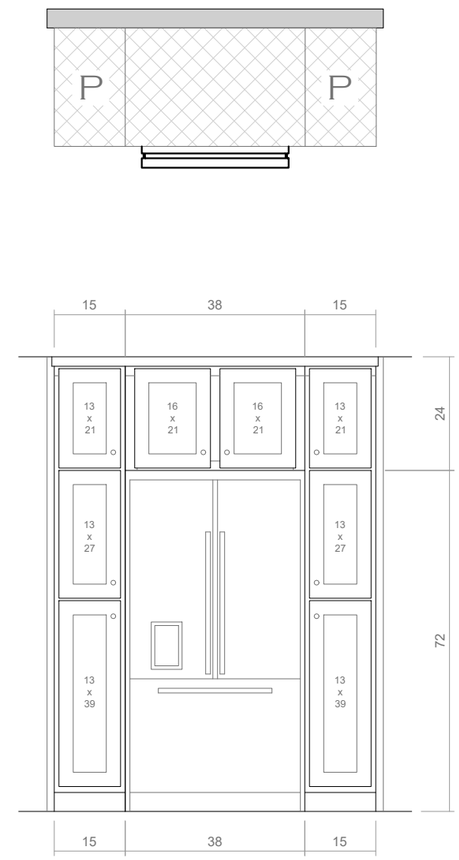

KITCHEN ELEVATION @ REFRIGERATOR

Clayton Built

MODEL NAME
CrossMod_Aspen-3260_R

MODEL NO.
CrossMod-3260-32-2_Aspen_R

BOX SIZE
32' x 60'

MODEL SQ. FT.
1,620

DATE PRINTED
9/27/2023

SCALE
3/8"=1'
* UNLESS OTHERWISE NOTED

PLAN NO.
CrossMod--3260-32-2_Aspen_R

SHEET NAME
CABINETS KITCHEN

SHEET NO.
A3.0.

File Path:B:\Architecture\CrossMod\DWG Files\3260_ASPEN\CrossMod--3260-32-2_Aspen_R.dwg, Last Saved By:Hutsella, Saved Date:9/27/2023 1:03 PM

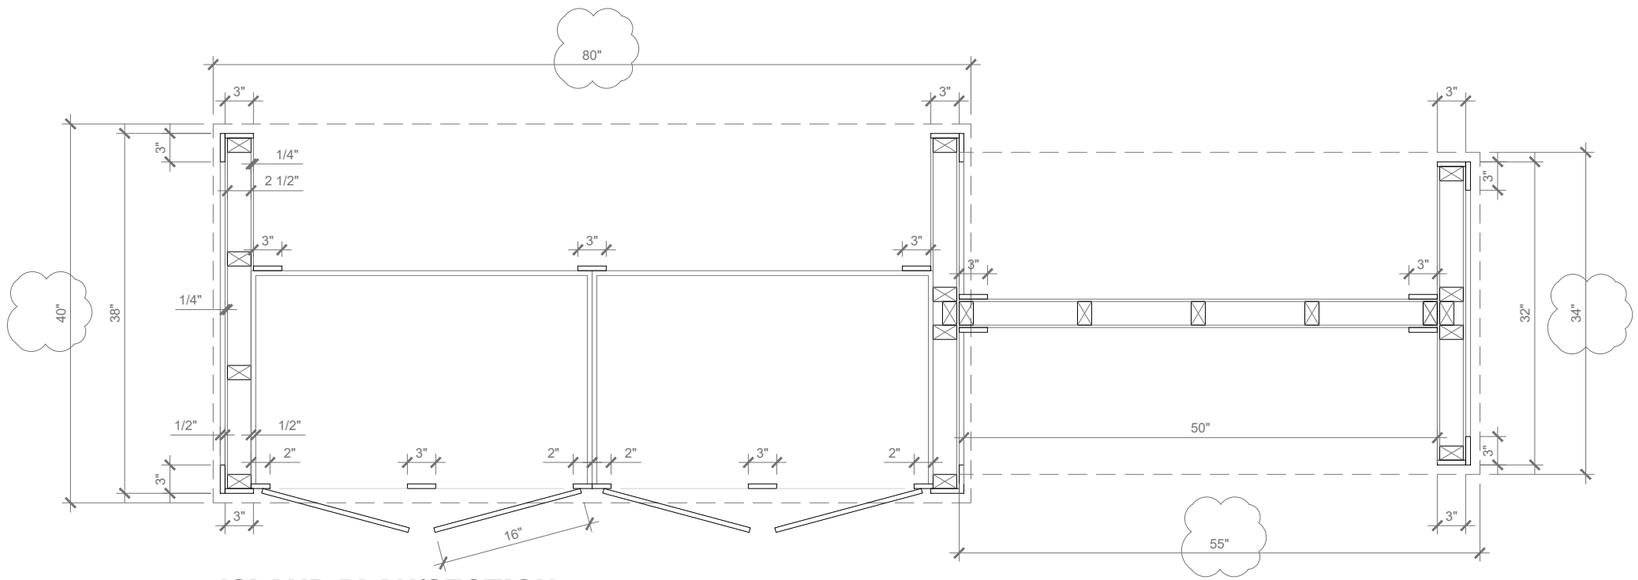

ISLAND PLAN/SECTION

$\frac{3}{4}$" = 1'-0"

Clayton Built

MODEL NAME
CrossMod_Aspen-3260_R

MODEL NO.
CrossMod-3260-32-2_Aspen_R

BOX SIZE
32' x 60'

MODEL SQ. FT.
1,620

DATE PRINTED
9/27/2023

SCALE
VARIES
* UNLESS OTHERWISE NOTED

PLAN NO.
CrossMod--3260-32-2_Aspen_R

SHEET NAME
CABINETS KITCHEN

SHEET NO.
A3.1.

File Path:B:\Architecture\CrossMod\DWG Files\3260_ASPEN\CrossMod--3260-32-2_Aspen_R.dwg, Last Saved By:Hutsella, Saved Date:9/27/2023 1:03 PM

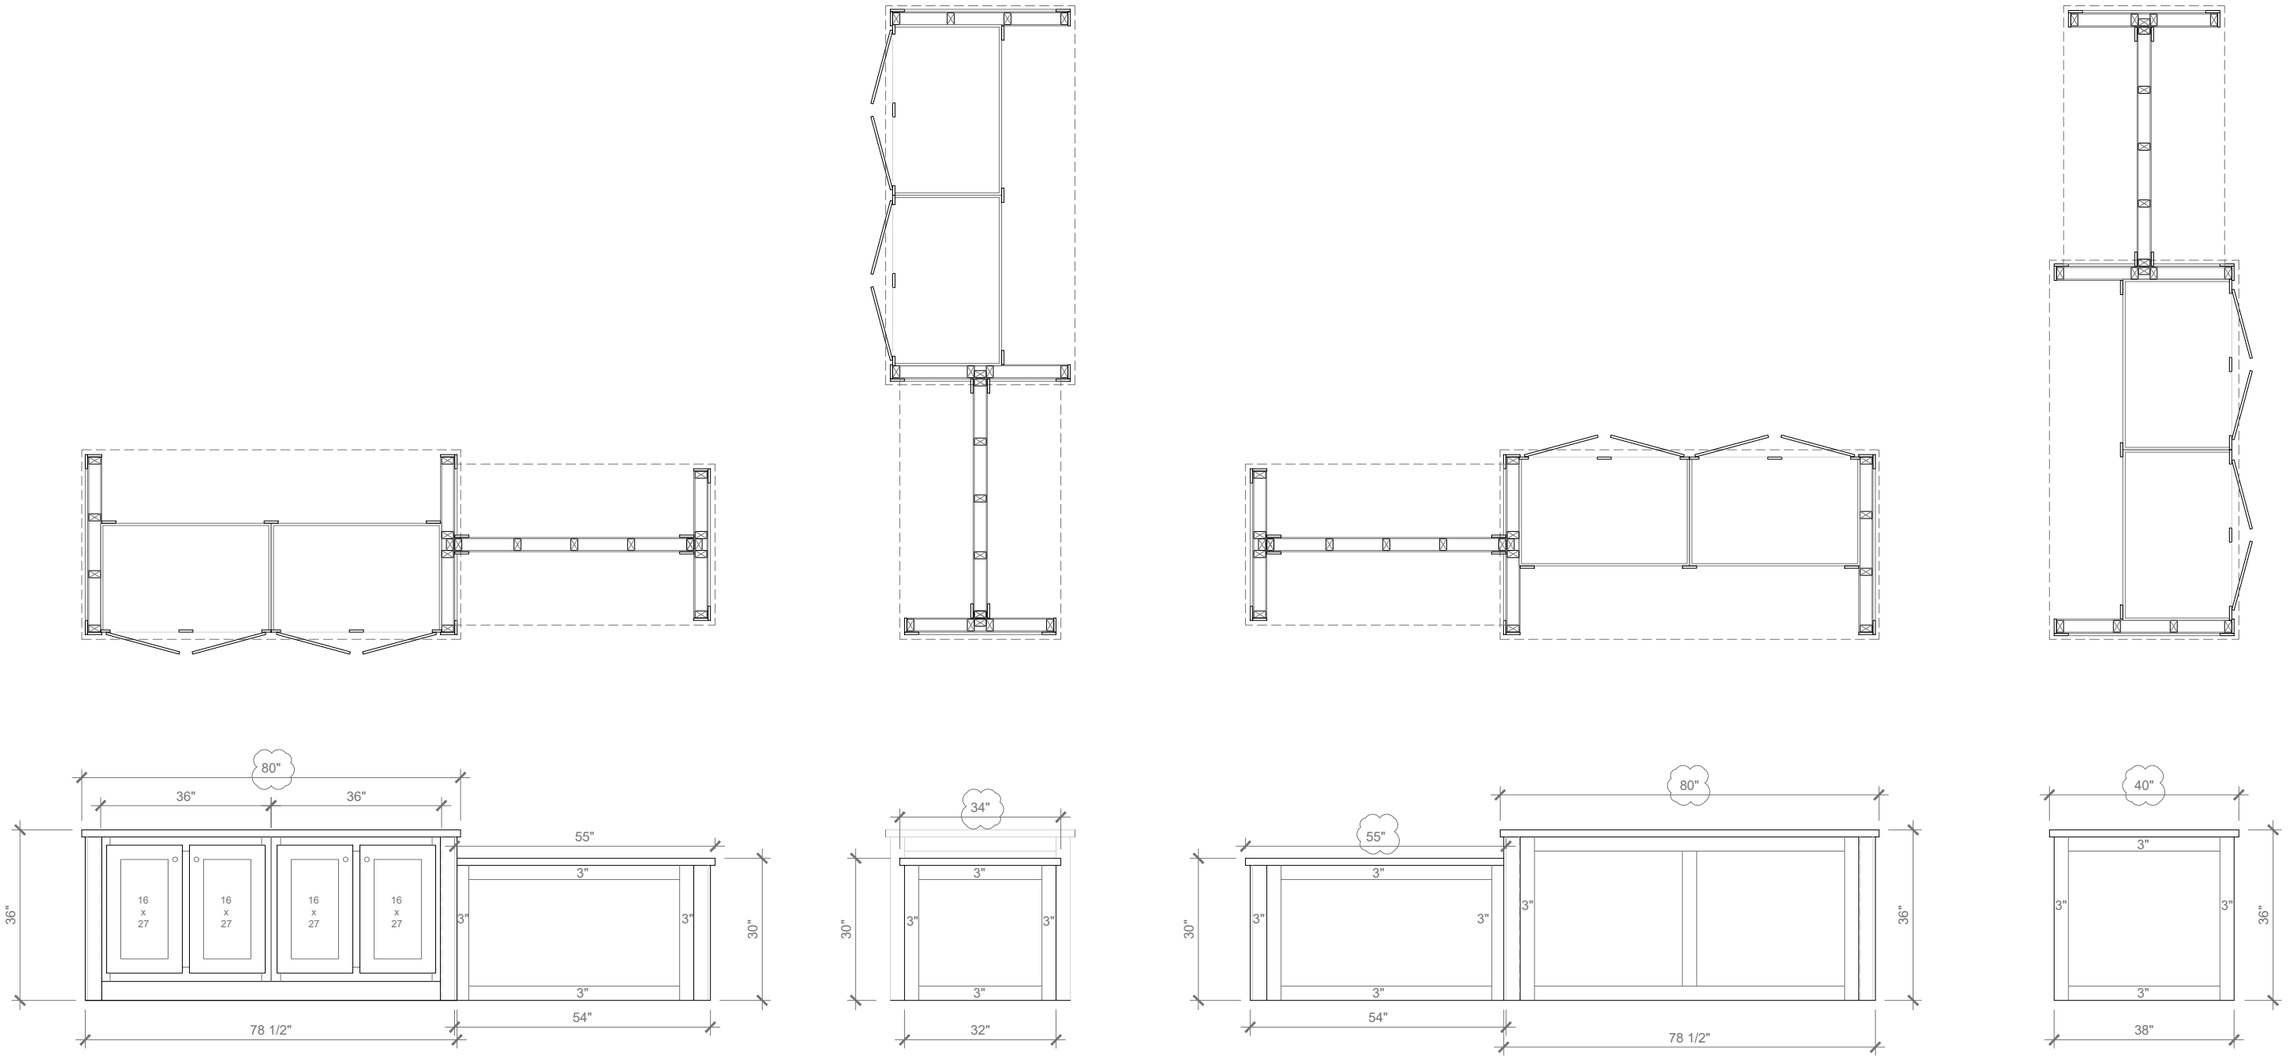

ISLAND ELEVATIONS

$\frac{3}{8}$" = 1'-0"

Clayton Built

MODEL NAME
CrossMod_Aspen-3260_R

MODEL NO.
CrossMod-3260-32-2_Aspen_R

BOX SIZE
32' x 60'

MODEL SQ. FT.
1,620

DATE PRINTED
9/27/2023

SCALE
VARIES
* UNLESS OTHERWISE NOTED

PLAN NO.
CrossMod--3260-32-2_Aspen_R

SHEET NAME
CABINETS KITCHEN

SHEET NO.
A3.2.

File Path:B:\Architecture\CrossMod\DWG Files\3260_ASPEN\CrossMod--3260-32-2_Aspen_R.dwg, Last Saved By:Hutsella, Saved Date:9/27/2023 1:03 PM

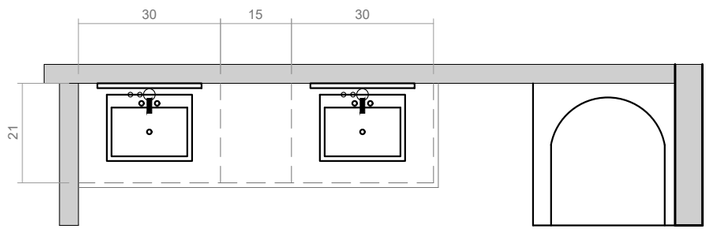

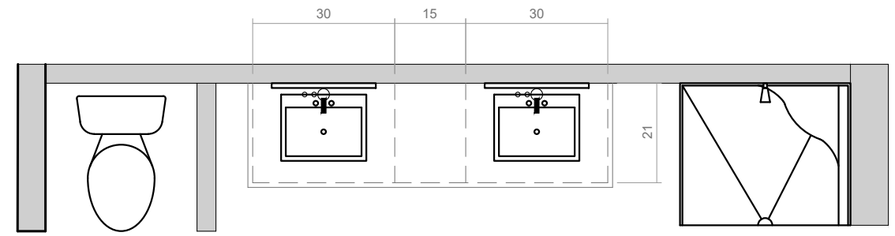

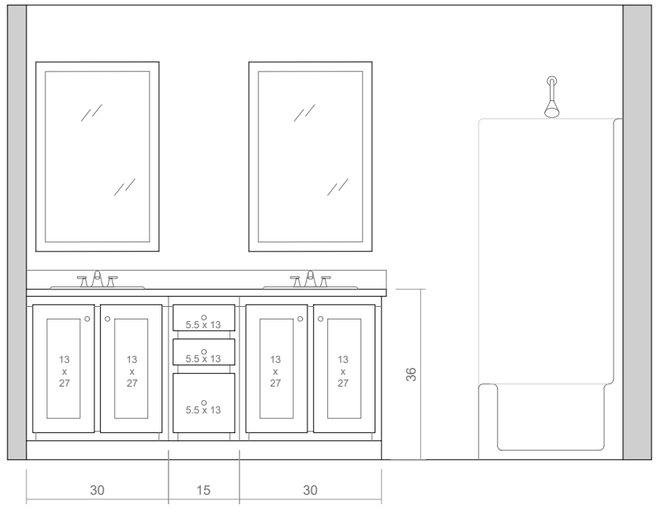

HALL BATHROOM
VANITY ELEVATION

PRIMARY BATH
VANITY ELEVATION

Clayton Built

MODEL NAME
CrossMod_Aspen-3260_R

MODEL NO.
CrossMod-3260-32-2_Aspen_R

BOX SIZE
32' x 60'

MODEL SQ. FT.
1,620

DATE PRINTED
9/27/2023

SCALE
3/8"=1'
* UNLESS OTHERWISE NOTED

PLAN NO.
CrossMod--3260-32-2_Aspen_R

SHEET NAME
CABINETS BATH

SHEET NO.
A3.3.

File Path:B:\Architecture\CrossMod\DWG Files\3260_ASPEN\CrossMod--3260-32-2_Aspen_R.dwg, Last Saved By:Hutsella, Saved Date:9/27/2023 1:03 PM

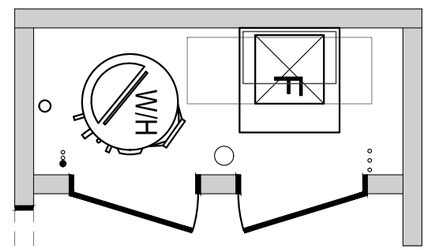

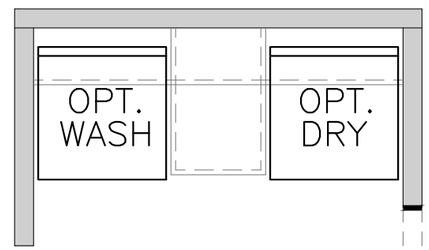

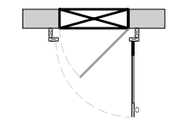

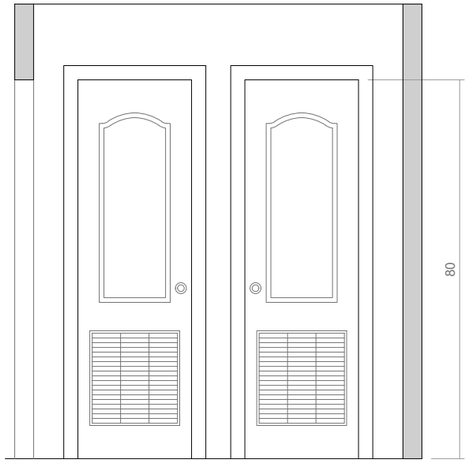

INTERIOR ELEVATION @ UTILITY CLOSET

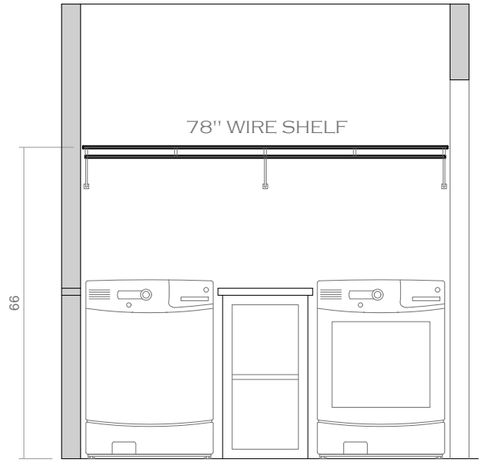

INTERIOR ELEVATION @ UTILITY CLOSET

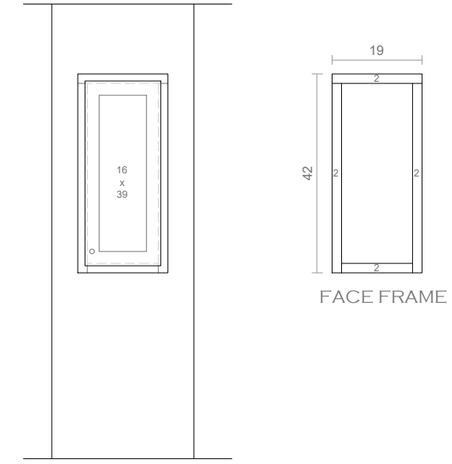

PROPOSED CABINET DOOR COVER @ PANEL BOX (NEEDS TO BE PROTOTYPED)

Clayton Built

MODEL NAME
CrossMod_Aspen-3260_R

MODEL NO.
CrossMod-3260-32-2_Aspen_R

BOX SIZE
32' x 60'

MODEL SQ. FT.
1,620

DATE PRINTED
9/27/2023

SCALE
3/8"=1'
* UNLESS OTHERWISE NOTED

PLAN NO.
CrossMod--3260-32-2_Aspen_R

SHEET NAME
MISC. DETAILS

SHEET NO.
A3.4.

File Path:B:\Architecture\CrossMod\DWG Files\3260_ASPEN\CrossMod--3260-32-2_Aspen_R.dwg, Last Saved By:Hutsella, Saved Date:9/27/2023 1:03 PM

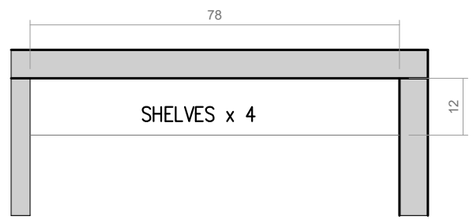

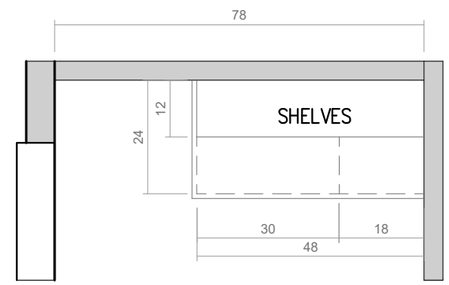

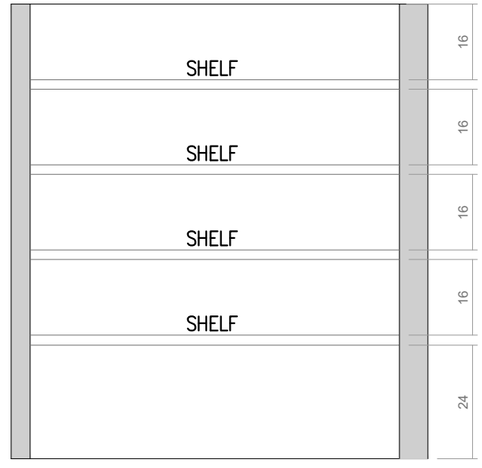

OPTIONAL BUTLER PANTRY @ SHELVING WALL

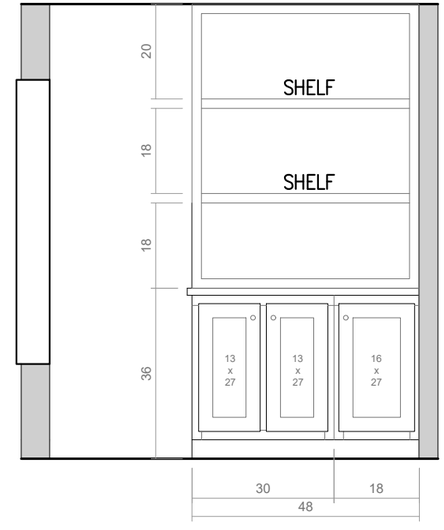

OPTIONAL BUTLER PANTRY @ CABINET WALL

Clayton Built

MODEL NAME
CrossMod_Aspen-3260_R
MODEL NO.
CrossMod-3260-32-2_Aspen_R
BOX SIZE
32' x 60'
MODEL SQ. FT.
1,620

DATE PRINTED
9/27/2023

SCALE
3/8"=1'
* UNLESS OTHERWISE NOTED

PLAN NO.
CrossMod--3260-32-2_Aspen_R

SHEET NAME
MISC. DETAILS

SHEET NO.
A3.5.

File Path:B:\Architecture\CrossMod\DWG Files\3260_ASPEN\CrossMod--3260-32-2_Aspen_R.dwg, Last Saved By:Hutsella, Saved Date:9/27/2023 1:03 PM

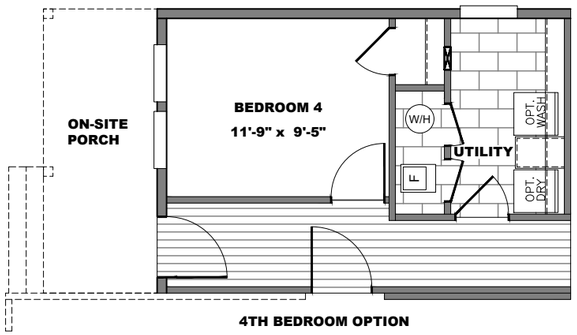

4TH BEDROOM OPTION

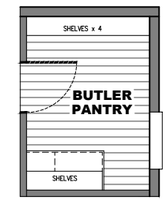

BUTLER PANTRY
OPTION

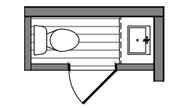

HALF BATH OPTION

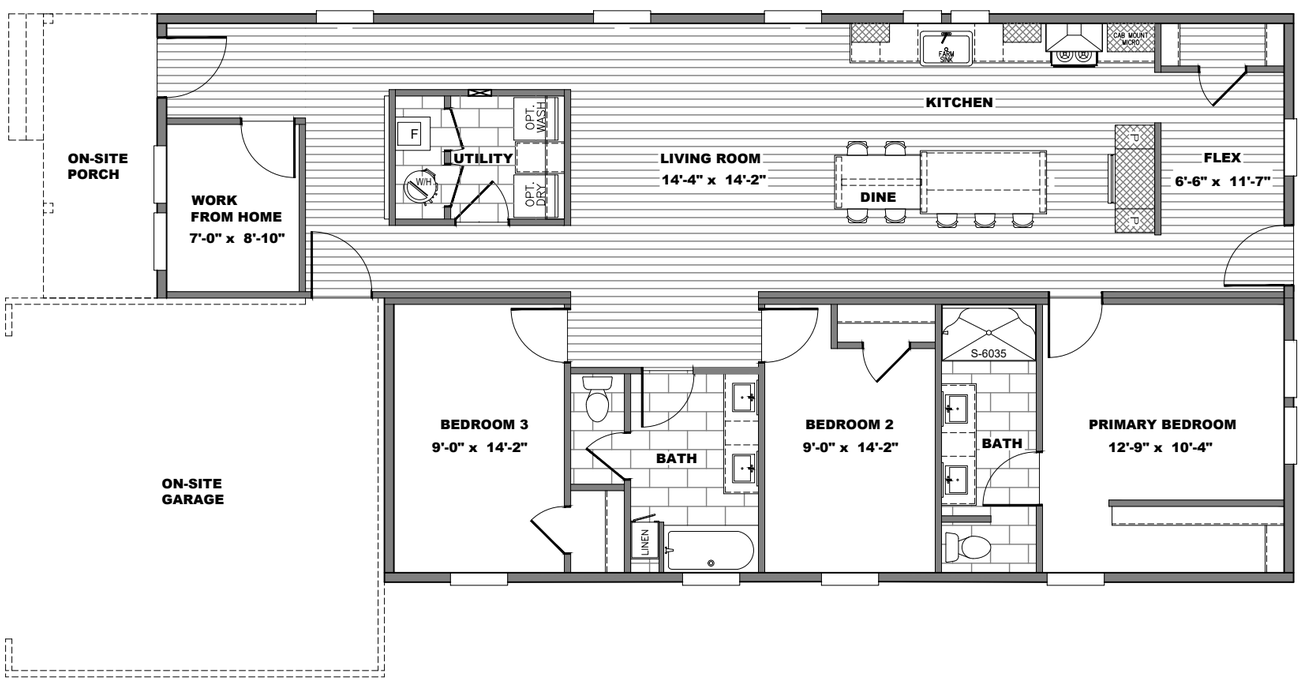

Clayton Built

MODEL NAME
CrossMod_Aspen-3260_R

MODEL NO.
CrossMod-3260-32-2_Aspen_R

BOX SIZE
32' x 60'

MODEL SQ. FT.
1,620

DATE PRINTED
9/27/2023

SCALE
1/8"=1'
* UNLESS OTHERWISE NOTED

PLAN NO.
CrossMod--3260-32-2_Aspen_R

SHEET NAME
SALESLIT

SHEET NO.
A4.0.

File Path:B:\Architecture\CrossMod\DWG Files\3260_ASPEN\CrossMod--3260-32-2_Aspen_R.dwg, Last Saved By:Hutsella, Saved Date:9/27/2023 1:03 PM

"CrossMod_Aspen-3260_R"

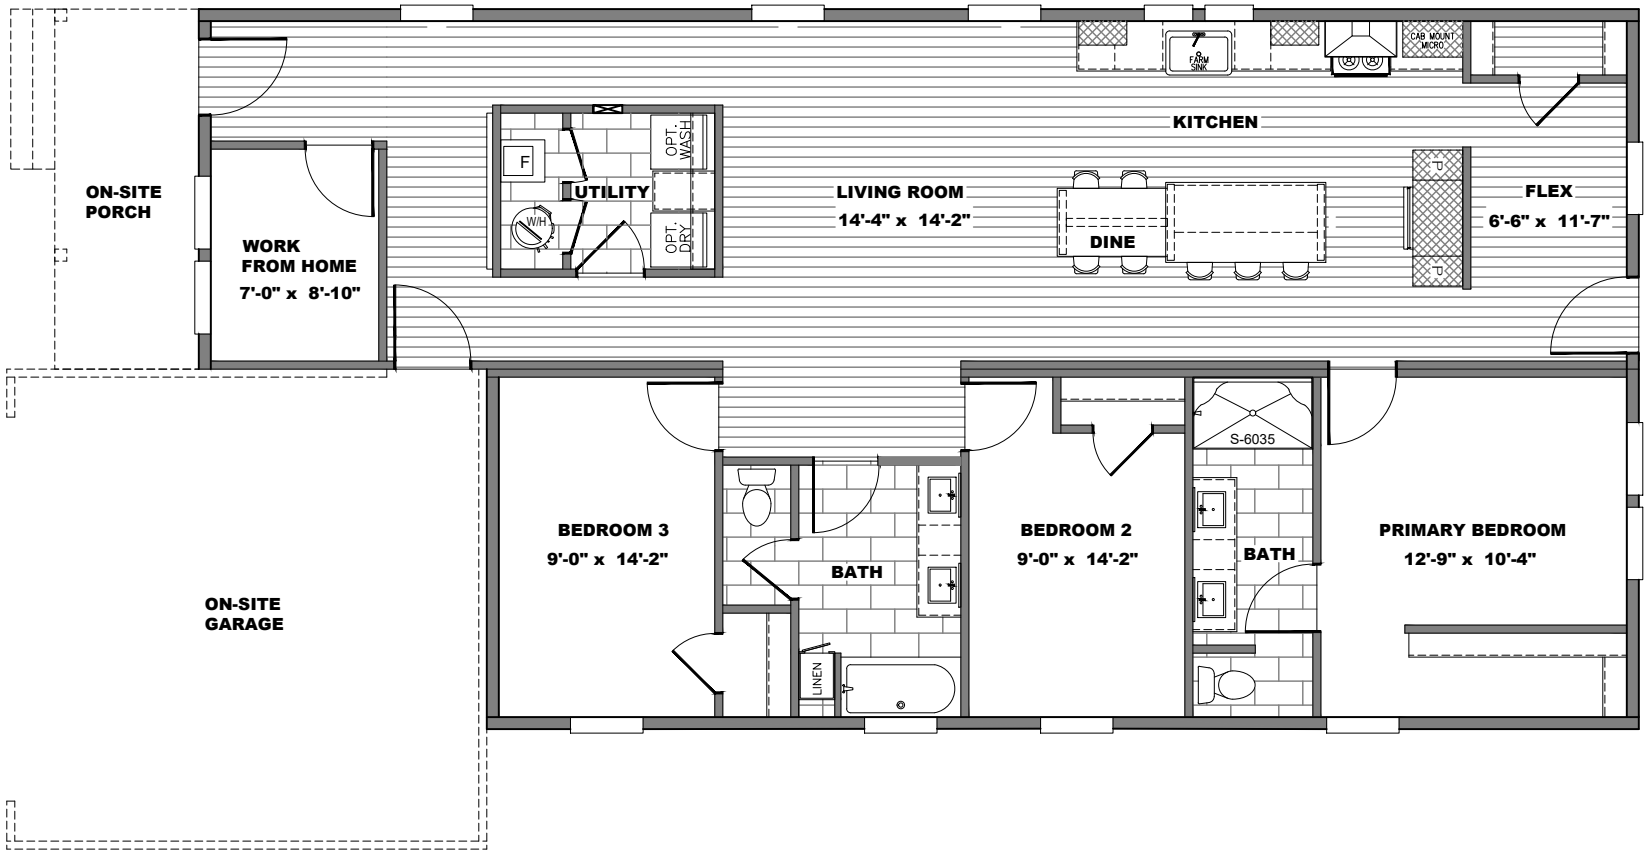

MODEL #CrossMod-3260-32-2_Aspen_R SQ.FT. 1,620 DRAWING # CROSSMOD-3260-32-2_ASPEN_R

File Path:B:\Architecture\CrossMod\DWG Files\3260_ASPEN\CrossMod--3260-32-2_Aspen_R.dwg, Last Saved By:Hutsella, Saved Date:9/27/2023 1:03 PM, Date Printed:9/27/23 1:06 PM

"CrossMod_Aspen-3260_R"

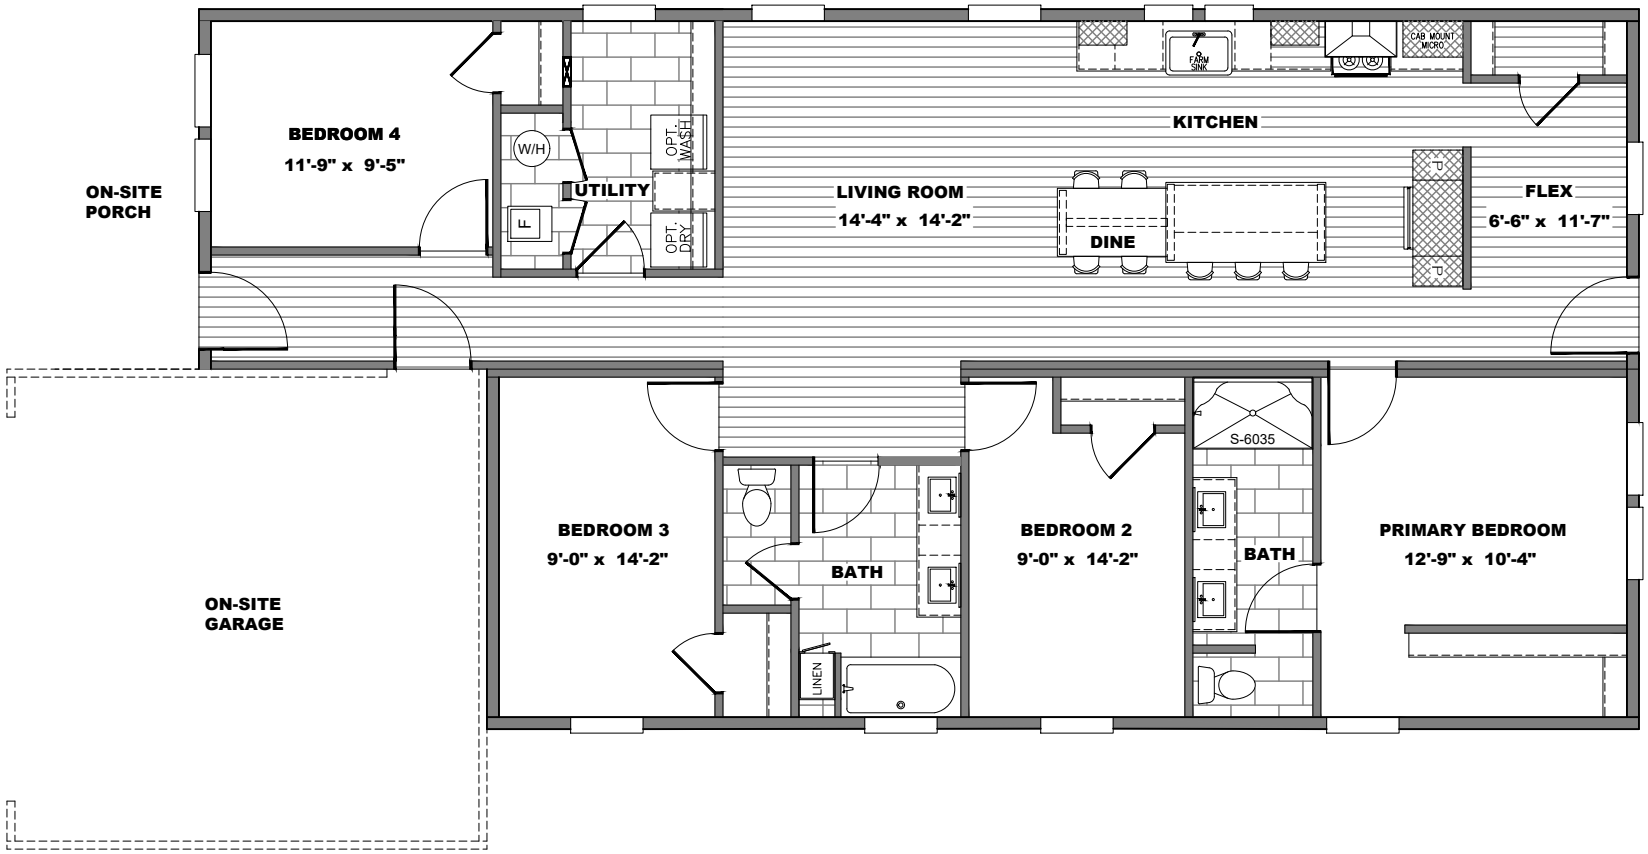

FLOOR PLAN WITH 4TH BEDROOM OPTION

MODEL #CrossMod-3260-32-2_Aspen_R SQ.FT. 1,620 DRAWING # CROSSMOD-3260-32-2_ASPEN_R

File Path:B:\Architecture\CrossMod\DWG Files\3260_ASPEN\CrossMod--3260-32-2_Aspen_R.dwg, Last Saved By:Hutsella, Saved Date:9/27/2023 1:03 PM, Date Printed:9/27/23 1:06 PM

"CrossMod_Aspen-3260_R"

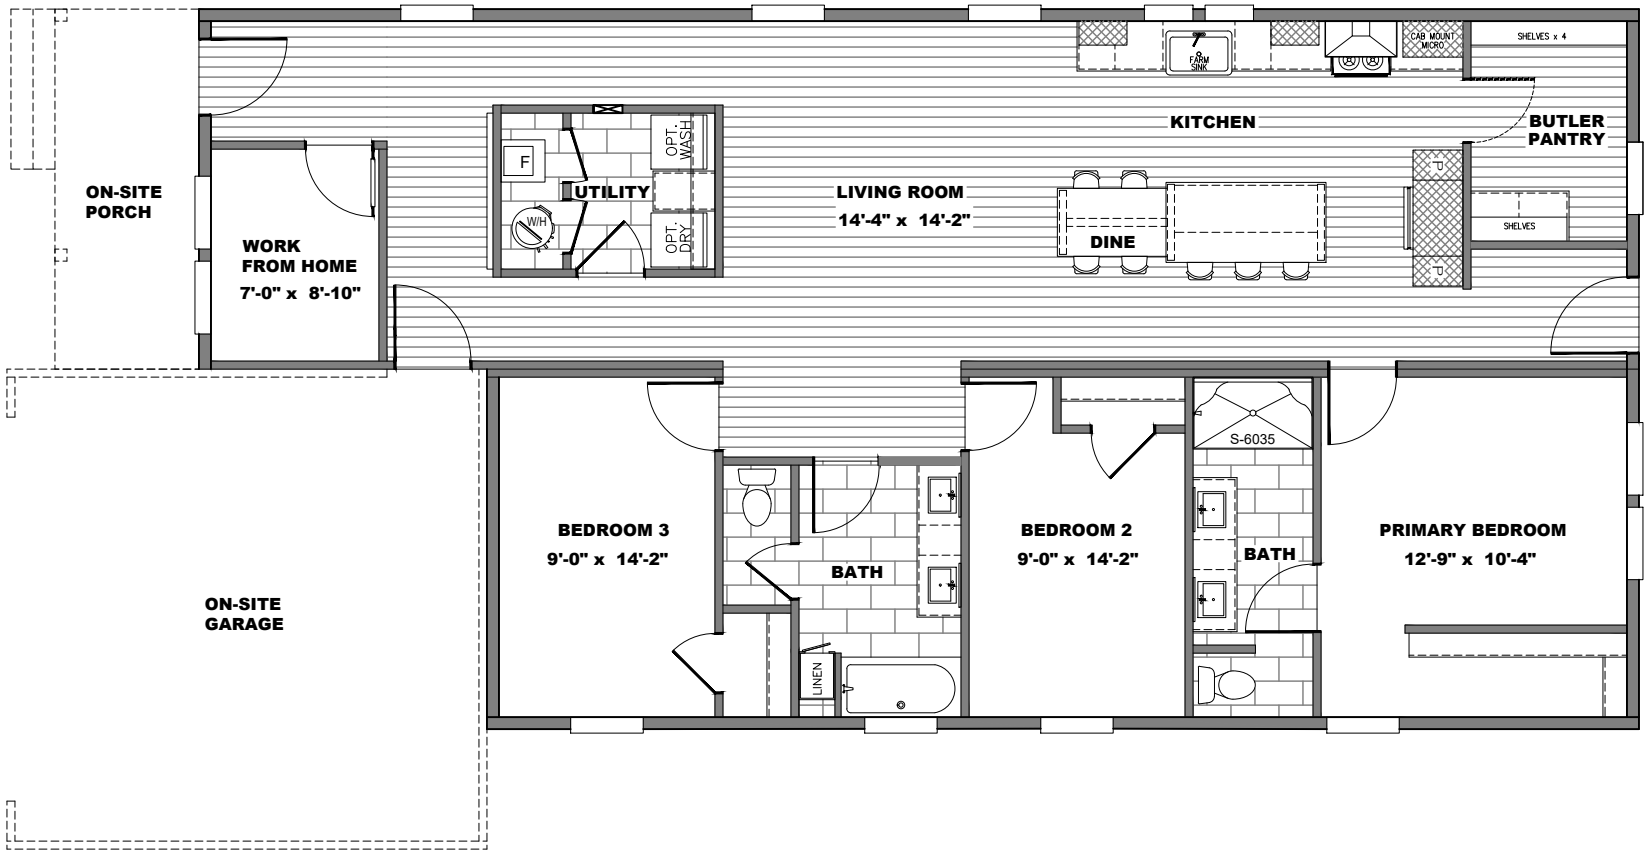

FLOOR PLAN WITH BUTLER PANTRY OPTION

MODEL #CrossMod-3260-32-2_Aspen_R SQ.FT. 1,620 DRAWING # CROSSMOD-3260-32-2_ASPEN_R

File Path:B:\Architecture\CrossMod\DWG Files\3260_ASPEN\CrossMod--3260-32-2_Aspen_R.dwg, Last Saved By:Hutsella, Saved Date:9/27/2023 1:03 PM, Date Printed:9/27/23 1:07 PM

"CrossMod_Aspen-3260_R"

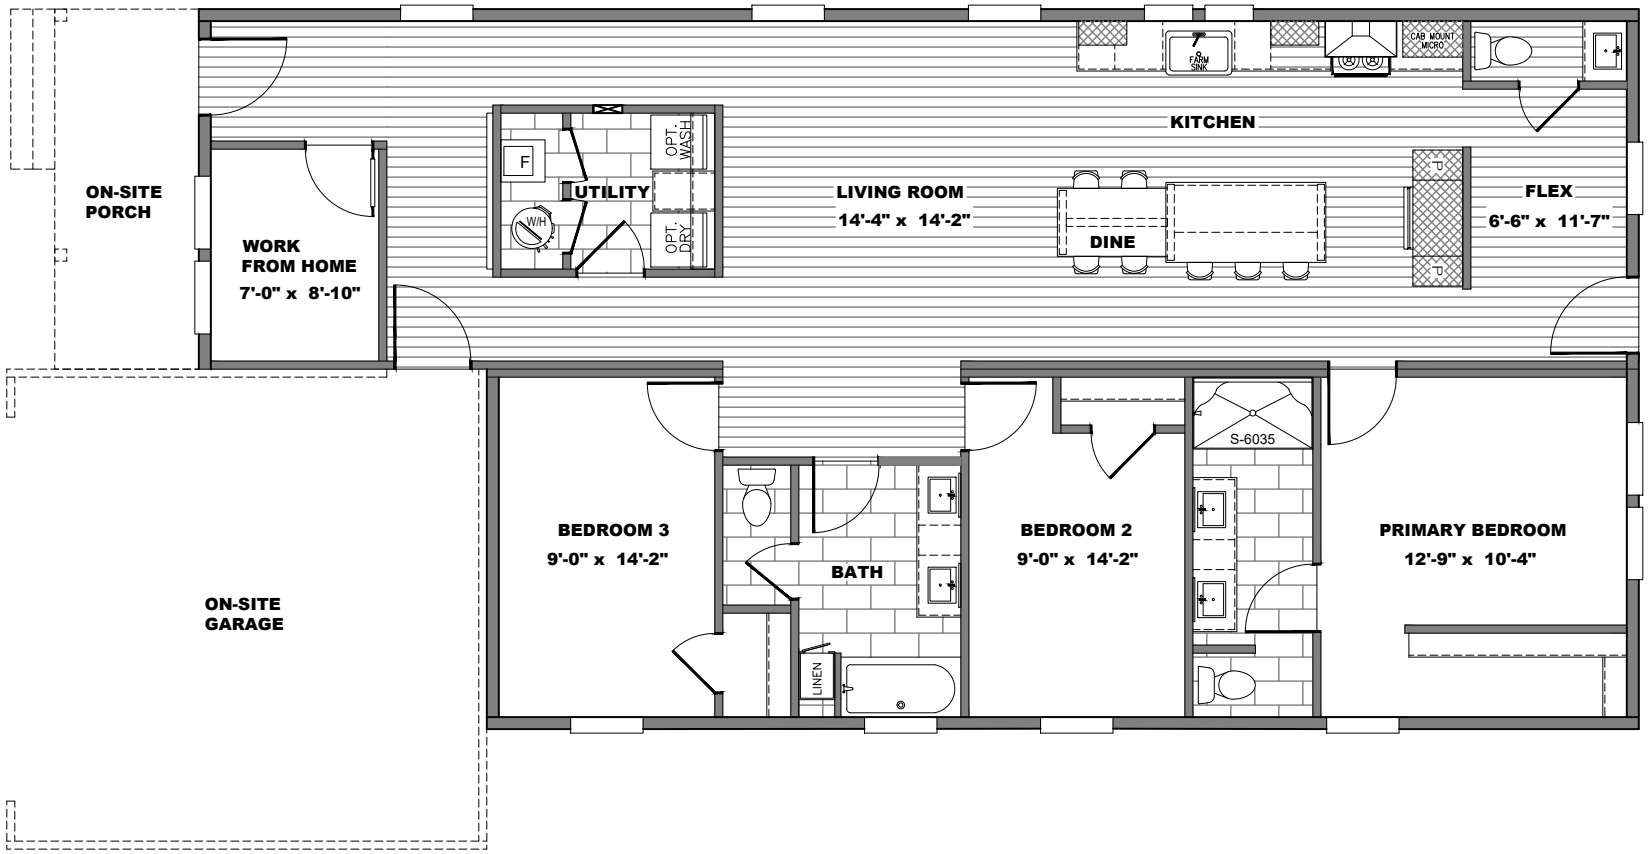

FLOOR PLAN WITH HALF BATH OPTION

MODEL #CrossMod-3260-32-2_Aspen_R SQ.FT. 1,620 DRAWING # CROSSMOD-3260-32-2_ASPEN_R

File Path:B:\Architecture\CrossMod\DWG Files\3260_ASPEN\CrossMod--3260-32-2_Aspen_R.dwg, Last Saved By:Hutsella, Saved Date:9/27/2023 1:03 PM, Date Printed:9/27/23 1:07 PM