## INDEX


| | |
|---|---|
| A0.0 | COVER SHEET |
| A1.0 | FLOOR PLAN |
| A1.1 | LIGHTING AND FLOOR REGISTER LAYOUT |
| A1.2 | FLOOR COVERING AREA CALCULATIONS |
| A2.0 | ELEVATIONS - STANDARD |
| A2.1 | ELEVATIONS - OPTION |
| A2.2 | ELEVATIONS - SITE INSTALLED CLADDING QUANTITIES |
| A3.0 | INTERIOR DETAILS - KITCHEN |
| A3.1 | INTERIOR DETAILS - KITCHEN |
| A3.2 | INTERIOR DETAILS - BATHS |
| A3.3 | INTERIOR DETAILS - MISC |
| A3.4 | INTERIOR DETAILS - MISC |
| A4.0 | SALESLIT PRINT |
| | SALESLIT |
| | SALESLIT 2 |
| | SALESLIT 3 |
| | SALESLIT 4 |


## GENERAL NOTES

1. THIS PACKAGE IS INTENDED TO RELAY DESIGN INTENT AND IS NOT FOR CONSTRUCTION.
2. PLEASE CONTACT ANDY HUTSELL AT ANDY.HUTSELL@CLAYTONHOMES.COM WITH QUESTIONS REGARDING THESE DRAWINGS.

## SYMBOLS AND ABBREVIATIONS

| | |
|---|---|
| CLG | CEILING |
| DR | DOOR |
| EF | EXHAUST FAN |
| FLR | FLOOR |
| MNT | MOUNT |
| OPT | OPTIONAL |
| RAG | RETURN AIR GRILLE |
| SEP | STANDARD ELECTRIC PANEL |
| SGD | SLIDING GLASS DOOR |

Clayton Built

MODEL NAME
CrossMod_Hawthorne_R

MODEL NO.
CrossMod-3264-32-1_Hawthorne_R

BOX SIZE
32' x 64'

MODEL SQ. FT.
1,620

DATE PRINTED
11/21/2023

SCALE
N.T.S.
* UNLESS OTHERWISE NOTED

PLAN NO.
CrossMod--3264-32-1_Hawthorne_R

SHEET NAME
COVER SHEET

SHEET NO.
A0.0.

File Path:B:\Architecture\CrossMod\DWG Files\3264_HAWTHORNE\CrossMod--3264-32-1_Hawthorne_R.dwg, Last Saved By:Hutsella, Saved Date:11/21/2023 12:44 PM

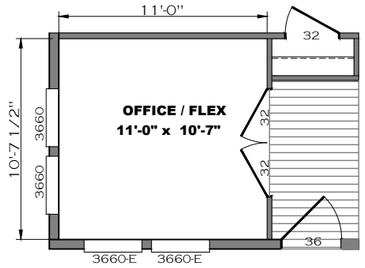


**OFFICE / FLEX SPACE OPTION**

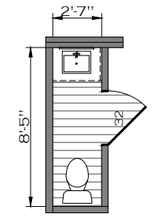


**HALF BATH OPTION**

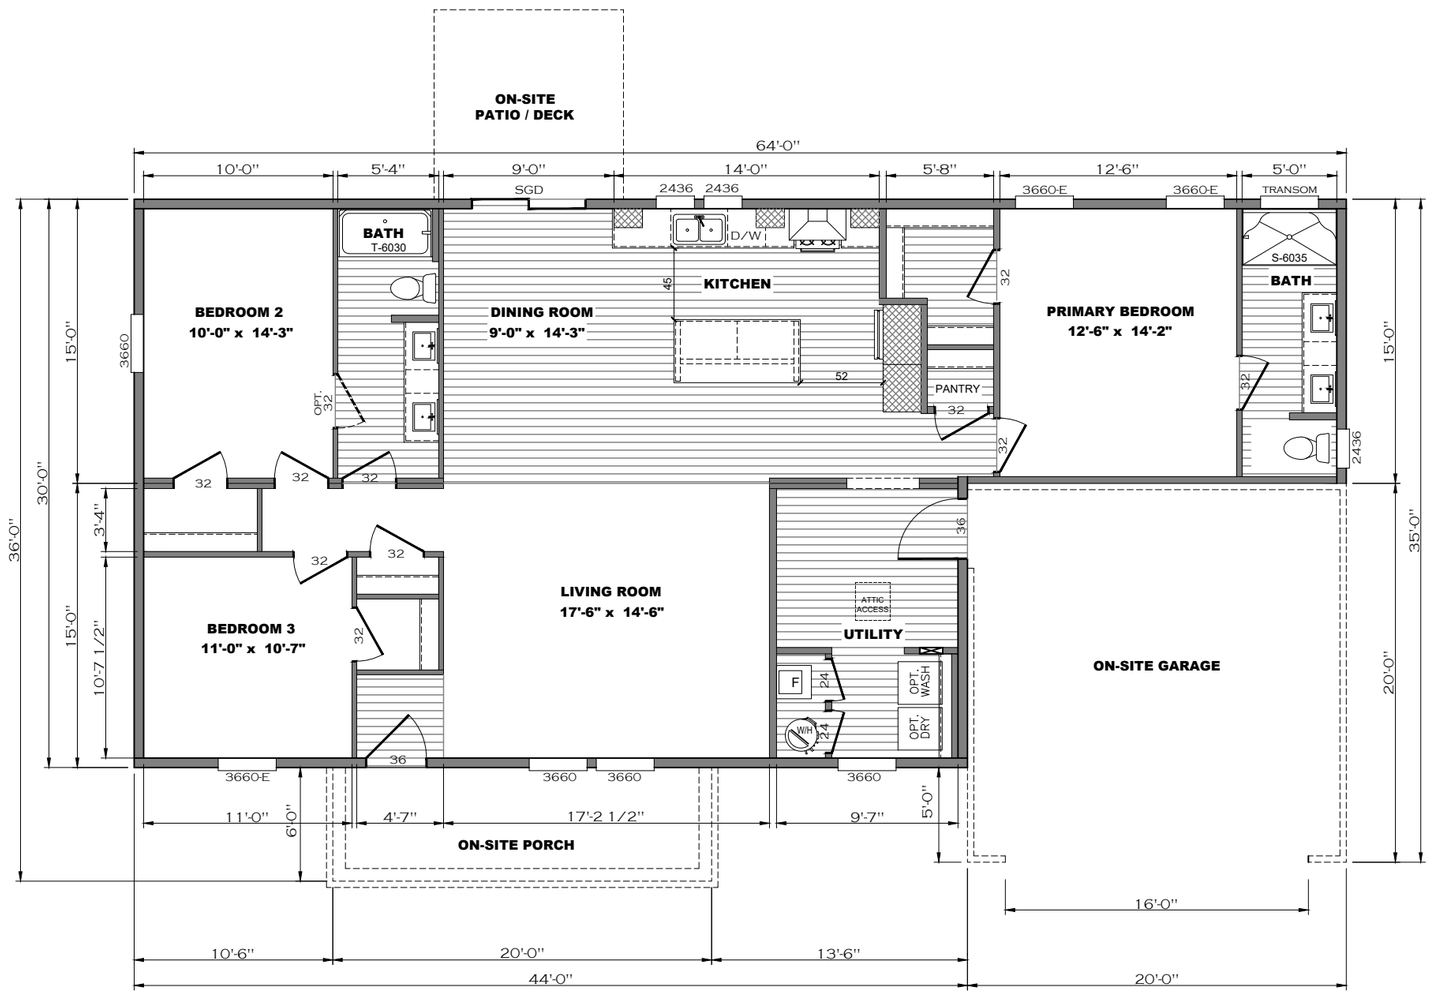


**FLOOR PLAN**

Clayton Built

MODEL NAME
CrossMod_Hawthorne_R

MODEL NO.
CrossMod-3264-32-1_Hawthorne_R

BOX SIZE
32' x 64'

MODEL SQ. FT.
1,620

DATE PRINTED
11/21/2023

SCALE
1/8"=1'
* UNLESS OTHERWISE NOTED

PLAN NO.
CrossMod--3264-32-1_Hawthorne_R

SHEET NAME
FLOOR PLAN

SHEET NO.
A1.0.

File Path:B:\Architecture\CrossMod\DWG Files\3264_HAWTHORNE\CrossMod--3264-32-1_Hawthorne_R.dwg, Last Saved By:Hutsella, Saved Date:11/21/2023 12:44 PM

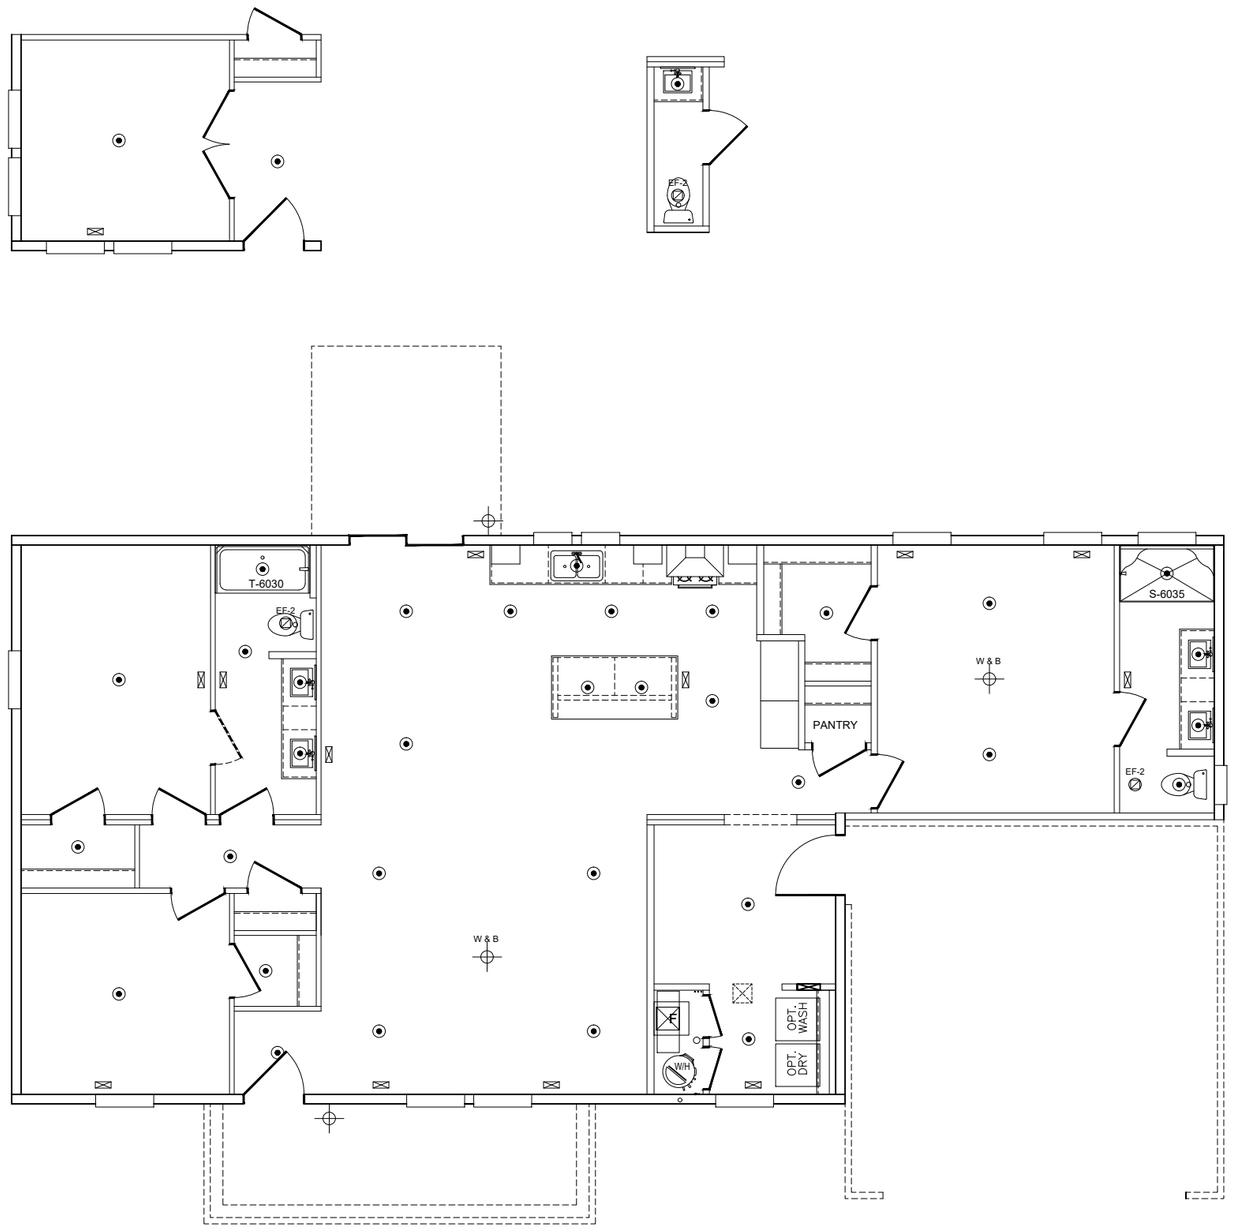


## LIGHTING AND FLOOR REGISTER LAYOUT

**SYMBOLS LEGEND**

| | |
|---|---|
| W & B | OPT. CEILING FAN or WIRE & BRACE |
| | WALL OR CEILING MNT FIXTURE |
| | CAN LIGHT |
| EF-2 | BATH FAN |
| | HVAC REGISTER |
| F | HVAC FURNACE |
| W/H | WATER HEATER |

NOTES:
1. ALL SYMBOLS MAY NOT BE APPLICABLE TO ALL PROJECTS.

Clayton Built

MODEL NAME
CrossMod_Hawthorne_R

MODEL NO.
CrossMod-3264-32-1_Hawthorne_R

BOX SIZE
32' x 64'

MODEL SQ. FT.
1,620

DATE PRINTED
11/21/2023

SCALE
1/8"=1'
* UNLESS OTHERWISE NOTED

PLAN NO.
CrossMod--3264-32-1_Hawthorne_R

SHEET NAME
ELEC. PLAN

SHEET NO.
A1.1.

File Path:B:\Architecture\CrossMod\DWG Files\3264_HAWTHORNE\CrossMod--3264-32-1_Hawthorne_R.dwg, Last Saved By:Hutsella, Saved Date:11/21/2023 12:44 PM

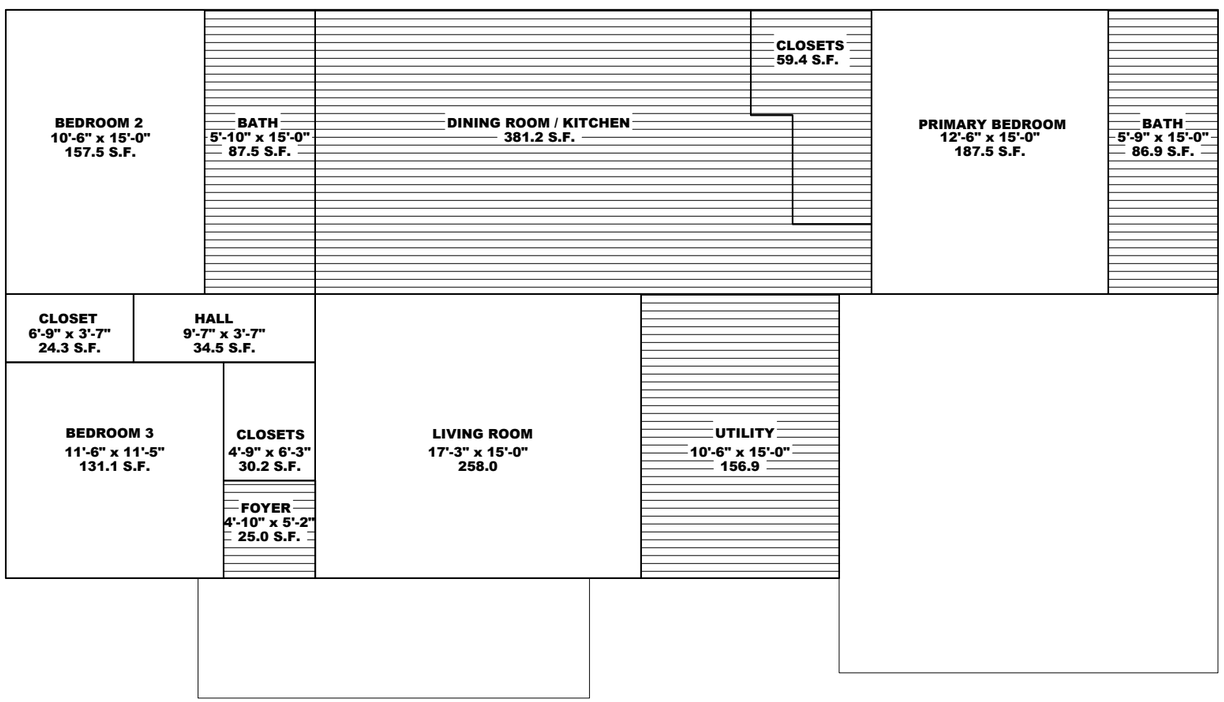


## FLOOR COVERING LEGEND

| FLOORING TYPE | | | |
|---|---|---|---|
| | BEDROOM 2 | 157.5 S.F. | |
| | HALL BATH | 87.5 S.F. | |
| | DINE / KIT | 381.2 S.F. | |
| | CLOSETS | 59.4 S.F. | |
| | PRIMARY BR | 187.5 S.F. | |
| | PRIMARY BA | 86.9 S.F. | |
| | BEDROOM 3 | 131.1 S.F. | |
| | BR 2 CLOSET | 24.3 S.F. | |
| | HALL | 34.5 S.F. | |
| | CLOSETS | 30.2 S.F. | |
| | FOYER | 25.0 S.F. | |
| | LIVING ROOM | 258.0 S.F. | |
| | UTILITY | 156.9 S.F. | |
| | | | 1620.0 S.F. |

| | |
|---|---|
| **OVERALL TOTAL HEATED SQUARE FOOTAGE** | 1620.0 S.F. |

**FLOOR COVERING SQUARE FT. CALCULATIONS**

Clayton Built

MODEL NAME
CrossMod_Hawthorne_R

MODEL NO.
CrossMod-3264-32-1_Hawthorne_R

BOX SIZE
32' x 64'

MODEL SQ. FT.
1,620

DATE PRINTED
11/21/2023

SCALE
1/8"=1'
* UNLESS OTHERWISE NOTED

PLAN NO.
CrossMod-3264-32-1_Hawthorne_R

SHEET NAME
FLOOR COVERING

SHEET NO.
A1.2.

File Path:B:\Architecture\CrossMod\DWG Files\3264_HAWTHORNE\CrossMod-3264-32-1_Hawthorne_R.dwg, Last Saved By:Hutsella, Saved Date:11/21/2023 12:44 PM

**FRONT ELEVATION**

**LEFT SIDE ELEVATION**

**RIGHT SIDE ELEVATION**

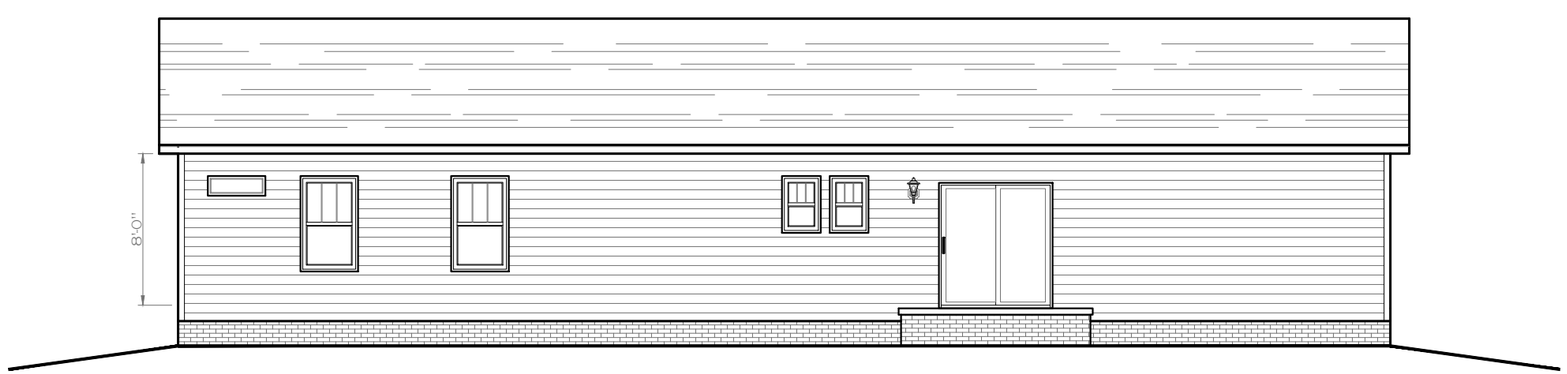


**REAR ELEVATION**

Clayton Built

MODEL NAME
CrossMod_Hawthorne_R

MODEL NO.
CrossMod-3264-32-1_Hawthorne_R

BOX SIZE
32' x 64'

MODEL SQ. FT.
1,620

DATE PRINTED
11/21/2023

SCALE
1/8"=1'
* UNLESS OTHERWISE NOTED

PLAN NO.
CrossMod--3264-32-1_Hawthorne_R

SHEET NAME
EXTERIOR ELEVATION

SHEET NO.
A2.0.

File Path:B:\Architecture\CrossMod\DWG Files\3264_HAWTHORNE\CrossMod--3264-32-1_Hawthorne_R.dwg, Last Saved By:Hutsella, Saved Date:11/21/2023 12:44 PM

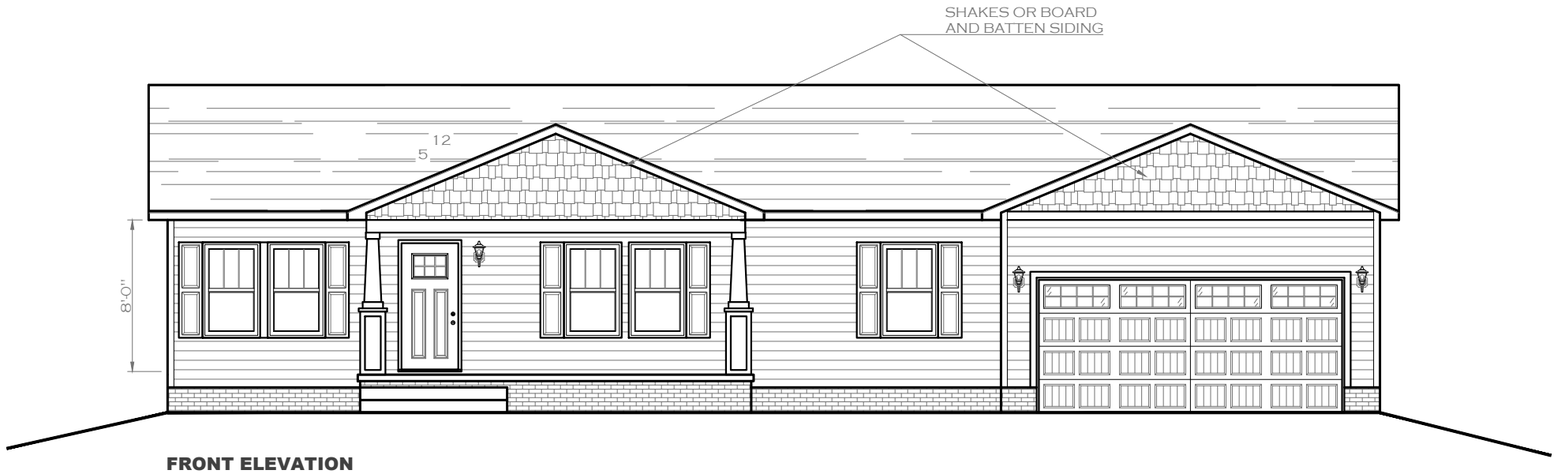


**FRONT ELEVATION**
**OFFICE / FLEX OPTION**

**LEFT SIDE ELEVATION**
**OFFICE / FLEX OPTION**

Clayton Built

MODEL NAME
CrossMod_Hawthorne_R

MODEL NO.
CrossMod-3264-32-1_Hawthorne_R

BOX SIZE
32' x 64'

MODEL SQ. FT.
1,620

DATE PRINTED
11/21/2023

SCALE
1/8"=1'
* UNLESS OTHERWISE NOTED

PLAN NO.
CrossMod--3264-32-1_Hawthorne_R

SHEET NAME
EXTERIOR ELEV. OPT.

SHEET NO.
A2.1.

File Path:B:\Architecture\CrossMod\DWG Files\3264_HAWTHORNE\CrossMod--3264-32-1_Hawthorne_R.dwg, Last Saved By:Hutsella, Saved Date:11/21/2023 12:44 PM

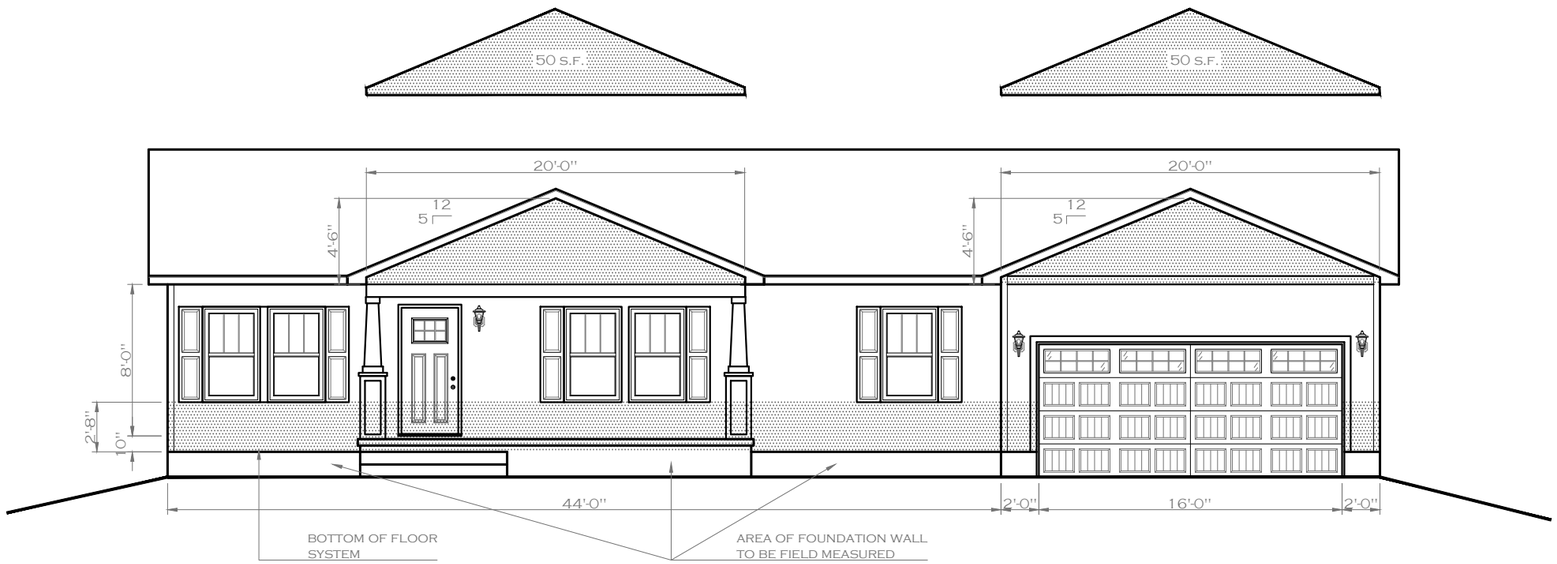


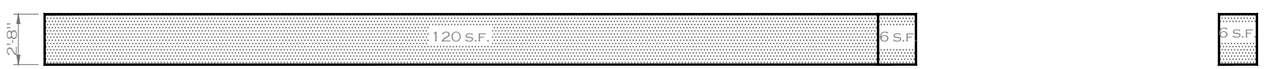


**HAWTHORNE FRONT ELEVATION WITH SITE INSTALLED CLADDING QUANTITY CALCS.**

NOTE: QUANTITIES SHOWN ON THIS DIAGRAM ARE ESTIMATES ONLY. THEY DO NOT ACCOUNT FOR WASTE.

Clayton Built

MODEL NAME
CrossMod_Hawthorne_R

MODEL NO.
CrossMod-3264-32-1_Hawthorne_R

BOX SIZE
32' x 64'

MODEL SQ. FT.
1,620

DATE PRINTED
11/21/2023

SCALE
1/8"=1'
* UNLESS OTHERWISE NOTED

PLAN NO.
CrossMod--3264-32-1_Hawthorne_R

SHEET NAME
EXTERIOR AREA CALCS

SHEET NO.
A2.2.

File Path:B:\Architecture\CrossMod\DWG Files\3264_HAWTHORNE\CrossMod--3264-32-1_Hawthorne_R.dwg, Last Saved By:Hutsella, Saved Date:11/21/2023 12:44 PM

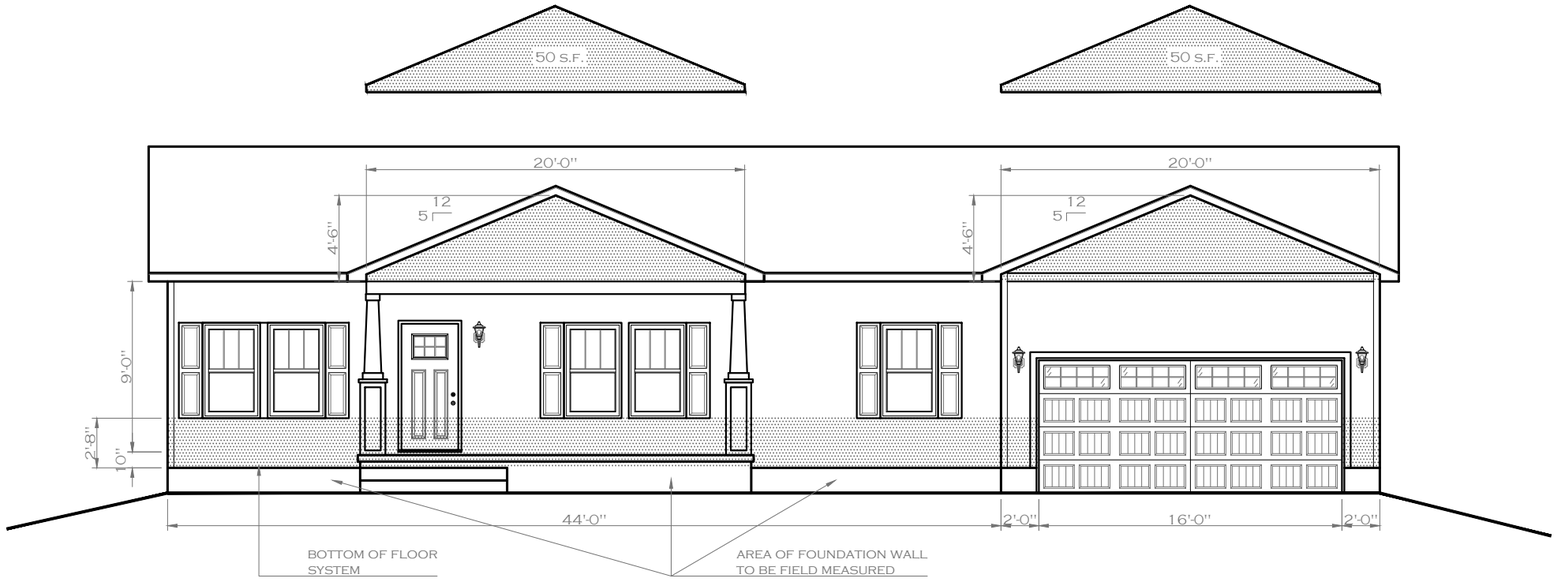


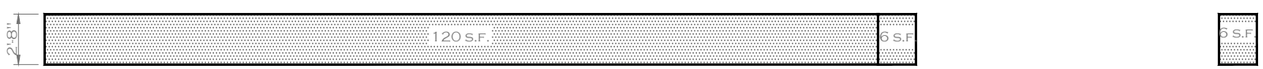


**HAWTHORNE FRONT ELEVATION**
**WITH SITE INSTALLED CLADDING**
**QUANTITY CALCS. WITH 9' CEILINGS**

NOTE: QUANTITIES SHOWN ON THIS DIAGRAM ARE ESTIMATES ONLY. THEY DO NOT ACCOUNT FOR WASTE.

Clayton Built

MODEL NAME
CrossMod_Hawthorne_R

MODEL NO.
CrossMod-3264-32-1_Hawthorne_R

BOX SIZE
32' x 64'

MODEL SQ. FT.
1,620

DATE PRINTED
11/21/2023

SCALE
1/8"=1'
* UNLESS OTHERWISE NOTED

PLAN NO.
CrossMod--3264-32-1_Hawthorne_R

SHEET NAME
EXTERIOR AREA CALCS

SHEET NO.
A2.3.

File Path:B:\Architecture\CrossMod\DWG Files\3264_HAWTHORNE\CrossMod--3264-32-1_Hawthorne_R.dwg, Last Saved By:Hutsella, Saved Date:11/21/2023 12:44 PM

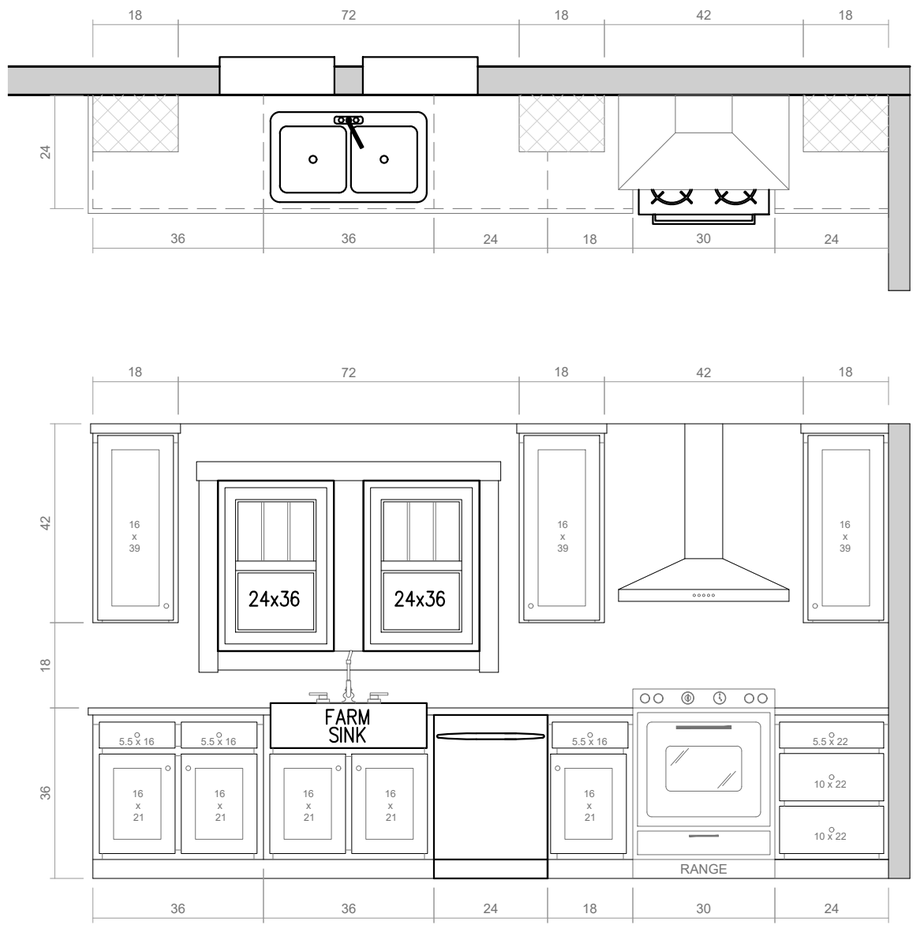


**KITCHEN ELEVATION @ SINK / OVEN WALL WITH**

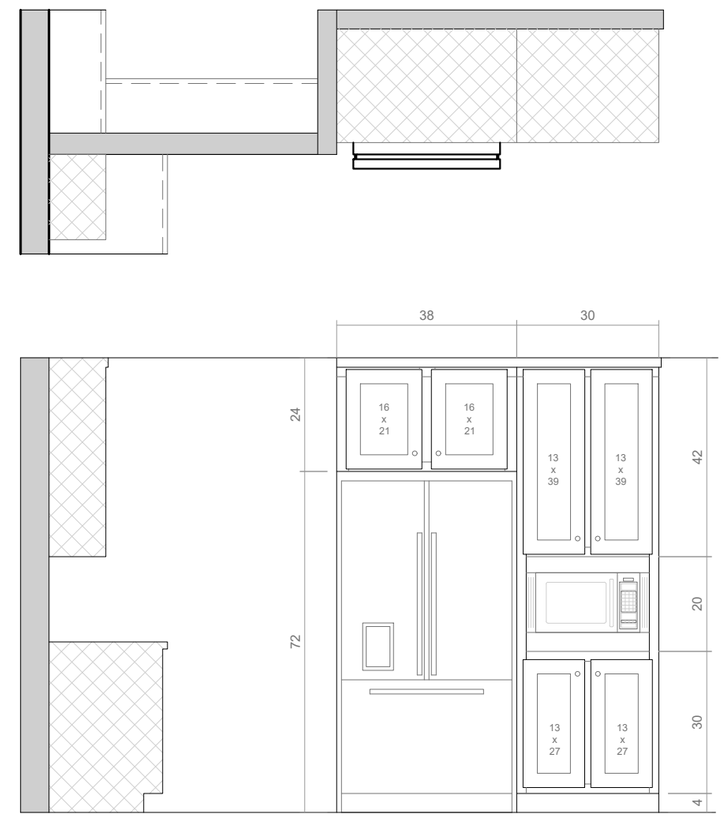


**KITCHEN ELEVATION @ REFER / MICROWAVE WALL**

Clayton Built

MODEL NAME
CrossMod_Hawthorne_R

MODEL NO.
CrossMod-3264-32-1_Hawthorne_R

BOX SIZE
32' x 64'

MODEL SQ. FT.
1,620

DATE PRINTED
11/21/2023

SCALE
3/8"=1'
*UNLESS OTHERWISE NOTED

PLAN NO.
CrossMod–3264-32-1_Hawthorne_R

SHEET NAME
CABINETS KITCHEN

SHEET NO.
A3.0.

File Path:B:\Architecture\CrossMod\DWG Files\3264_HAWTHORNE\CrossMod–3264-32-1_Hawthorne_R.dwg, Last Saved By:Hutsella, Saved Date:11/21/2023 12:44 PM

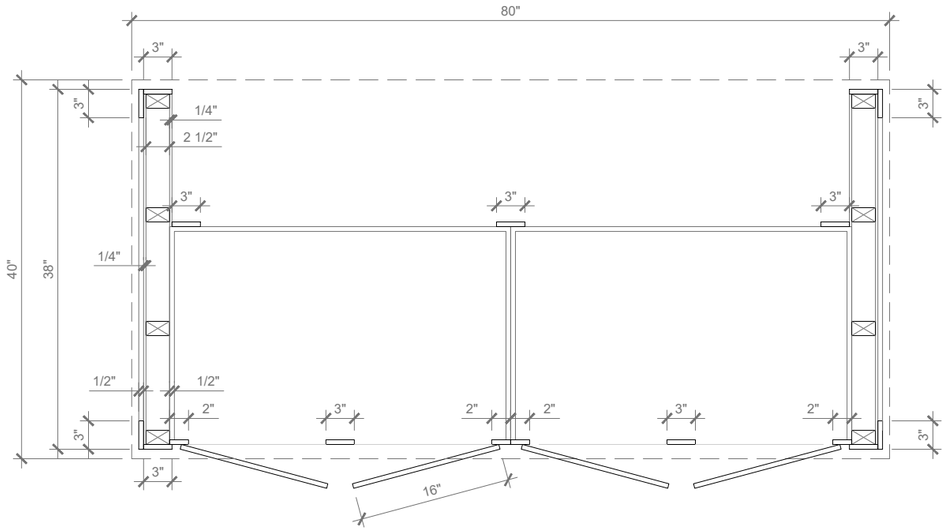


## ISLAND PLAN/SECTION

$\frac{3}{4}$" = 1'-0"

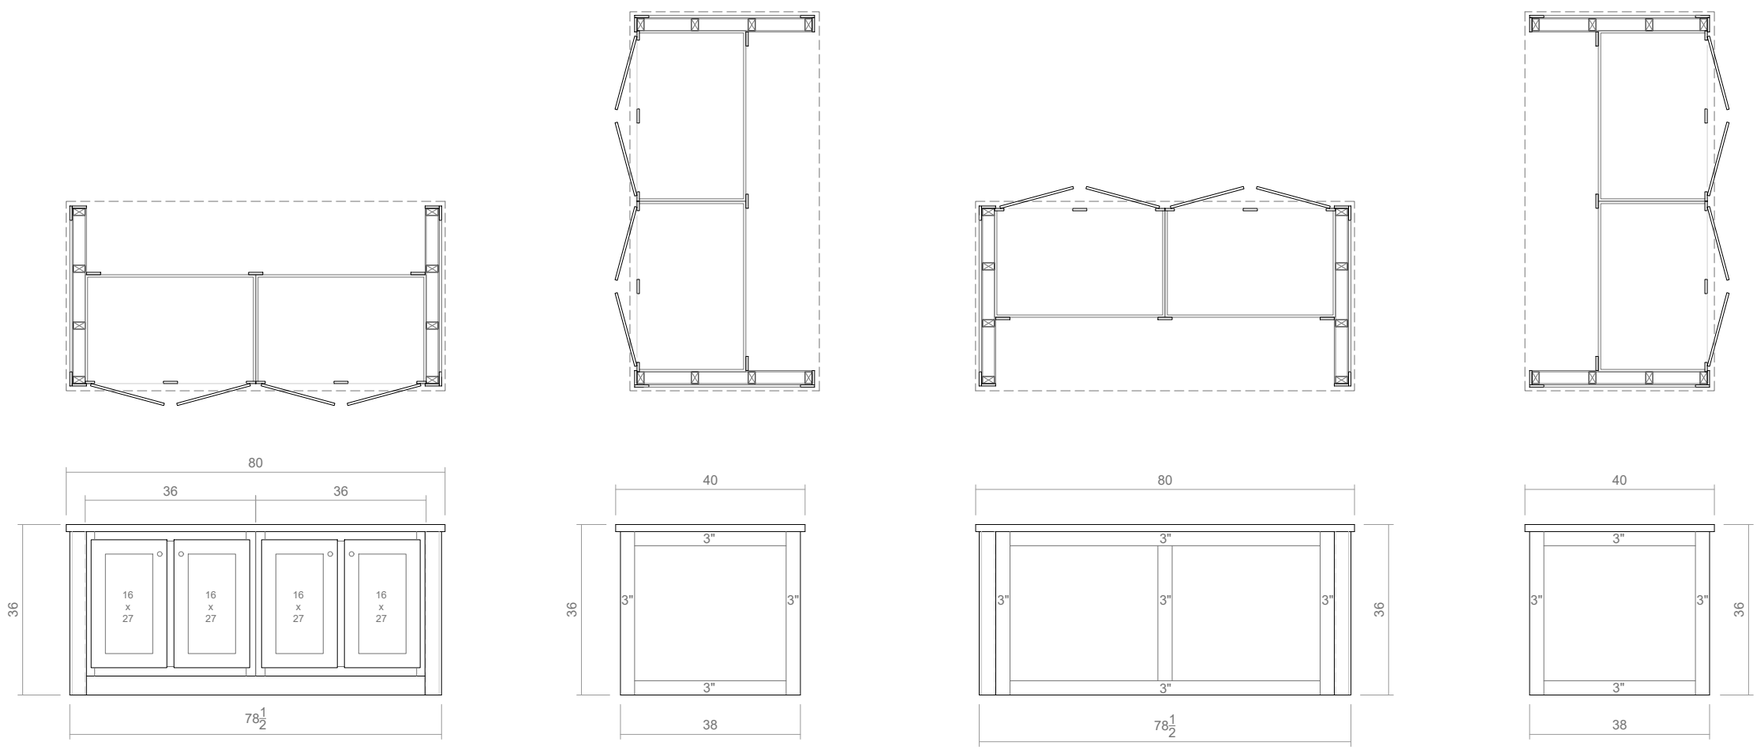


## ISLAND ELEVATIONS

$\frac{3}{8}$" = 1'-0"

Clayton Built

MODEL NAME
CrossMod_Hawthorne_R

MODEL NO.
CrossMod-3264-32-1_Hawthorne_R

BOX SIZE
32' x 64'

MODEL SQ. FT.
1,620

DATE PRINTED
11/21/2023

SCALE
VARIES
*UNLESS OTHERWISE NOTED

PLAN NO.
CrossMod--3264-32-1_Hawthorne_R

SHEET NAME
CABINETS KITCHEN

SHEET NO.
A3.1.

File Path:B:\Architecture\CrossMod\DWG Files\3264_HAWTHORNE\CrossMod--3264-32-1_Hawthorne_R.dwg, Last Saved By:Hutsella, Saved Date:11/21/2023 12:44 PM

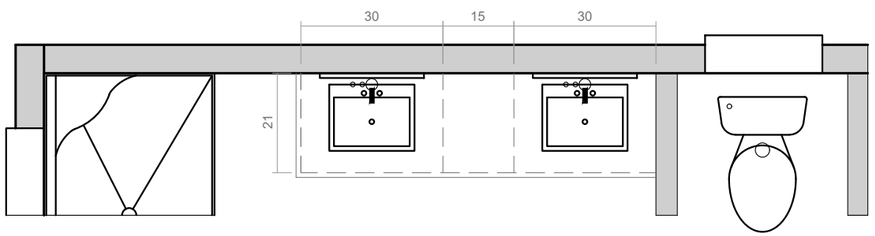


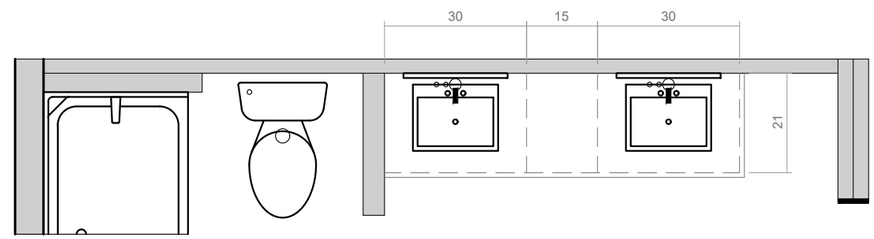


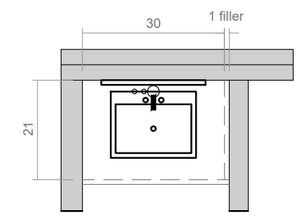


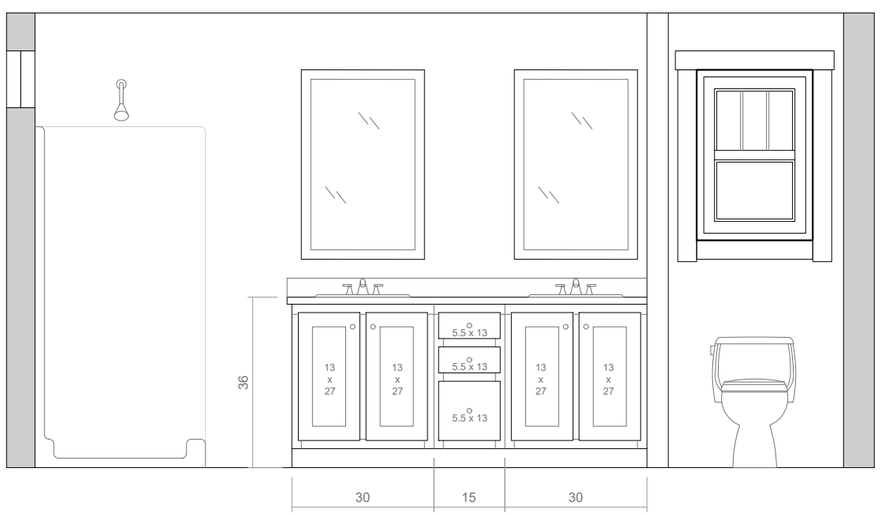


**PRIMARY BATH**
**VANITY ELEVATION**

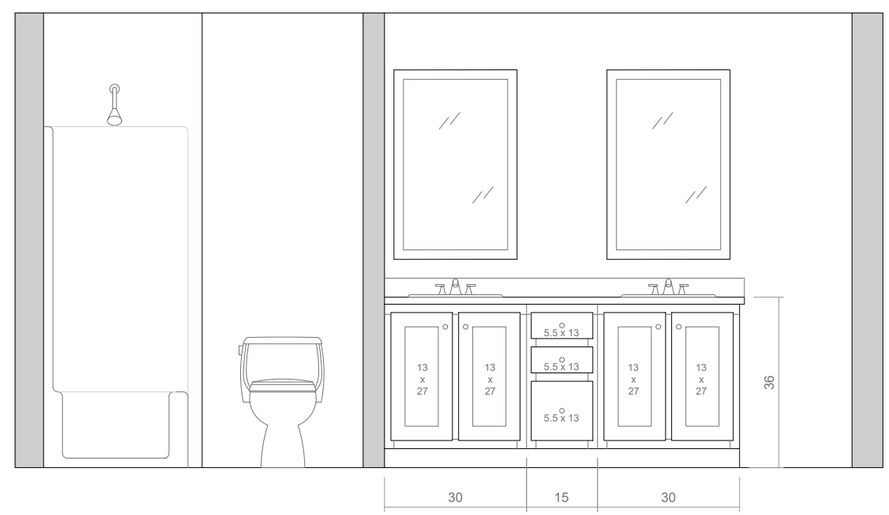


**HALL BATH**
**VANITY ELEVATION**

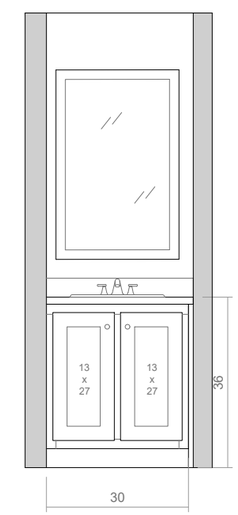


**HALF BATH**
**VANITY ELEVATION**

Clayton Built

MODEL NAME
CrossMod_Hawthorne_R

MODEL NO.
CrossMod-3264-32-1_Hawthorne_R

BOX SIZE
32' x 64'

MODEL SQ. FT.
1,620

DATE PRINTED
11/21/2023

SCALE
3/8"=1'
*UNLESS OTHERWISE NOTED

PLAN NO.
CrossMod--3264-32-1_Hawthorne_R

SHEET NAME
CABINETS BATH

SHEET NO.
A3.2

File Path:B:\Architecture\CrossMod\DWG Files\3264_HAWTHORNE\CrossMod--3264-32-1_Hawthorne_R.dwg, Last Saved By:Hutsella, Saved Date:11/21/2023 12:44 PM

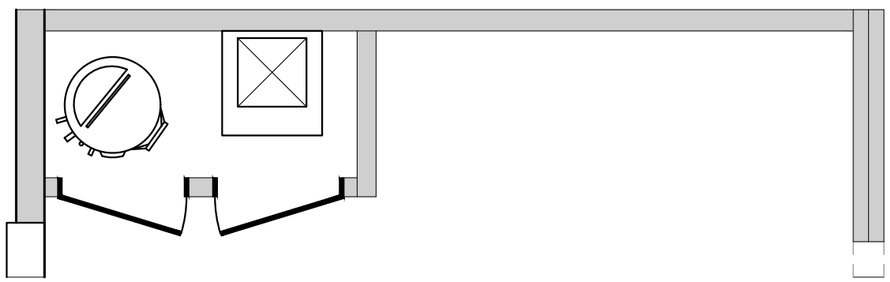

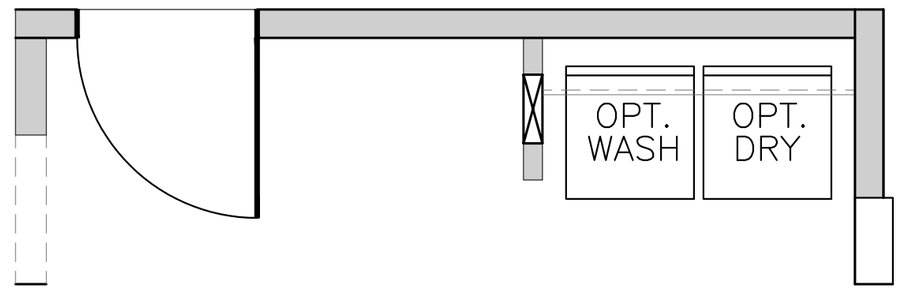


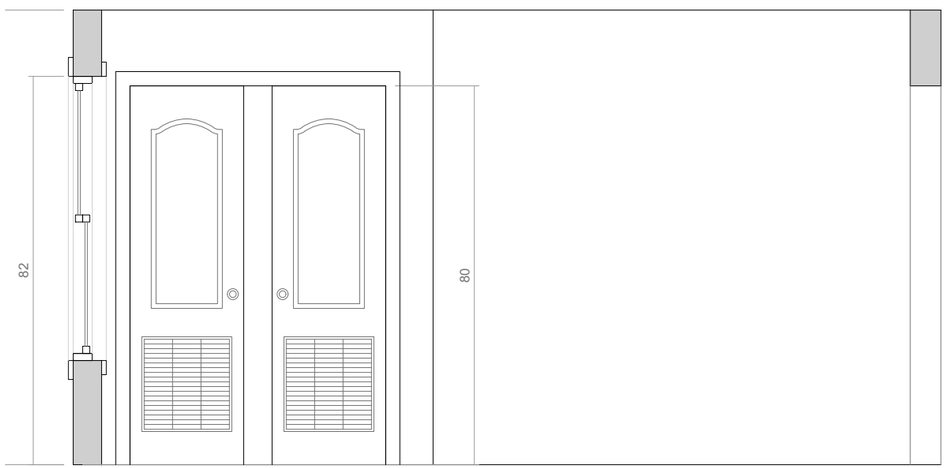


**INTERIOR ELEVATION @
UTILITY CLOSET**

**INTERIOR ELEVATION @
WASHER & DRYER**

Clayton Built

MODEL NAME
CrossMod_Hawthorne_R
MODEL NO.
CrossMod-3264-32-1_Hawthorne_R
BOX SIZE
32' x 64'
MODEL SQ. FT.
1,620

DATE PRINTED
11/21/2023

SCALE
3/8"=1'
*UNLESS OTHERWISE NOTED

PLAN NO.
CrossMod--3264-32-1_Hawthorne_R

SHEET NAME
MISC.
DETAILS

SHEET NO.
A3.3.

File Path:B:\Architecture\CrossMod\DWG Files\3264_HAWTHORNE\CrossMod--3264-32-1_Hawthorne_R.dwg, Last Saved By:Hutsella, Saved Date:11/21/2023 12:44 PM

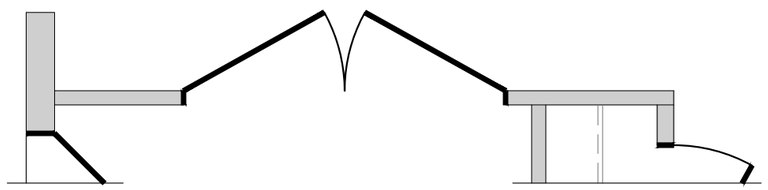

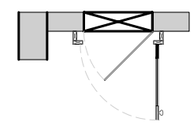

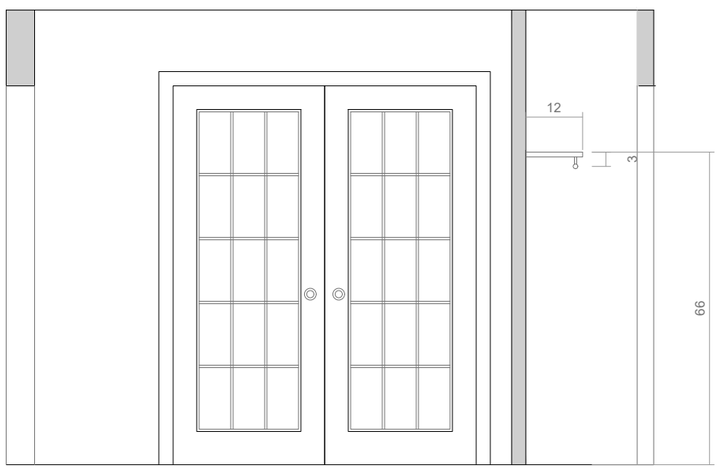


**OFFICE / FLEX**
**ENTRANCE ELEVATION**
**(glass doors to be locally sourced)**

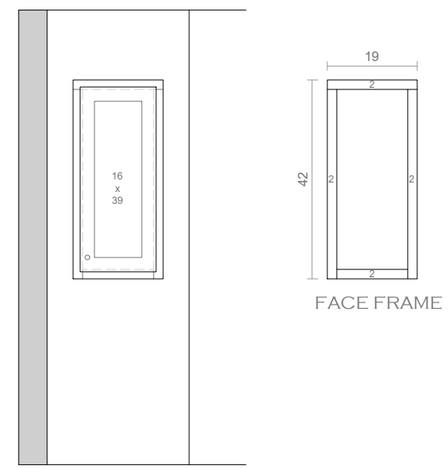


**PROPOSED CABINET DOOR**
**COVER @ PANEL BOX**
**(NEEDS TO BE PROTOTYPED)**

Clayton Built

MODEL NAME
CrossMod_Hawthorne_R
MODEL NO.
CrossMod-3264-32-1_Hawthorne_R
BOX SIZE
32' x 64'
MODEL SQ. FT.
1,620

DATE PRINTED
11/21/2023
SCALE
3/8"=1'
*UNLESS OTHERWISE NOTED
PLAN NO.
CrossMod--3264-32-1_Hawthorne_R
SHEET NAME
MISC. DETAILS
SHEET NO.
A3.4.

File Path:B:\Architecture\CrossMod\DWG Files\3264_HAWTHORNE\CrossMod--3264-32-1_Hawthorne_R.dwg, Last Saved By:Hutsella, Saved Date:11/21/2023 12:44 PM

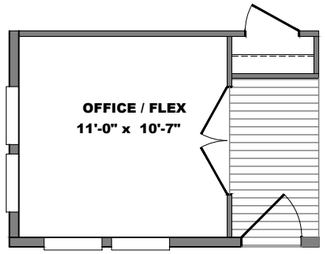


**OFFICE / FLEX SPACE OPTION**

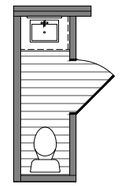

**HALF BATH OPTION**

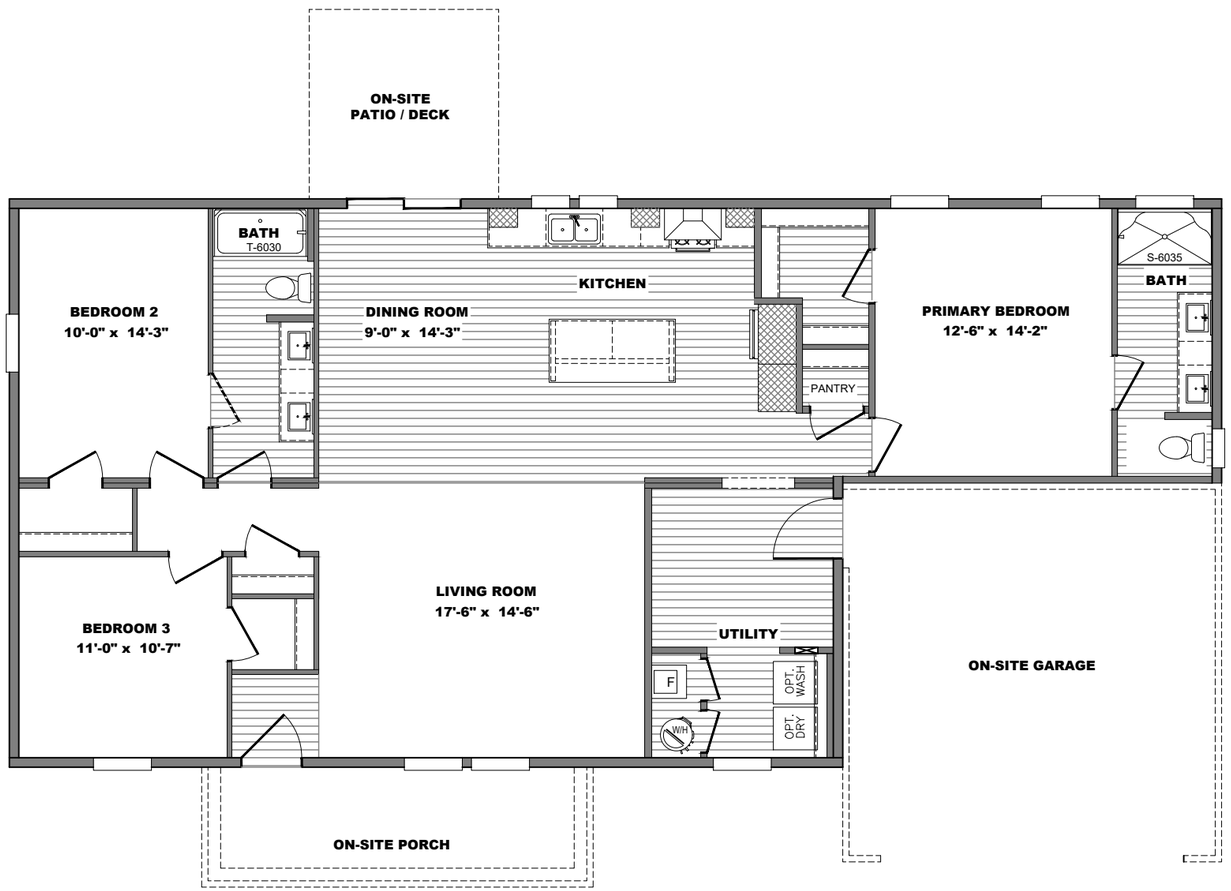


Clayton Built

MODEL NAME
CrossMod_Hawthorne_R

MODEL NO.
CrossMod-3264-32-1_Hawthorne_R

BOX SIZE
32' x 64'

MODEL SQ. FT.
1,620

DATE PRINTED
11/21/2023

SCALE
1/8"=1'
* UNLESS OTHERWISE NOTED

PLAN NO.
CrossMod--3264-32-1_Hawthorne_R

SHEET NAME
SALESLIT

SHEET NO.
A4.0.

File Path:B:\Architecture\CrossMod\DWG Files\3264_HAWTHORNE\CrossMod--3264-32-1_Hawthorne_R.dwg, Last Saved By:Hutsella, Saved Date:11/21/2023 12:44 PM

# "CrossMod_Hawthorne_R"

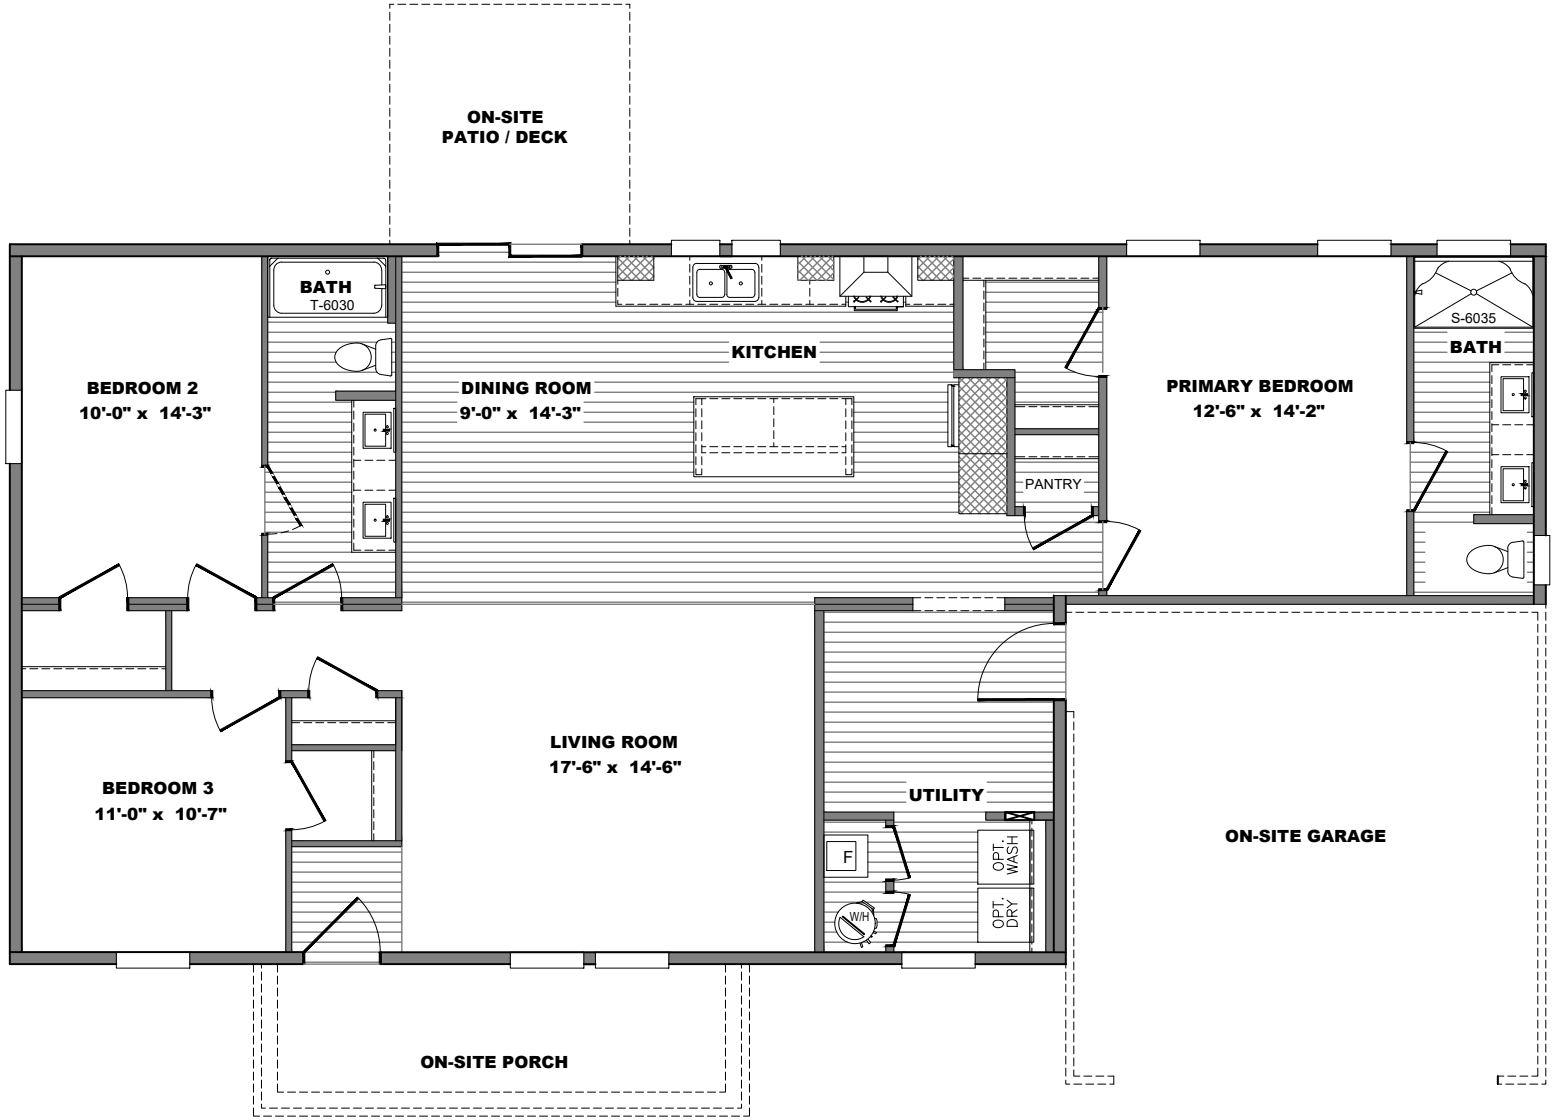


MODEL #CrossMod-3264-32-1_Hawthorne_R SQ.FT. 1,620 DRAWING # CROSSMOD-3264-32-1_HAWTHORNE_R

File Path:B:\Architecture\CrossMod\DWG Files\3264_HAWTHORNE\CrossMod--3264-32-1_Hawthorne_R.dwg, Last Saved By:Hutsella, Saved Date:11/21/2023 12:44 PM, Date Printed:11/21/23 12:50 PM

# "CrossMod_Hawthorne_R"

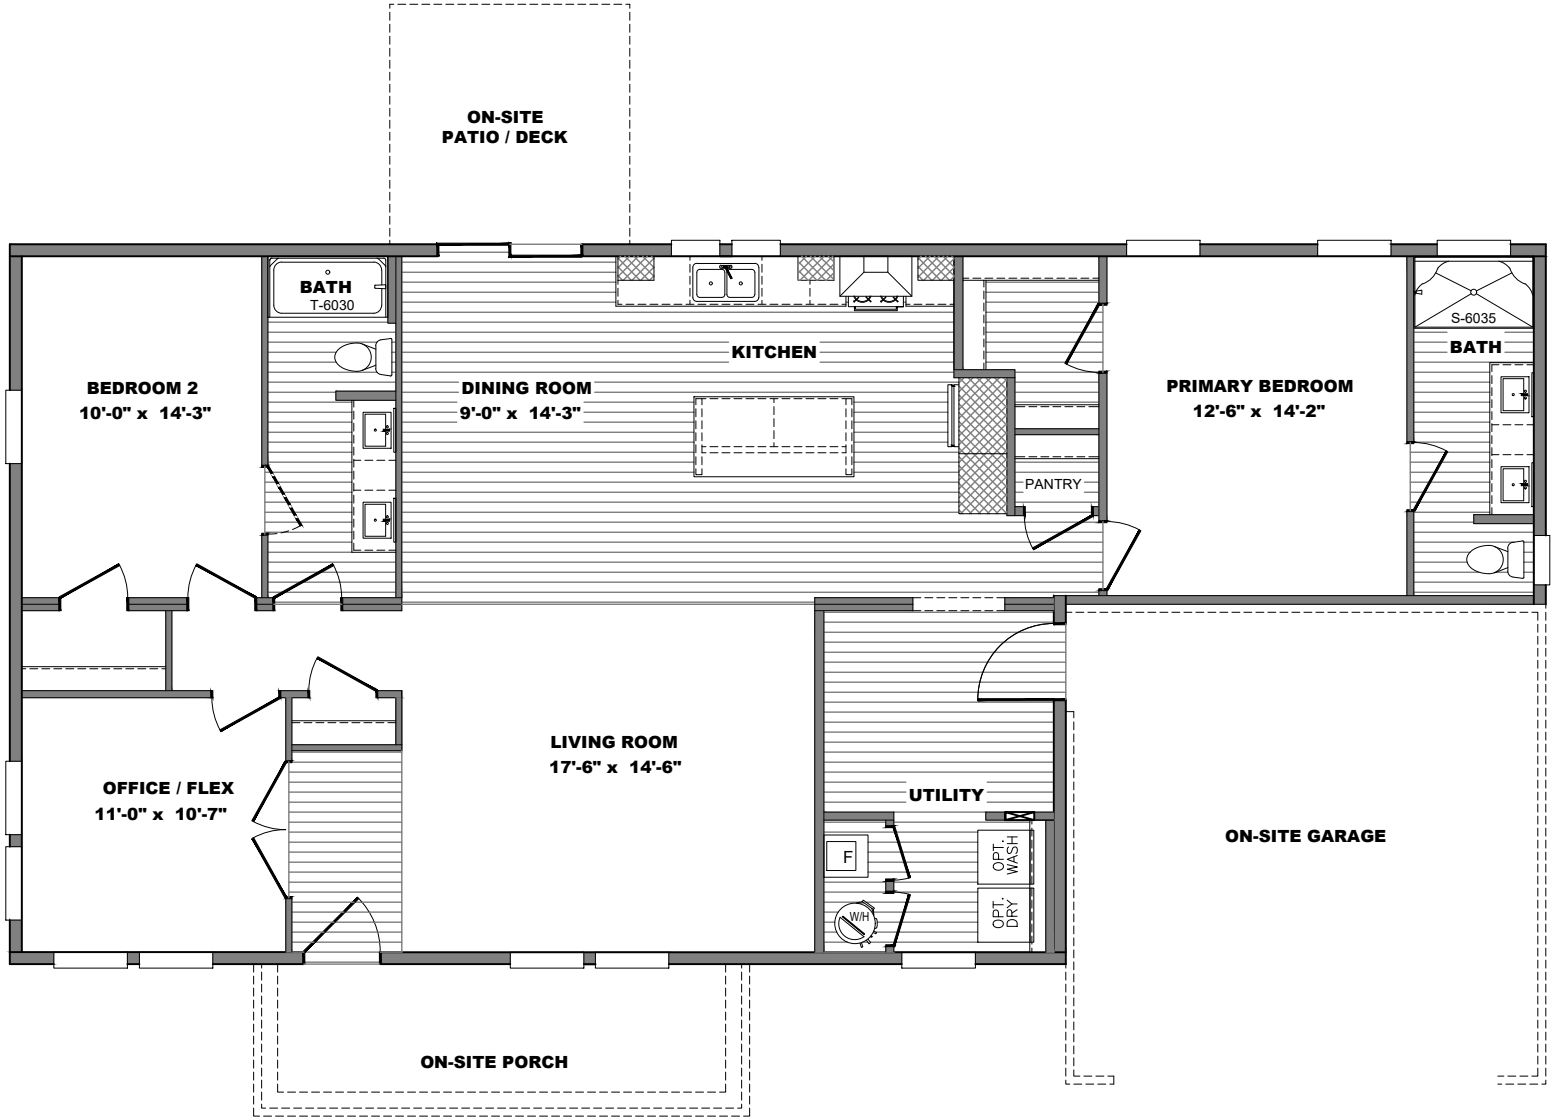


**FLOOR PLAN WITH OFFICE/FLEX OPTION**

MODEL #CrossMod-3264-32-1_Hawthorne_R SQ.FT. 1,620 DRAWING # CROSSMOD-3264-32-1_HAWTHORNE_R

File Path:B:\Architecture\CrossMod\DWG Files\3264_HAWTHORNE\CrossMod--3264-32-1_Hawthorne_R.dwg, Last Saved By:Hutsella, Saved Date:11/21/2023 12:44 PM, Date Printed:11/21/23 12:50 PM

# "CrossMod_Hawthorne_R"

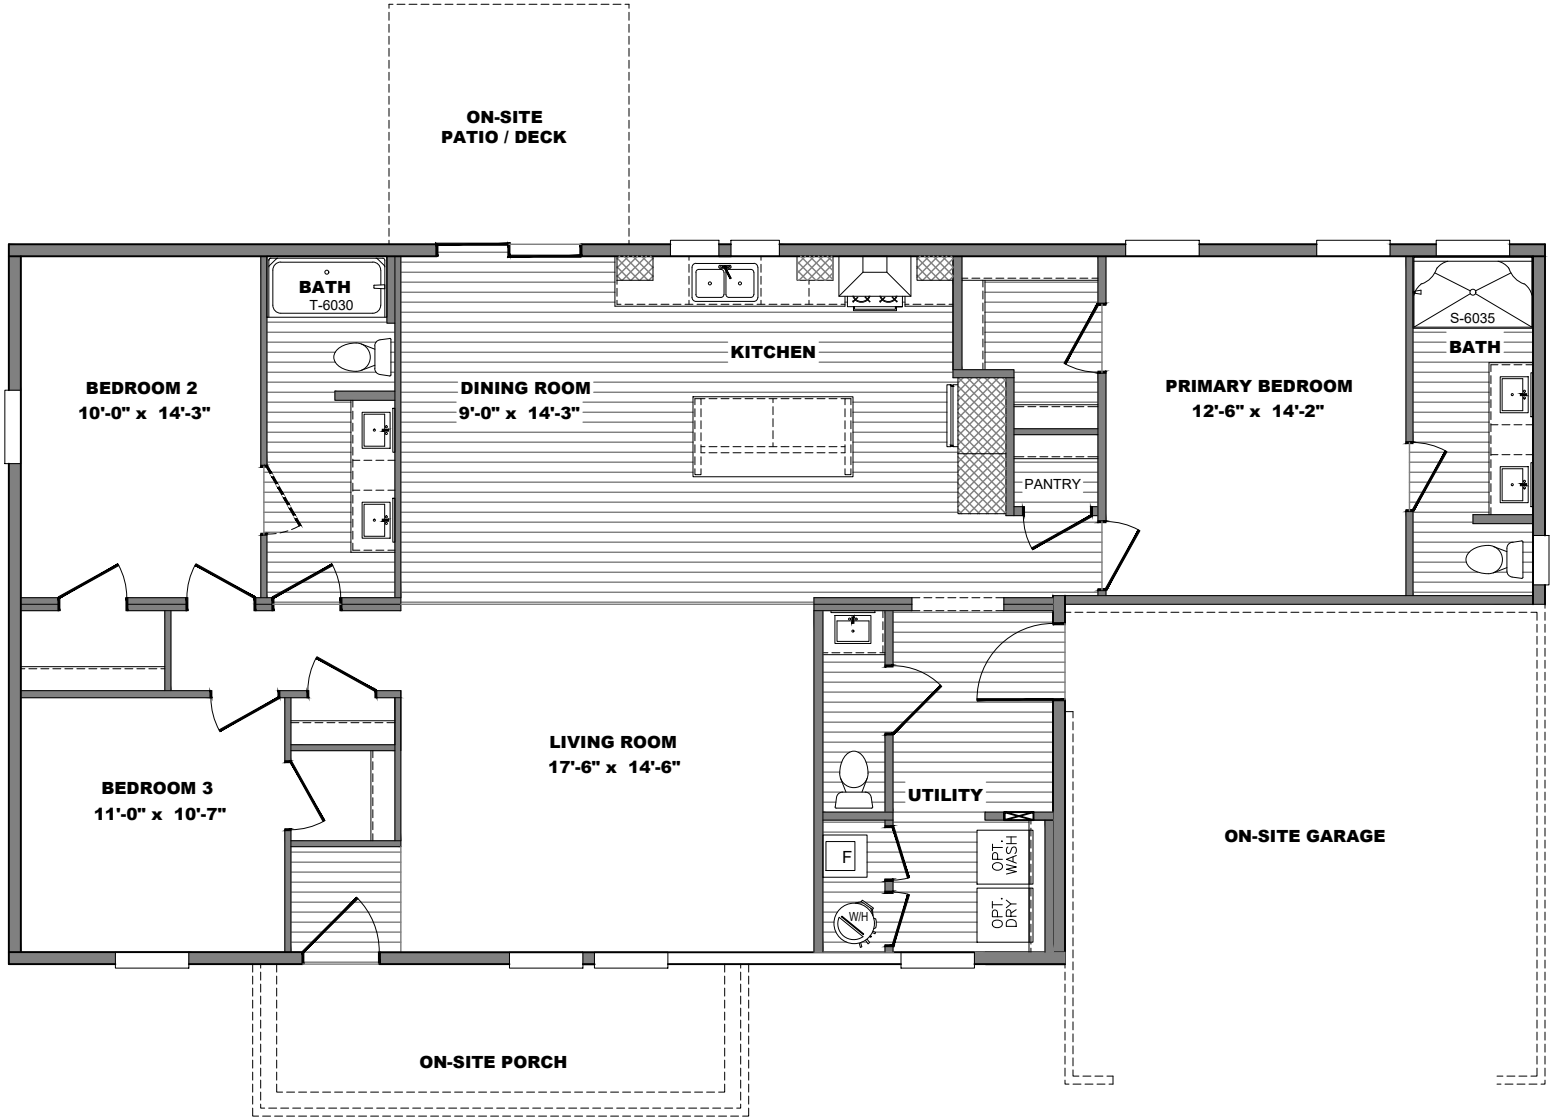


**FLOOR PLAN WITH HALF BATH OPTION**

MODEL #CrossMod-3264-32-1_Hawthorne_R SQ.FT. 1,620 DRAWING # CROSSMOD-3264-32-1_HAWTHORNE_R

File Path:B:\Architecture\CrossMod\DWG Files\3264_HAWTHORNE\CrossMod--3264-32-1_Hawthorne_R.dwg, Last Saved By:Hutsella, Saved Date:11/21/2023 12:44 PM, Date Printed:11/21/23 12:50 PM

# "CrossMod_Hawthorne_R"

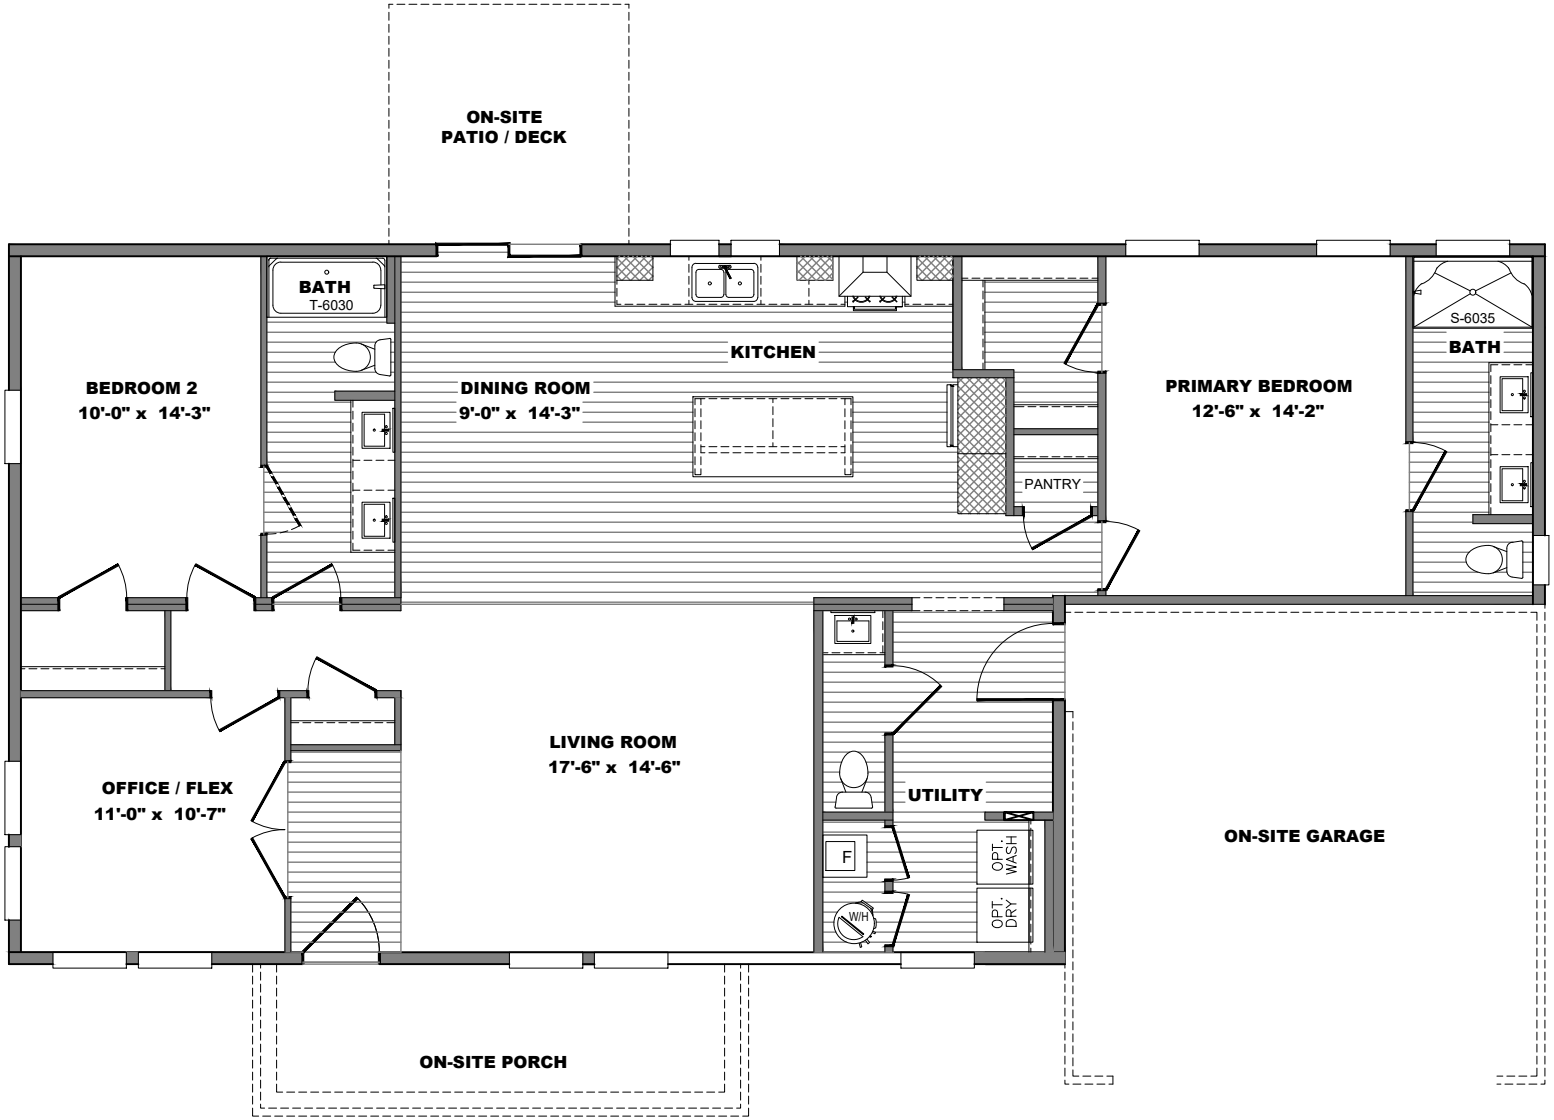


**FLOOR PLAN WITH HALF BATH AND OFFICE/FLEX OPTIONS.**

MODEL #CrossMod-3264-32-1_Hawthorne_R SQ.FT. 1,620 DRAWING # CROSSMOD-3264-32-1_HAWTHORNE_R

File Path:B:\Architecture\CrossMod\DWG Files\3264_HAWTHORNE\CrossMod--3264-32-1_Hawthorne_R.dwg, Last Saved By:Hutsella, Saved Date:11/21/2023 12:44 PM, Date Printed:11/21/23 12:50 PM