CROSS MOD
KEENELAND_R-BLN-3258-32-1

INDEX

A0.0	COVER SHEET
A1.0	FLOOR PLAN
A1.1	LIGHTING AND FLOOR REGISTER LAYOUT
A2.0	ELEVATIONS - STANDARD
A3.0	INTERIOR DETAILS - KITCHEN
A3.1	INTERIOR DETAILS - KITCHEN
A3.2	INTERIOR DETAILS - BATHS
A3.3	INTERIOR DETAILS - MISC
A4.0	SALESLIT PRINT
	SALESLIT

GENERAL NOTES

1. THIS PACKAGE IS INTENDED TO RELAY DESIGN INTENT AND IS NOT FOR CONSTRUCTION.
2. PLEASE CONTACT ANDY HUTSELL AT ANDY.HUTSELL@CLAYTONHOMES.COM WITH QUESTIONS REGARDING THESE DRAWINGS.

SYMBOLS AND ABBREVIATIONS

CLG	CEILING
DR	DOOR
EF	EXHAUST FAN
FLR	FLOOR
MNT	MOUNT
OPT	OPTIONAL
RAG	RETURN AIR GRILLE
SEP	STANDARD ELECTRIC PANEL
SGD	SLIDING GLASS DOOR

Clayton Built

MODEL NAME
Keeneland_R
MODEL NO.
BLN-3258-32-1
BOX SIZE
32' x 58'
MODEL SQ. FT.
1.635

DATE PRINTED
4/25/2024

SCALE
N.T.S.
*UNLESS OTHERWISE NOTED

PLAN NO.
BLN-3258-32-1_Keeneland_R

SHEET NAME
COVER SHEET

SHEET NO.
A0.0.

File Path:B:\Architecture\CrossMod\DWG Files\3258_KEENELAND\BLN-3258-32-1_Keeneland_R.dwg, Last Saved By:HutsellA, Saved Date:4/25/2024 11:46 AM

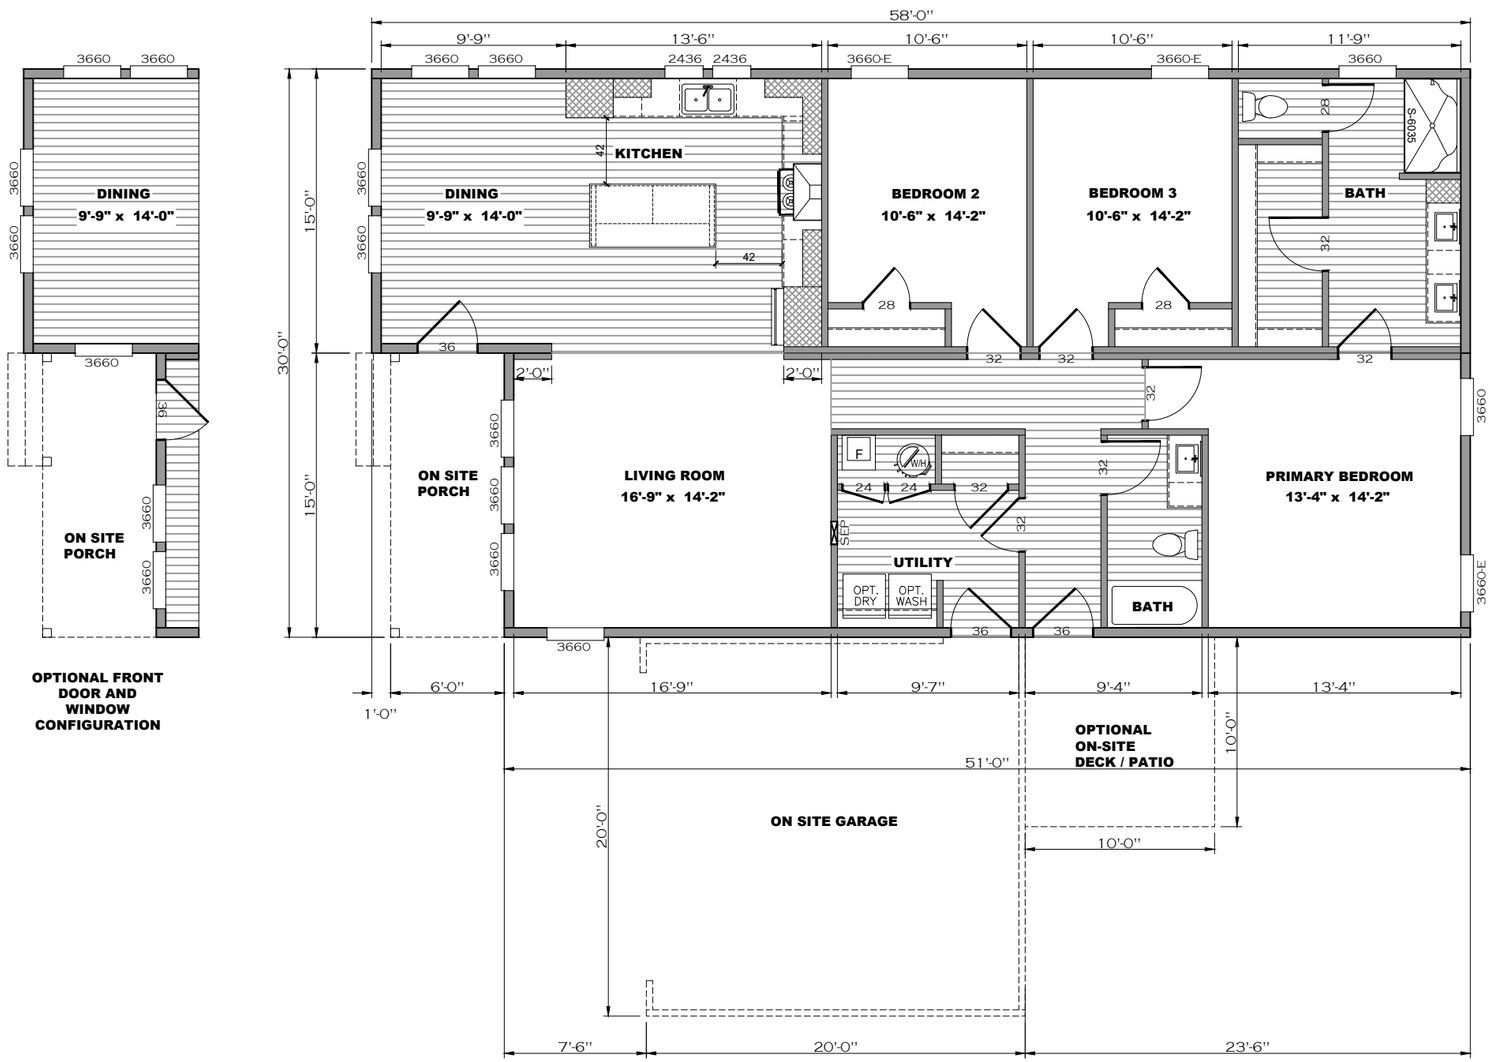

FLOOR PLAN

Clayton Built

MODEL NAME
Keeneland_R

MODEL NO.
BLN-3258-32-1

MODEL SQ. FT.
1,635

BOX SIZE
32' x 58'

DATE PRINTED
4/25/2024

SCALE
1/8"=1'
* UNLESS OTHERWISE NOTED

PLAN NO.
BLN-3258-32-1_Keeneland_R

SHEET NAME
FLOOR PLAN

SHEET NO.
A1.0.

File Path:B:\Architecture\CrossMod\DWG Files\3258_KEENELAND\BLN-3258-32-1_Keeneland_R.dwg, Last Saved By:HutsellA, Saved Date:4/25/2024 11:46 AM

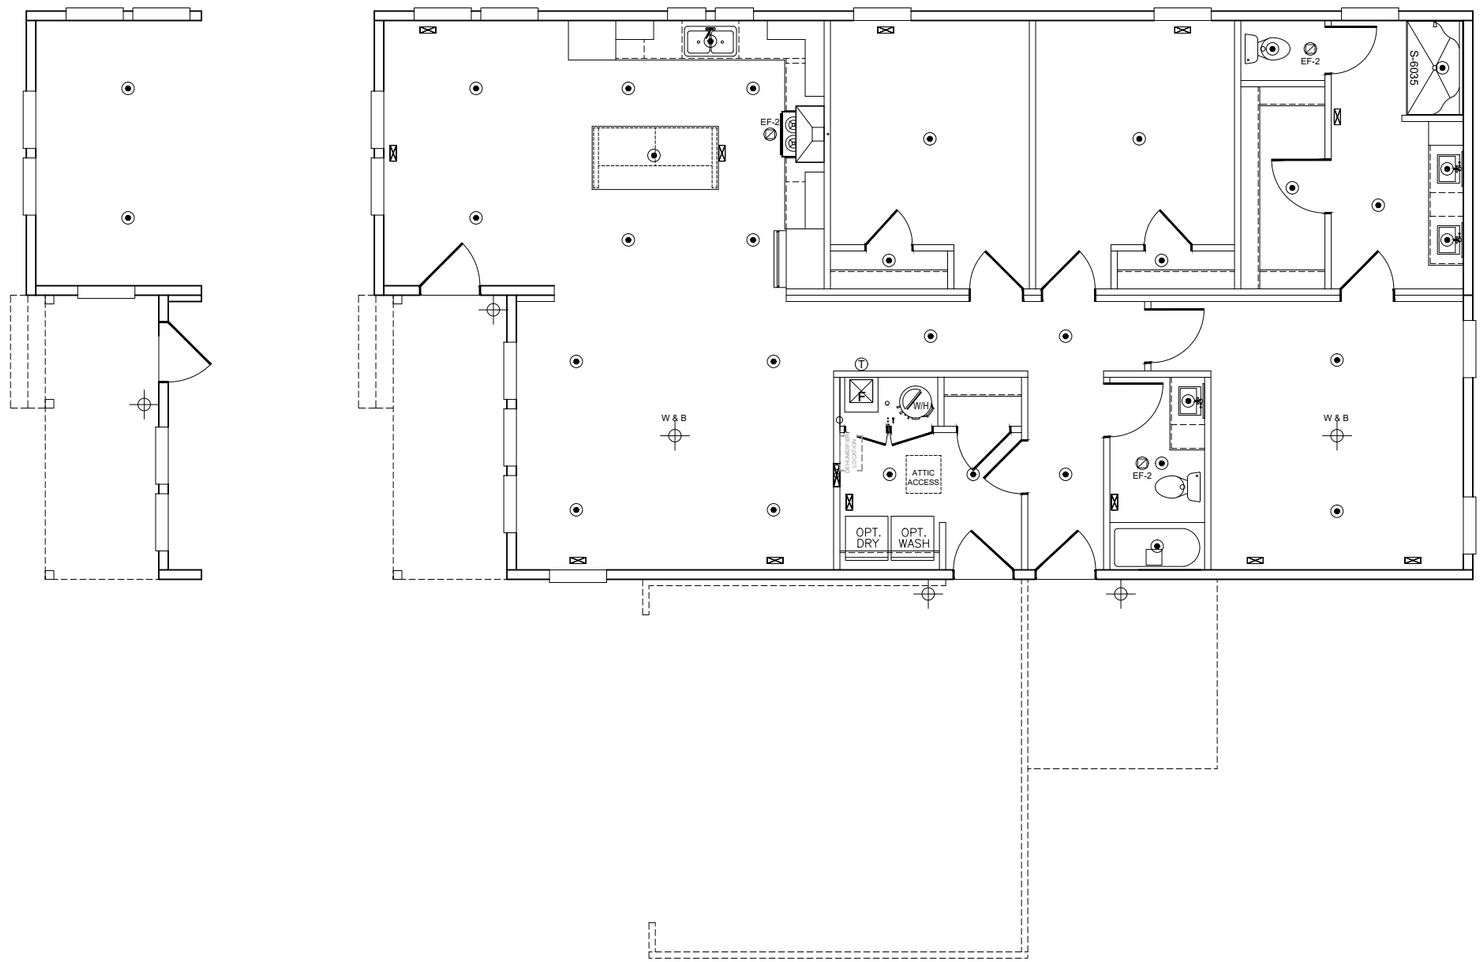

LIGHTING AND FLOOR REGISTER LAYOUT

SYMBOLS LEGEND

W & B	OPT. CEILING FAN or WIRE & BRACE
	WALL OR CEILING MNT FIXTURE
	CAN LIGHT
EF-2	BATH FAN
	HVAC REGISTER
F	HVAC FURNACE
W/H	WATER HEATER
T	THERMOSTAT
EF-4	WHOLE HOUSE VENT
DEHUMIDIFIER LOCATION	DEHUMIDIFIER LOCATION
ATTIC ACCESS	ATTIC ACCESS

NOTES:

1. ALL SYMBOLS MAY NOT BE APPLICABLE TO ALL PROJECTS.

Clayton Built

MODEL NAME
Keeneland_R

MODEL NO.
BLN-3258-32-1

BOX SIZE
32' x 58'

MODEL SQ. FT.
1,635

DATE PRINTED
4/25/2024

SCALE
1/8"=1'
* UNLESS OTHERWISE NOTED

PLAN NO.
BLN-3258-32-1_Keeneland_R

SHEET NAME
ELEC. PLAN

SHEET NO.
A1.1.

File Path:B:\Architecture\CrossMod\DWG Files\3258_KEENELAND\BLN-3258-32-1_Keeneland_R.dwg, Last Saved By:HutsellA, Saved Date:4/25/2024 11:46 AM

FRONT ELEVATION

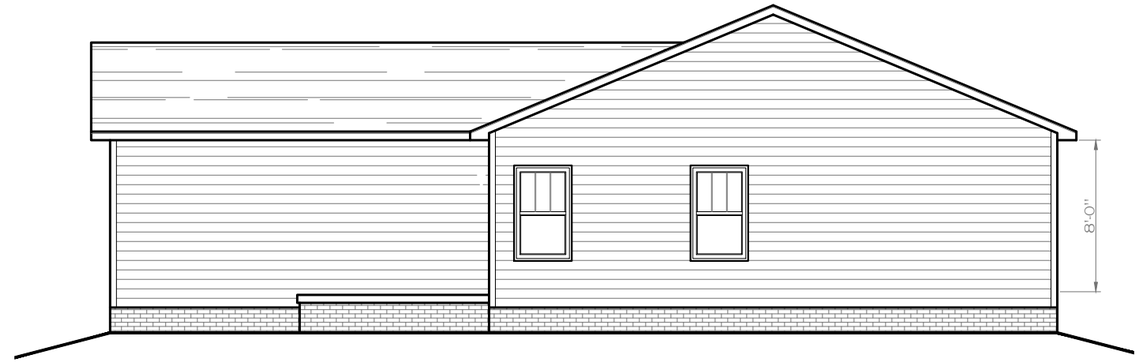

REAR ELEVATION

RIGHT SIDE ELEVATION

LEFT SIDE ELEVATION

Clayton Built

MODEL NAME
Keeneland_R

MODEL NO.
BLN-3258-32-1

BOX SIZE
32' x 58'

MODEL SQ. FT.
1,635

DATE PRINTED
4/25/2024

SCALE
1/8"=1'
* UNLESS OTHERWISE NOTED

PLAN NO.
BLN-3258-32-1_Keeneland_R

SHEET NAME
EXTERIOR ELEVATION

SHEET NO.
A2.0.

File Path:B:\Architecture\CrossMod\DWG Files\3258_KEENELAND\BLN-3258-32-1_Keeneland_R.dwg, Last Saved By:HutsellA, Saved Date:4/25/2024 11:46 AM

FRONT ELEVATION
(FOR OPT. DOOR LOCATION)
note: for this option, shutters are not available.

RIGHT SIDE ELEVATION
(FOR OPT. FRONT DOOR LOCATION)
note: for this options, shutters are not available.

Clayton Built

MODEL NAME
Keeneland_R
MODEL NO.
BLN-3258-32-1
MODEL SQ. FT.
1,635
BOX SIZE
32' x 58'

DATE PRINTED
4/25/2024

SCALE
1/8"=1'
* UNLESS OTHERWISE NOTED

PLAN NO.
BLN-3258-32-1_Keeneland_R

SHEET NAME
EXTERIOR ELEVATION

SHEET NO.
A2.1.

File Path:B:\Architecture\CrossMod\DWG Files\3258_KEENELAND\BLN-3258-32-1_Keeneland_R.dwg, Last Saved By:HutsellA, Saved Date:4/25/2024 11:46 AM

KITCHEN ELEVATION @ SINK / DISHWASHER

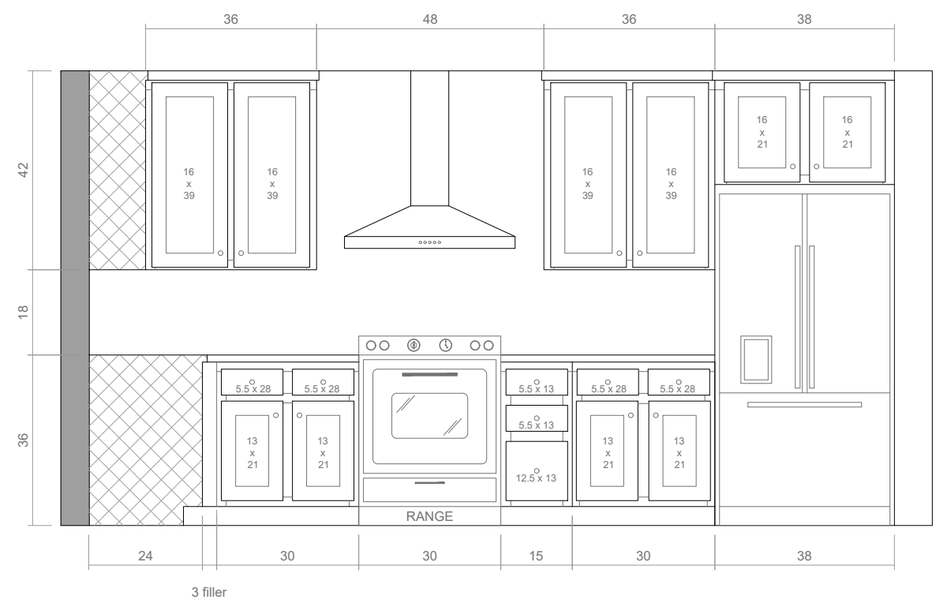

KITCHEN ELEVATION @ OVEN / REFRIDGERATOR

Clayton Built

MODEL NAME
Keeneland_R

MODEL NO.
BLN-3258-32-1

BOX SIZE
32' x 58'

MODEL SQ. FT.
1,635

DATE PRINTED
4/25/2024

SCALE
3/8"=1'
* UNLESS OTHERWISE NOTED

PLAN NO.
BLN-3258-32-1_Keeneland_R

SHEET NAME
CABINETS KITCHEN

SHEET NO.
A3.0.

File Path:B:\Architecture\CrossMod\DWG Files\3258_KEENELAND\BLN-3258-32-1_Keeneland_R.dwg, Last Saved By:HutsellA, Saved Date:4/25/2024 11:46 AM

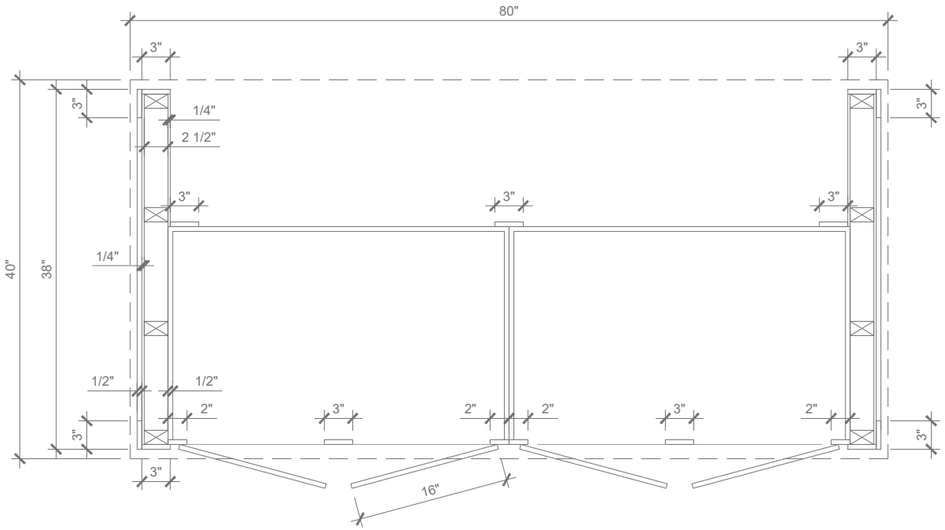

ISLAND PLAN/SECTION

$\frac{3}{4}$" = 1'-0"

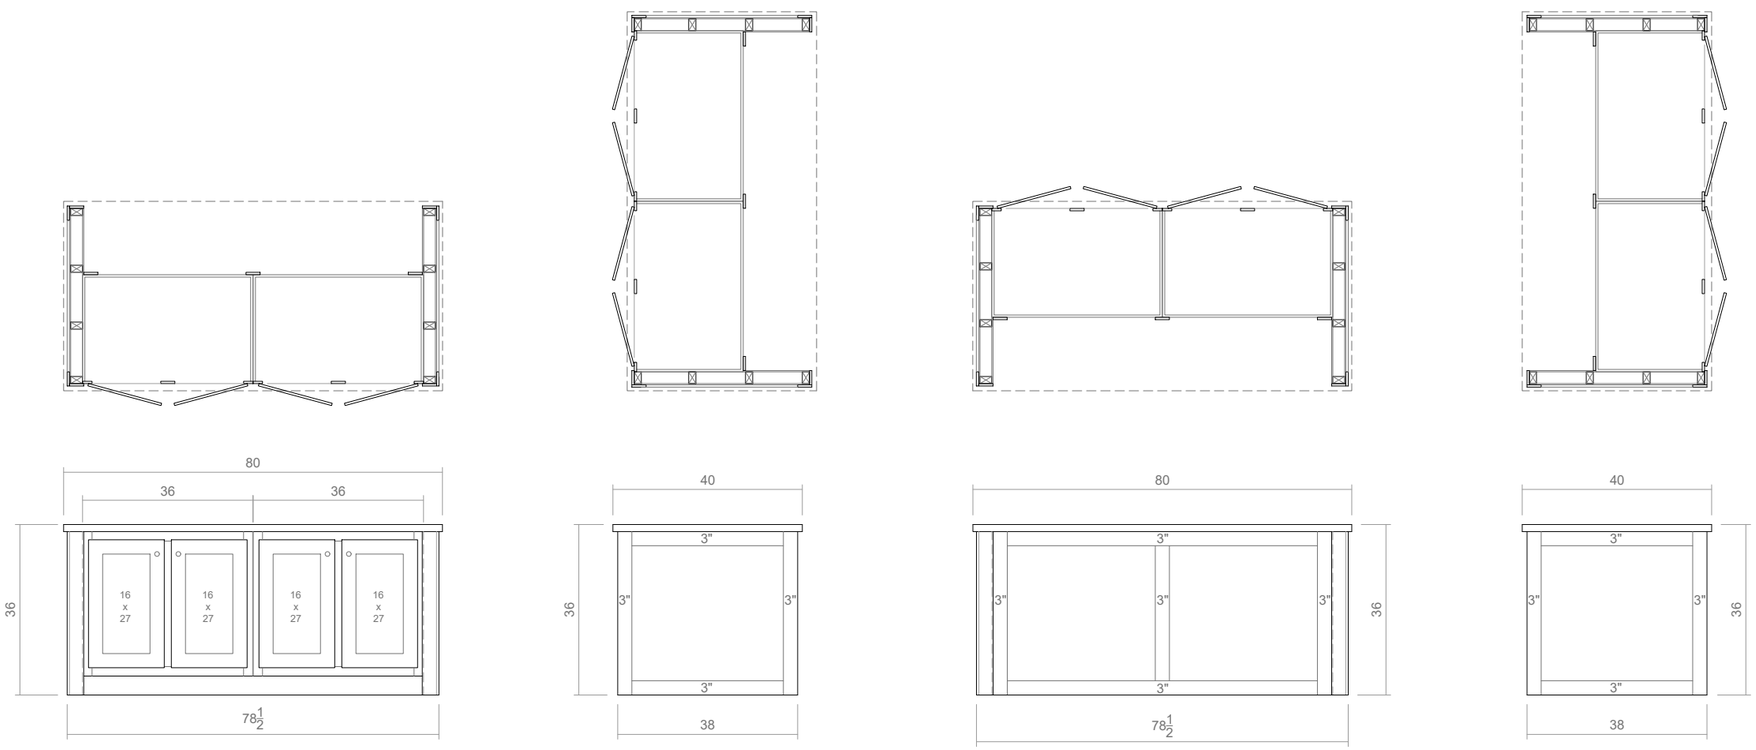

ISLAND ELEVATIONS

$\frac{3}{8}$" = 1'-0"

Clayton Built

MODEL NAME
Keeneland_R

MODEL NO.
BLN-3258-32-1

BOX SIZE
32' x 58'

MODEL SQ. FT.
1,635

DATE PRINTED
4/25/2024

SCALE
VARIES
* UNLESS OTHERWISE NOTED

PLAN NO.
BLN-3258-32-1_Keeneland_R

SHEET NAME
CABINETS KITCHEN

SHEET NO.
A3.1.

File Path:B:\Architecture\CrossMod\DWG Files\3258_KEENELAND\BLN-3258-32-1_Keeneland_R.dwg, Last Saved By:HutsellA, Saved Date:4/25/2024 11:46 AM

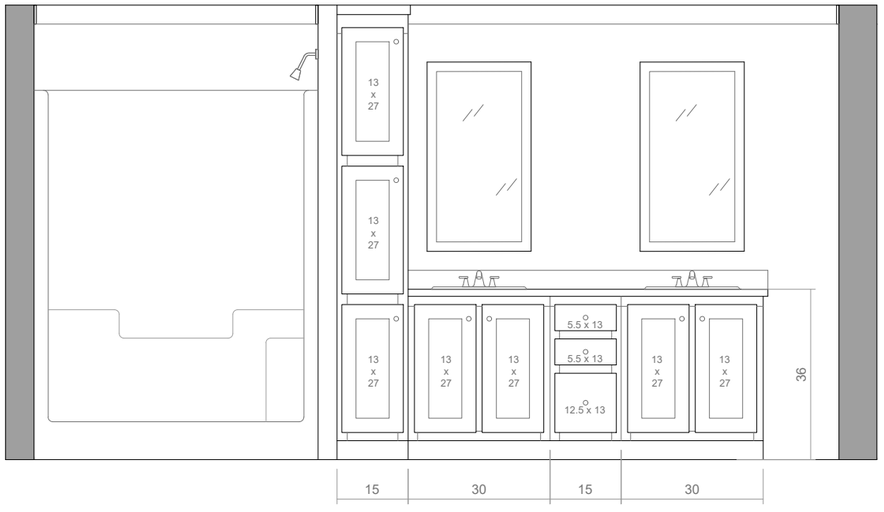

PRIMARY BATH
VANITY ELEVATION

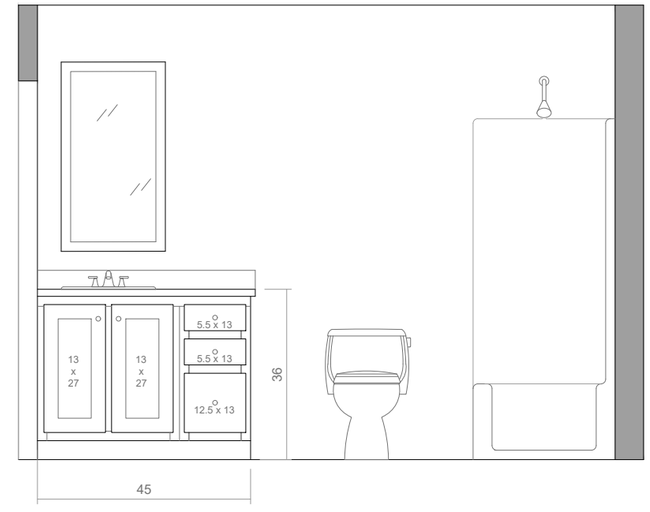

HALL BATHROOM
VANITY ELEVATION

Clayton Built

MODEL NAME
Keeneland_R
MODEL NO.
BLN-3258-32-1
BOX SIZE
32' x 58'
MODEL SQ. FT.
1,635

DATE PRINTED
4/25/2024

SCALE
3/8"=1'
* UNLESS OTHERWISE NOTED

PLAN NO.
BLN-3258-32-1_Keeneland_R

SHEET NAME
CABINETS BATH

SHEET NO.
A3.2

File Path:B:\Architecture\CrossMod\DWG Files\3258_KEENELAND\BLN-3258-32-1_Keeneland_R.dwg, Last Saved By:HutsellA, Saved Date:4/25/2024 11:46 AM

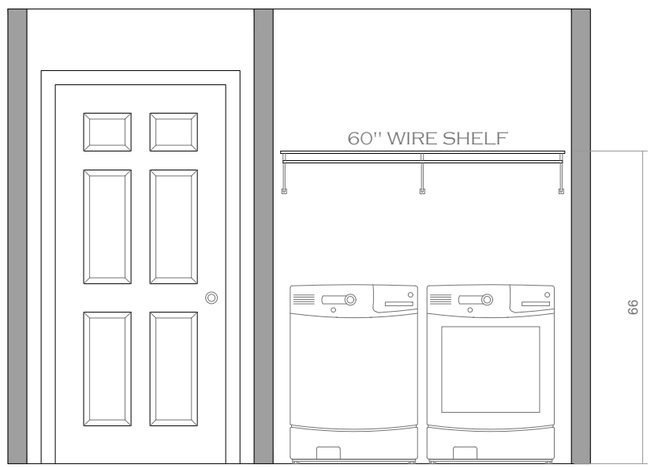

INTERIOR ELEVATION @ WASHER / DRYER

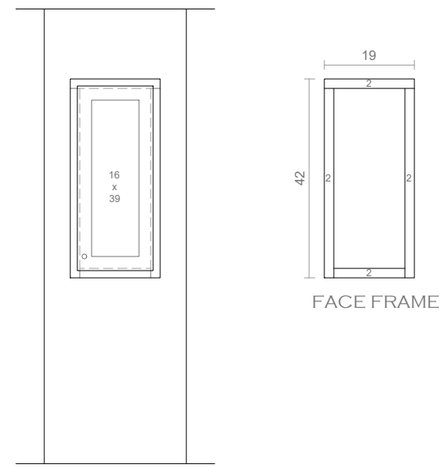

PROPOSED CABINET DOOR COVER @ PANEL BOX (NEEDS TO BE PROTOTYPED)

Clayton Built

MODEL NAME
Keeneland_R

MODEL NO.
BLN-3258-32-1

MODEL SQ. FT.
1.635

BOX SIZE
32' x 58'

DATE PRINTED
4/25/2024

SCALE
3/8"=1'
* UNLESS OTHERWISE NOTED

PLAN NO.
BLN-3258-32-1_Keeneland_R

SHEET NAME
MISC. DETAILS

SHEET NO.
A3.3.

File Path:B:\Architecture\CrossMod\DWG Files\3258_KEENELAND\BLN-3258-32-1_Keeneland_R.dwg, Last Saved By:HutsellA, Saved Date:4/25/2024 11:46 AM

"Keeneland_R"

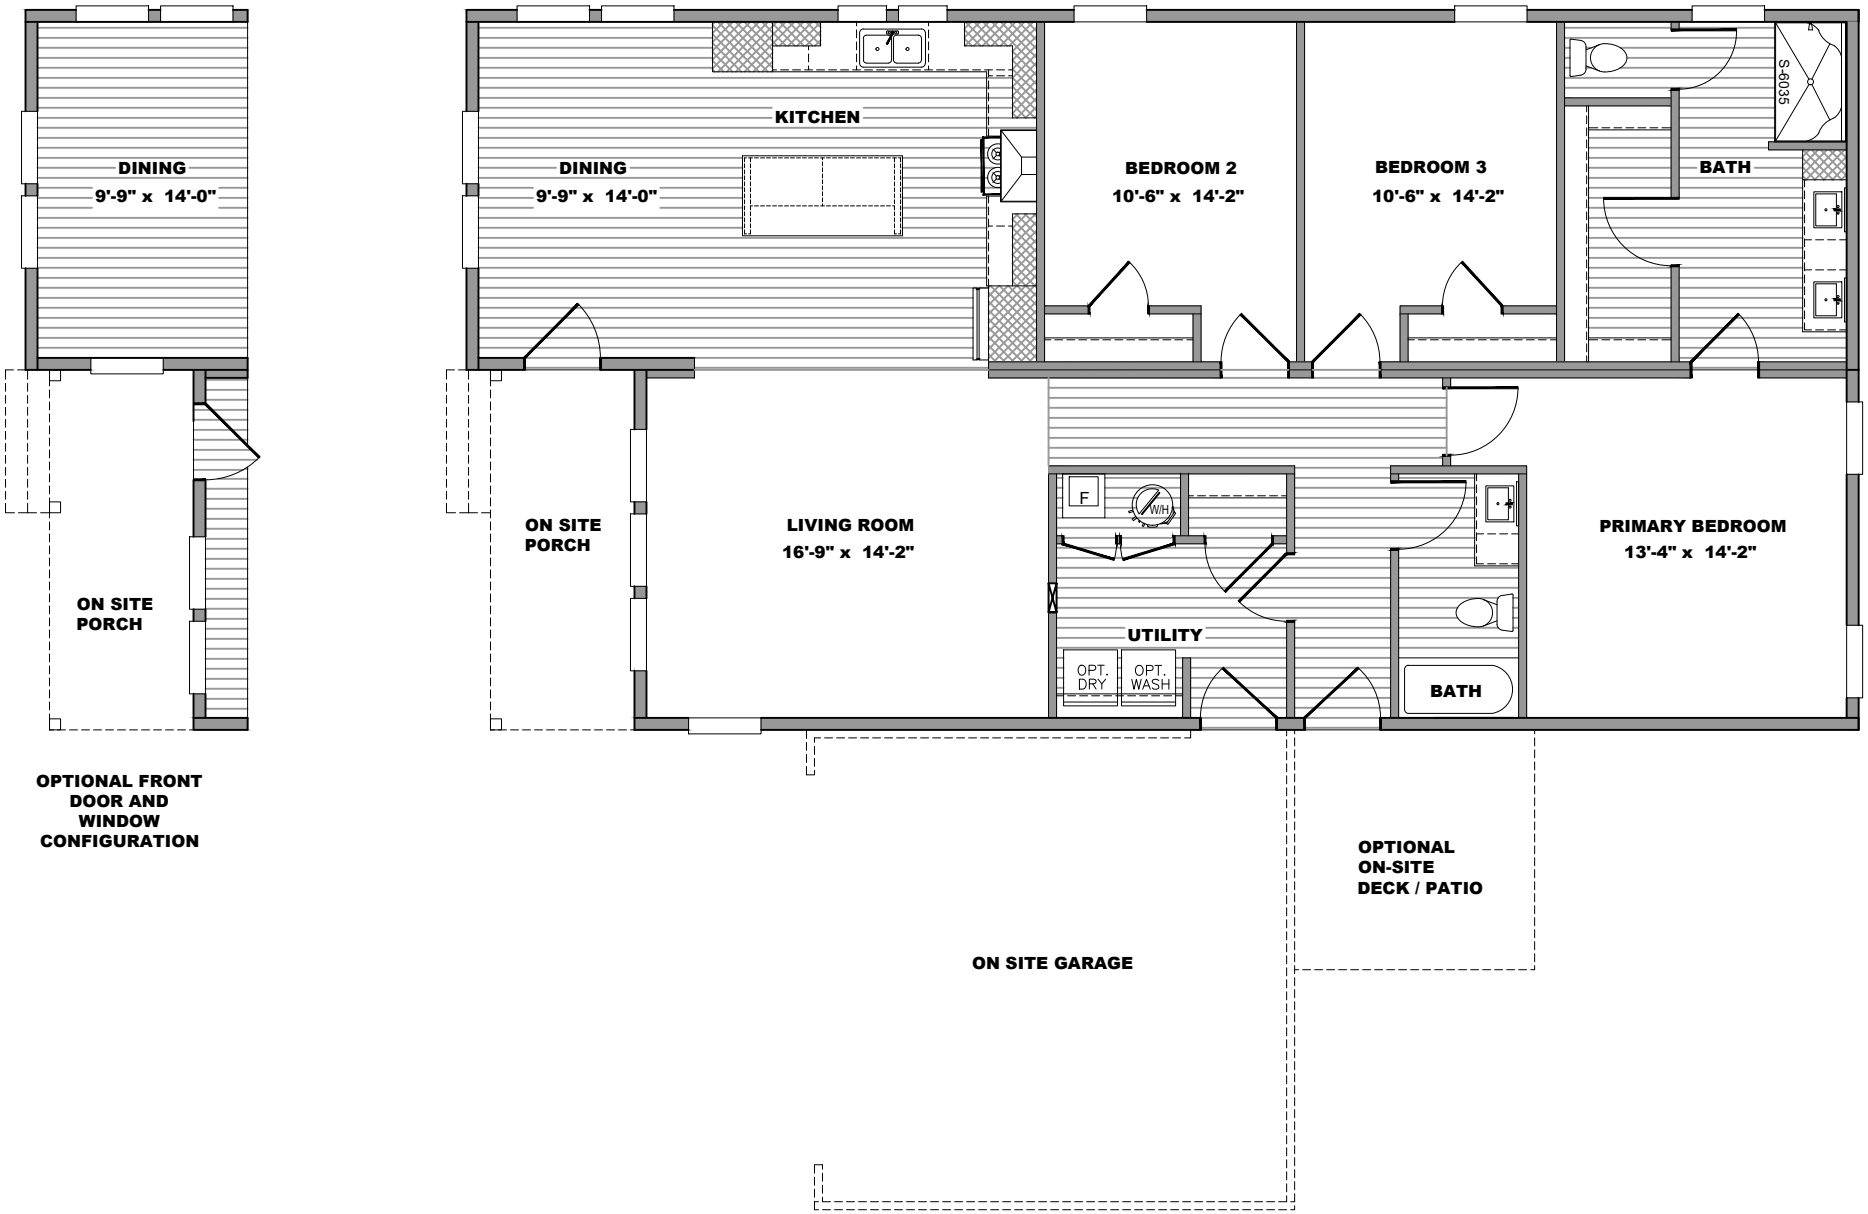

MODEL #BLN-3258-32-1 SQ.FT. 1,635 DRAWING # BLN-3258-32-1_KEENELAND_R

File Path:B:\Architecture\CrossMod\DWG Files\3258_KEENELAND\BLN-3258-32-1_Keeneland_R.dwg, Last Saved By:HutsellA, Saved Date:4/25/2024 11:46 AM, Date Printed:4/25/24 3:46 PM